



BASEMENT -
RENOVATION LAYOUT

BF-PP-01

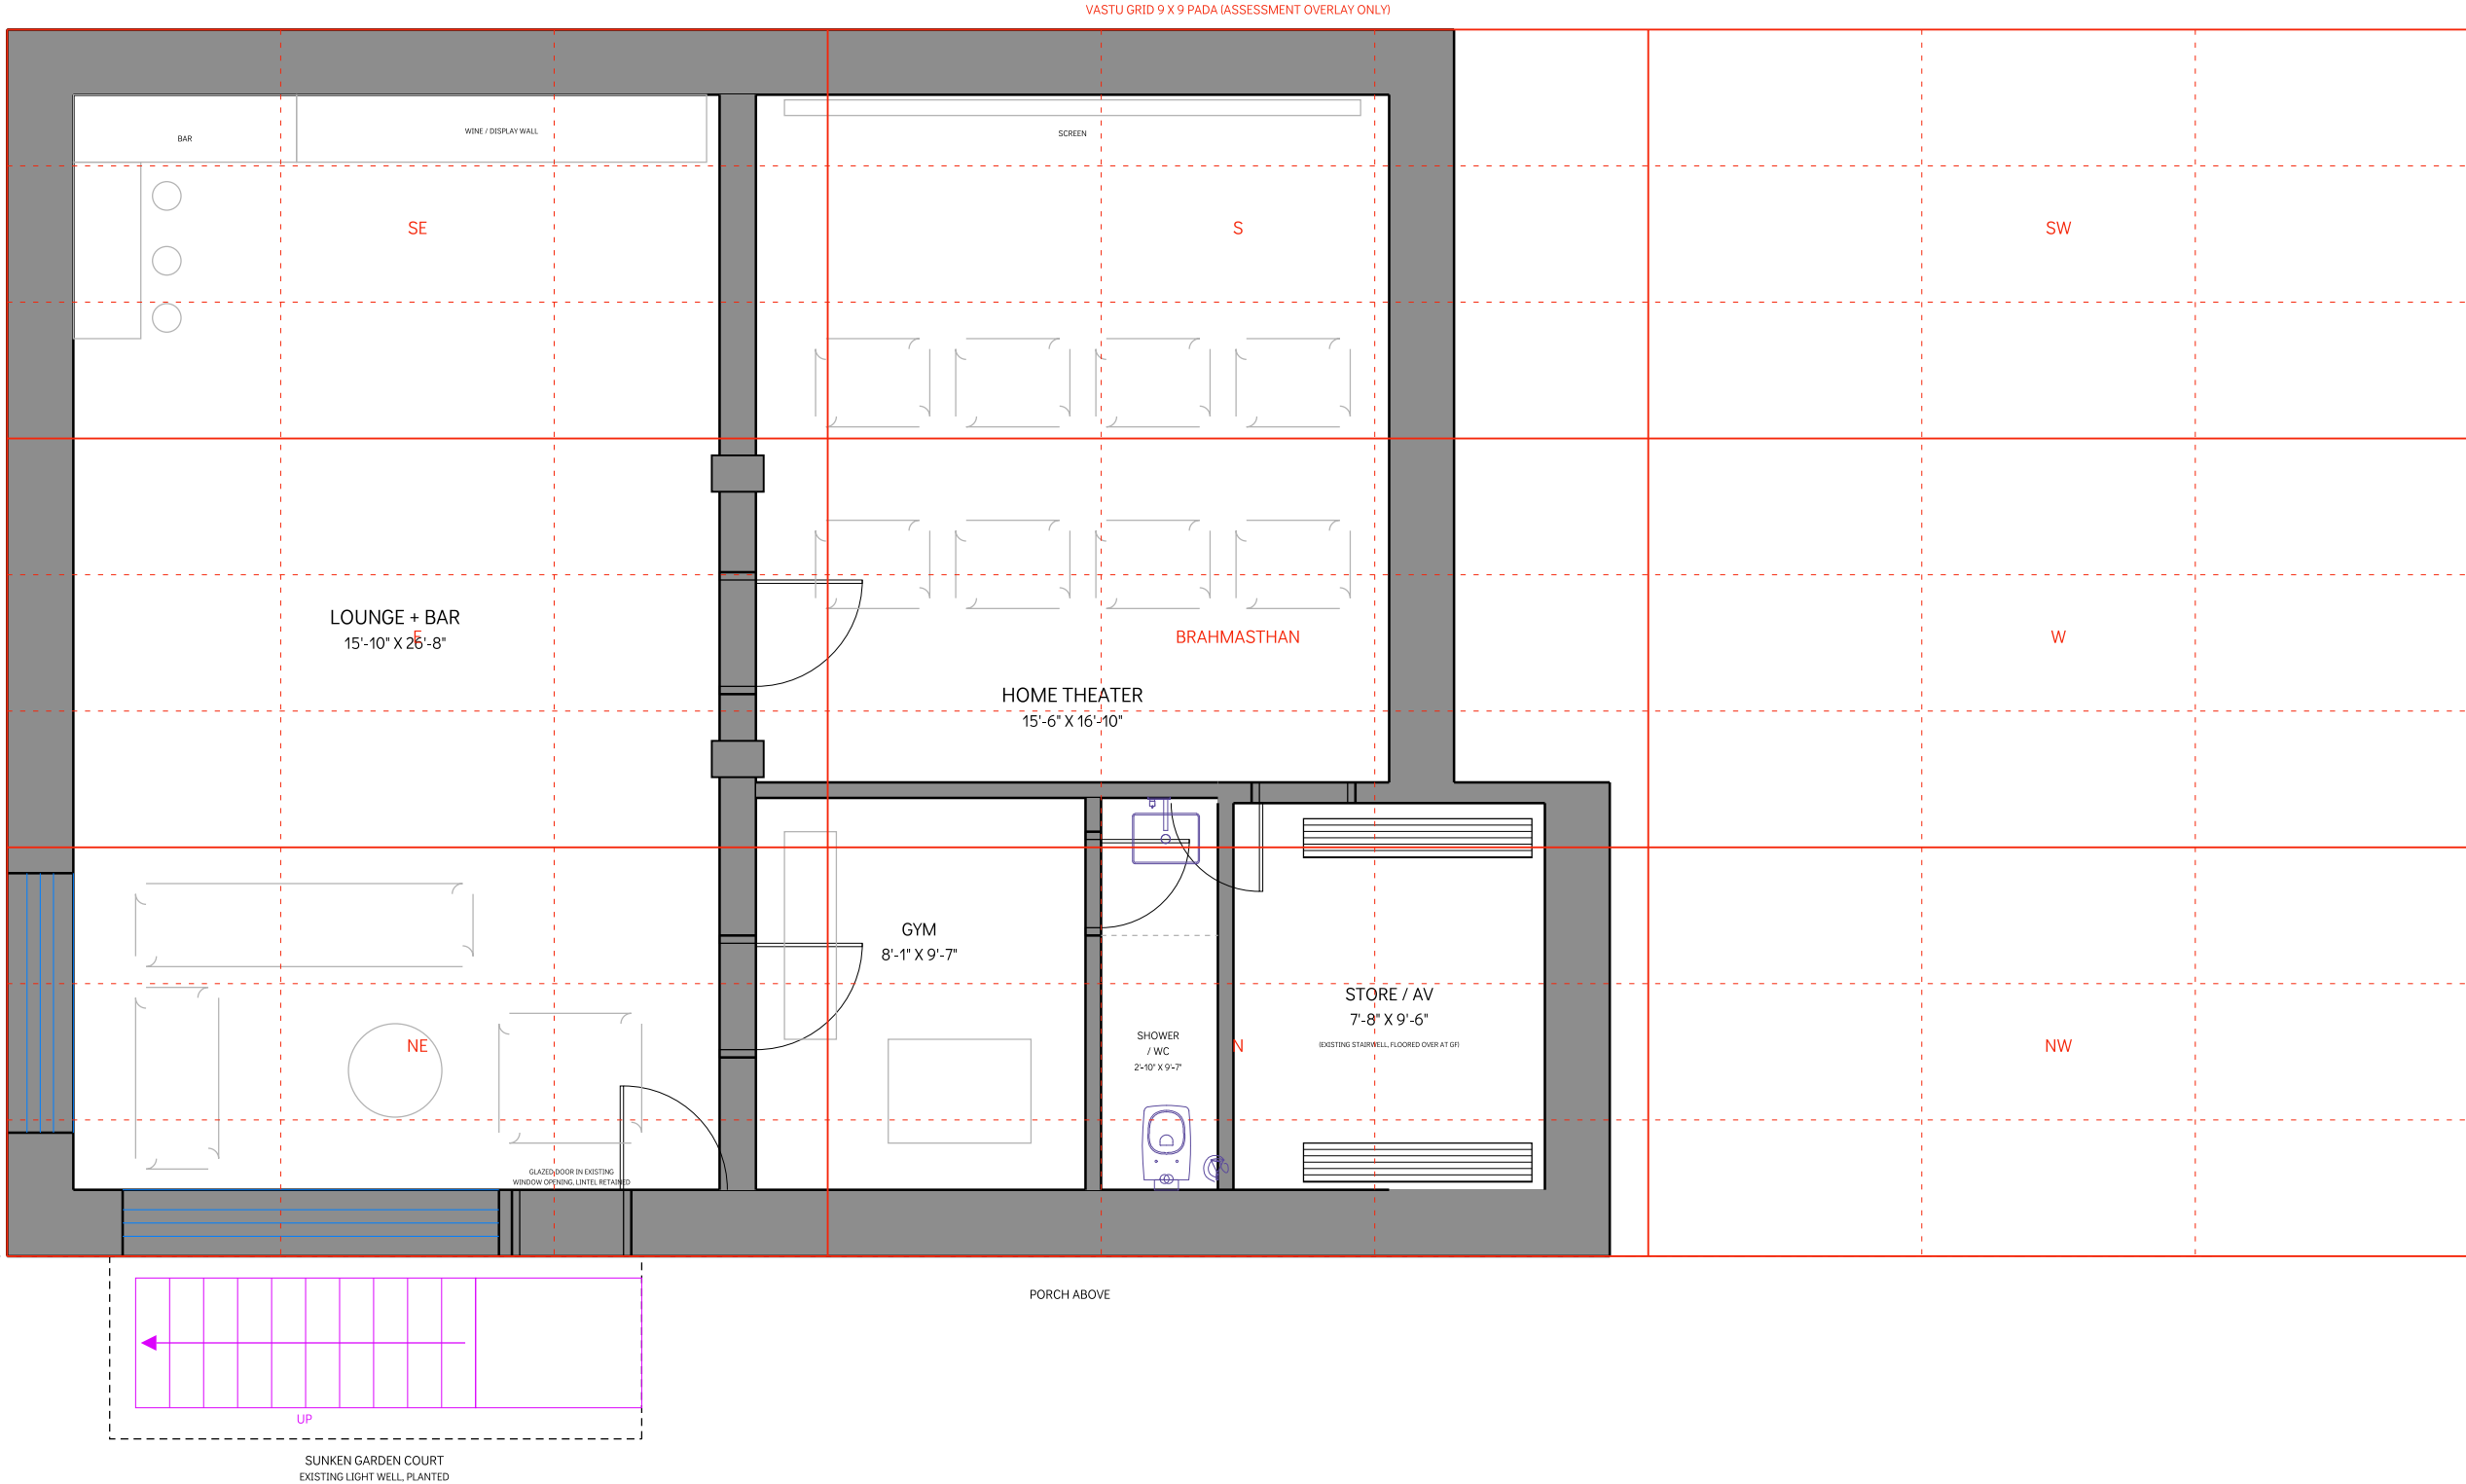


- NOTES (BASEMENT):
- Existing stairwell floored over at ground floor level; the well below becomes the store / AV room; the courtyard planter above it is waterproofed.
 - Existing north window converted to a glazed door; sill masonry removed, existing lintel retained.
 - New external stair inside the existing sunken light well, approx. 10 risers, 3'-6" wide, with canopy and floor trap.
 - Existing ceiling height 8'-6". Existing RCC columns and hidden beam on the centre line are retained; theater partition is non-load-bearing.
 - No new opening in the ground floor slab. Existing basement windows and walls otherwise unchanged.

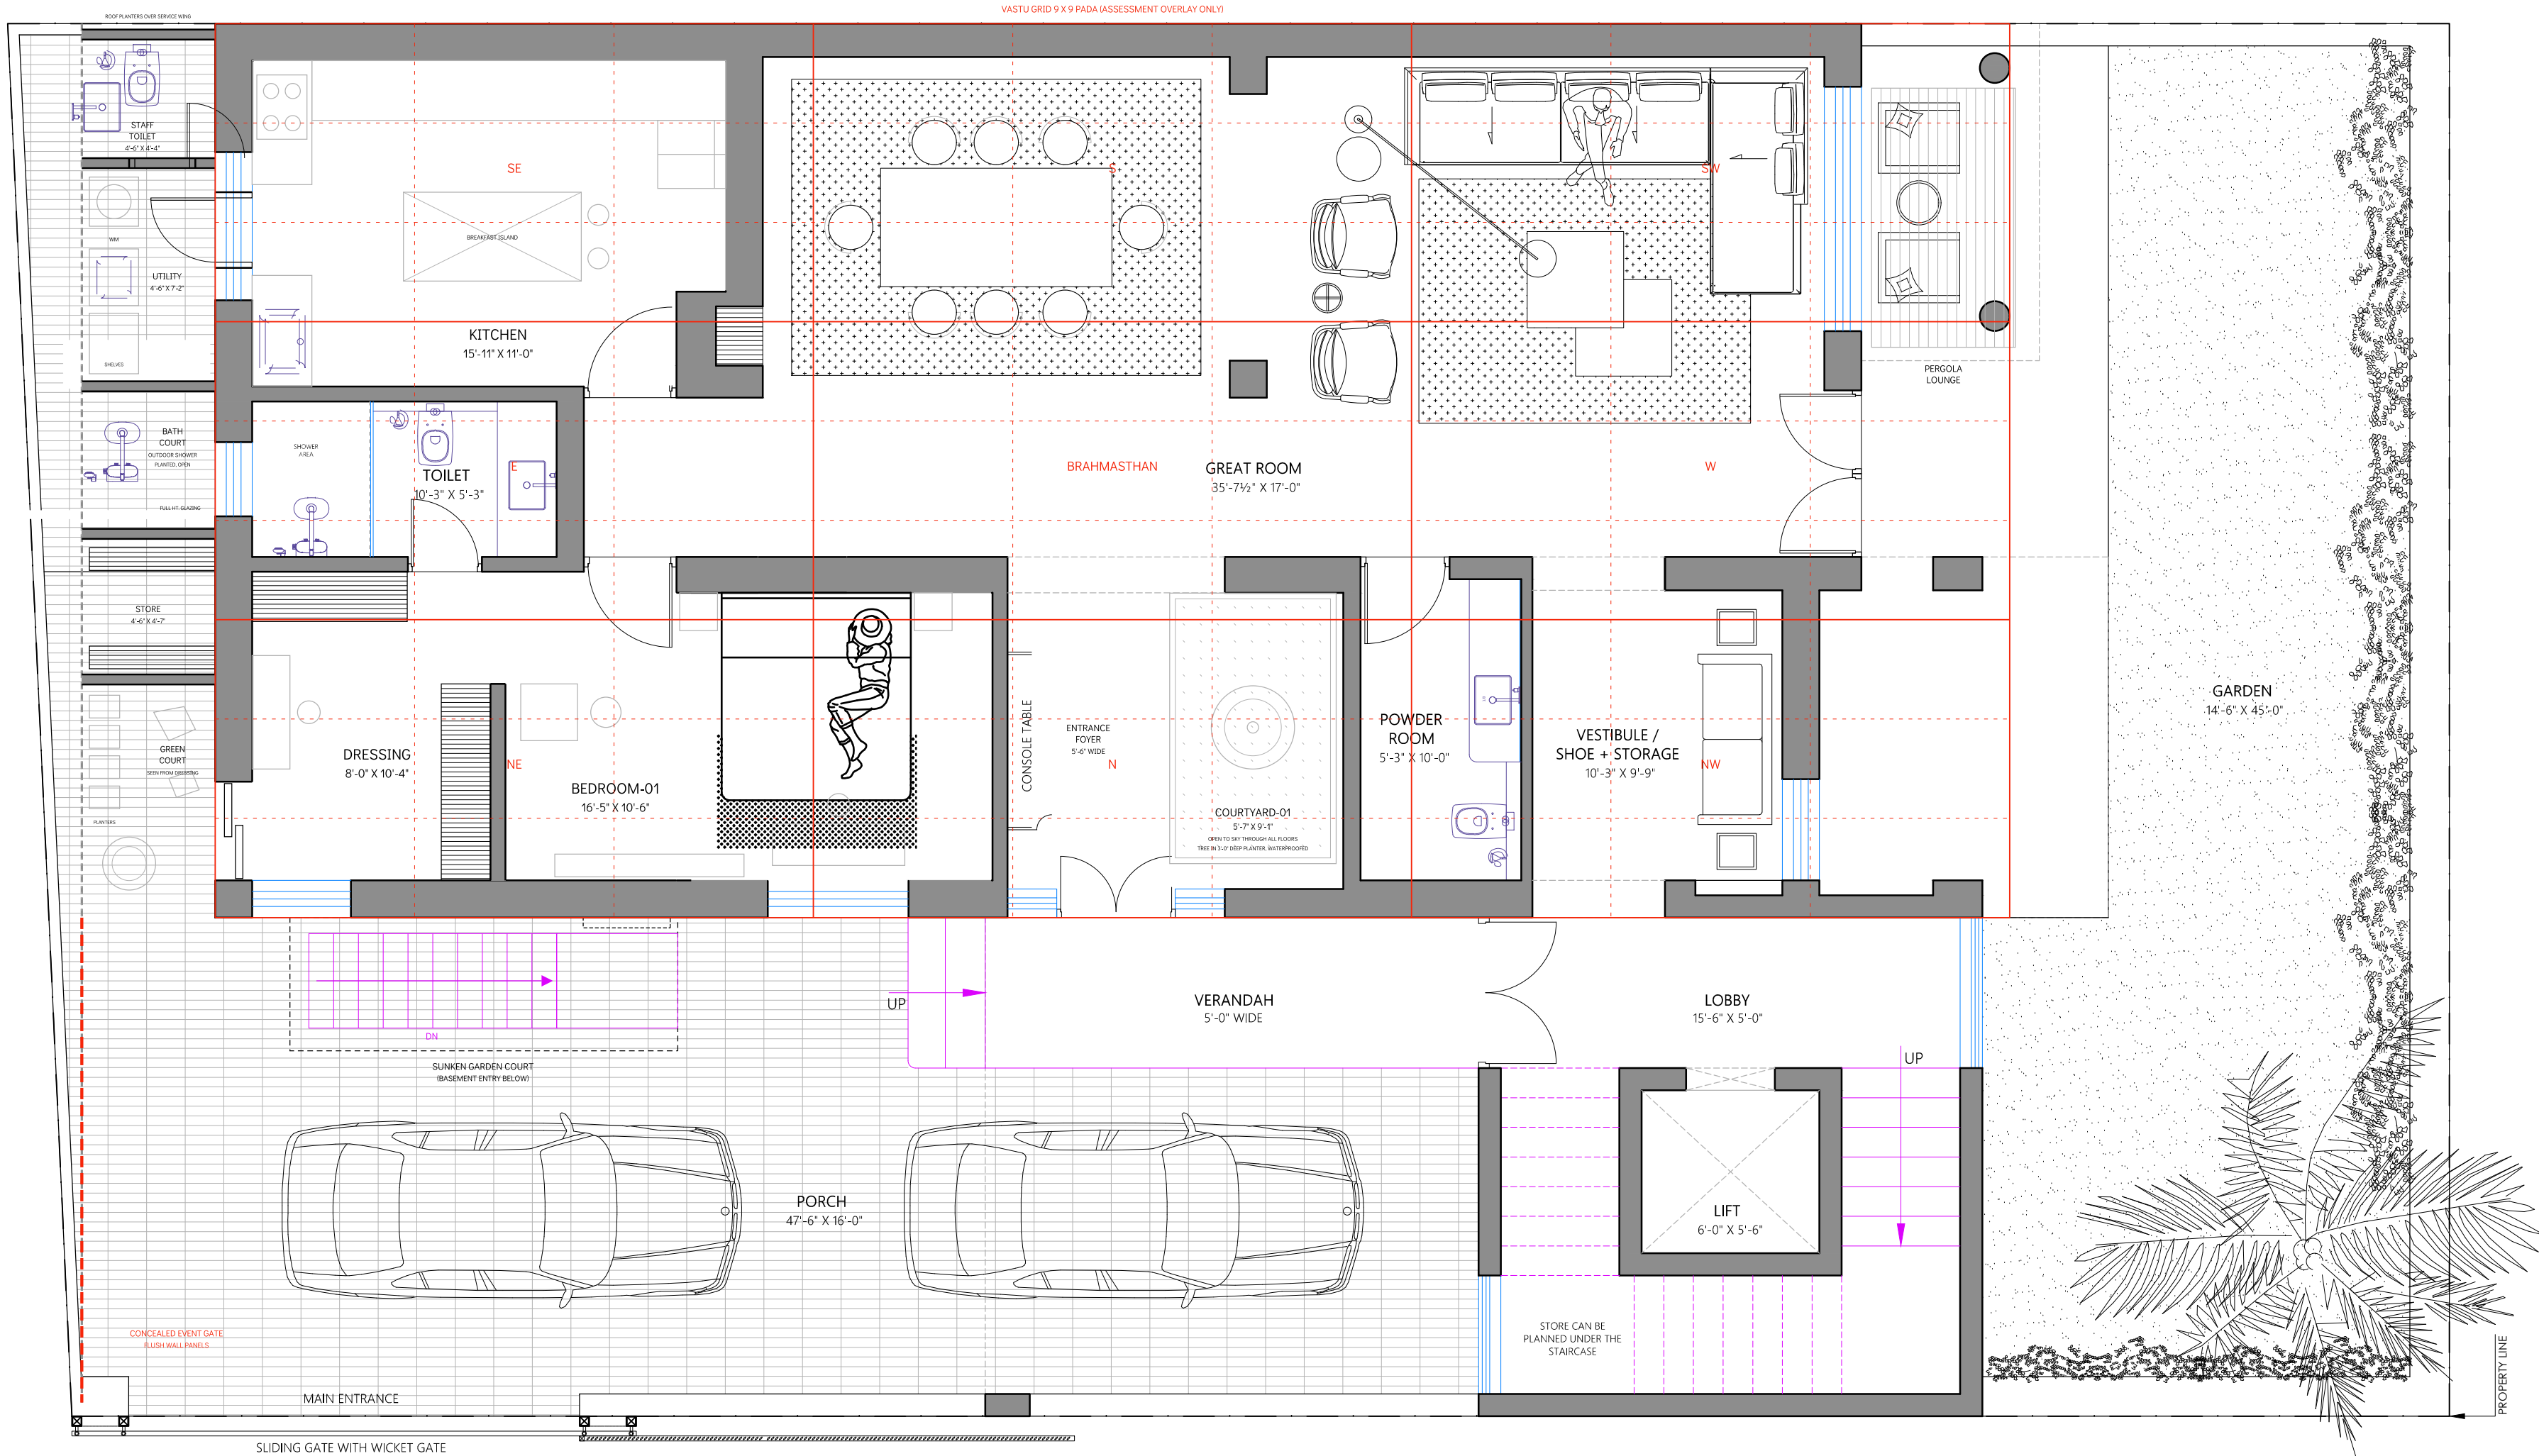

- NOTES:
1. Read this drawing along with relevant architectural, structural or service drawings.
 2. Do not scale; drawing should be read only.
 3. Any discrepancy to be brought to the notice of the architect before commencement of work.
 4. This drawing is a property of Ar. Akash Purohit and shall not be used or reproduced in any manner without the permission of the architects.

PROJECT:
17- CHANDRA PATH

SHEET TITLE:
**GROUND FLOOR -
RENOVATION LAYOUT**

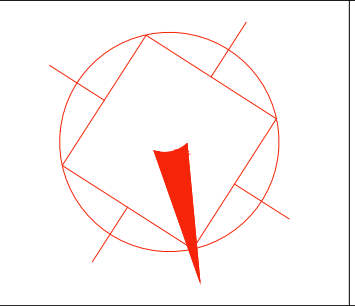

DRAWING NO:
GF-PP-01

DEALT BY:
KAPIL

CHECKED BY:
AKASH

SCALE:
N.T.S.

DATE:
15-09-2026

FILE PATH:

studio sqft

AR. AKASH PUROHIT
ar.akashpurohit@gmail.com
9784784226

NOTES (REVISION R3):
A. EAST BOUNDARY WALL TO BE REBUILT STRAIGHT AND PARALLEL TO THE HOUSE (SHOWN DASHED AT THE WIDEST OFFSET); SIDE COURTS SET OUT FROM THE NEW WALL.
B. CONCEALED EVENT GATE IN THE EAST BOUNDARY WALL FROM THE HOUSE CORNER TO THE FRONT BOUNDARY: FLUSH WALL-FINISHED PANELS ON CONCEALED PIVOTS, OPENED ONLY FOR EVENTS.
C. COURTYARD-01: OPEN TO SKY THROUGH FIRST, SECOND AND TERRACE FLOORS WITHIN THE EXISTING STAIRWELL SHAFT; NO NEW SLAB OPENINGS. GLASS BALUSTRADE AT EACH FLOOR.
D. SERVICE WING ALONG THE FULL EAST SIDE (STAFF TOILET, UTILITY, BATH COURT, STORE, GREEN COURT); 4'-6" WIDE FROM THE STRAIGHTENED WALL; KITCHEN/UTILITY DOOR CUT BELOW THE EXISTING WINDOW; LINTEL RETAINED.
E. SERVICE WING ROOF AT 7'-6" WITH A CONTINUOUS PLANTER PARAPET (GREEN VIEW FROM KITCHEN, BATH AND DRESSING TOWARDS THE PARK SIDE); STAFF ROOM ON THE TERRACE FLOOR BESIDE THE MUMTY (SEE TF-PP-01).
F. VASTU GRID (RED) IS AN ASSESSMENT OVERLAY ONLY. SHEET ORIENTATION: TOP = SOUTH, BOTTOM = NORTH, LEFT = EAST, RIGHT = WEST.

- NOTES:
1. Read this drawing along with relevant architectural, structural or service drawings.
 2. Do not scale; drawing should be read only.
 3. Any discrepancy to be brought to the notice of the architect before commencement of work.
 4. This drawing is a property of Ar. Akash Purohit and shall not be used or reproduced in any manner without the permission of the architects.

PROJECT:
17- CHANDRA PATH

SHEET TITLE:
**FIRST FLOOR -
RENOVATION LAYOUT**

DRAWING NO:
FF-PP-01


DEALT BY: KAPIL	CHECKED BY: AKASH
--------------------	----------------------

SCALE: N.T.S.	DATE: 15-09-2026
------------------	---------------------

FILE PATH:


studio sqft

AR. AKASH PUROHIT
ar.akashpurohit@gmail.com
9784784226

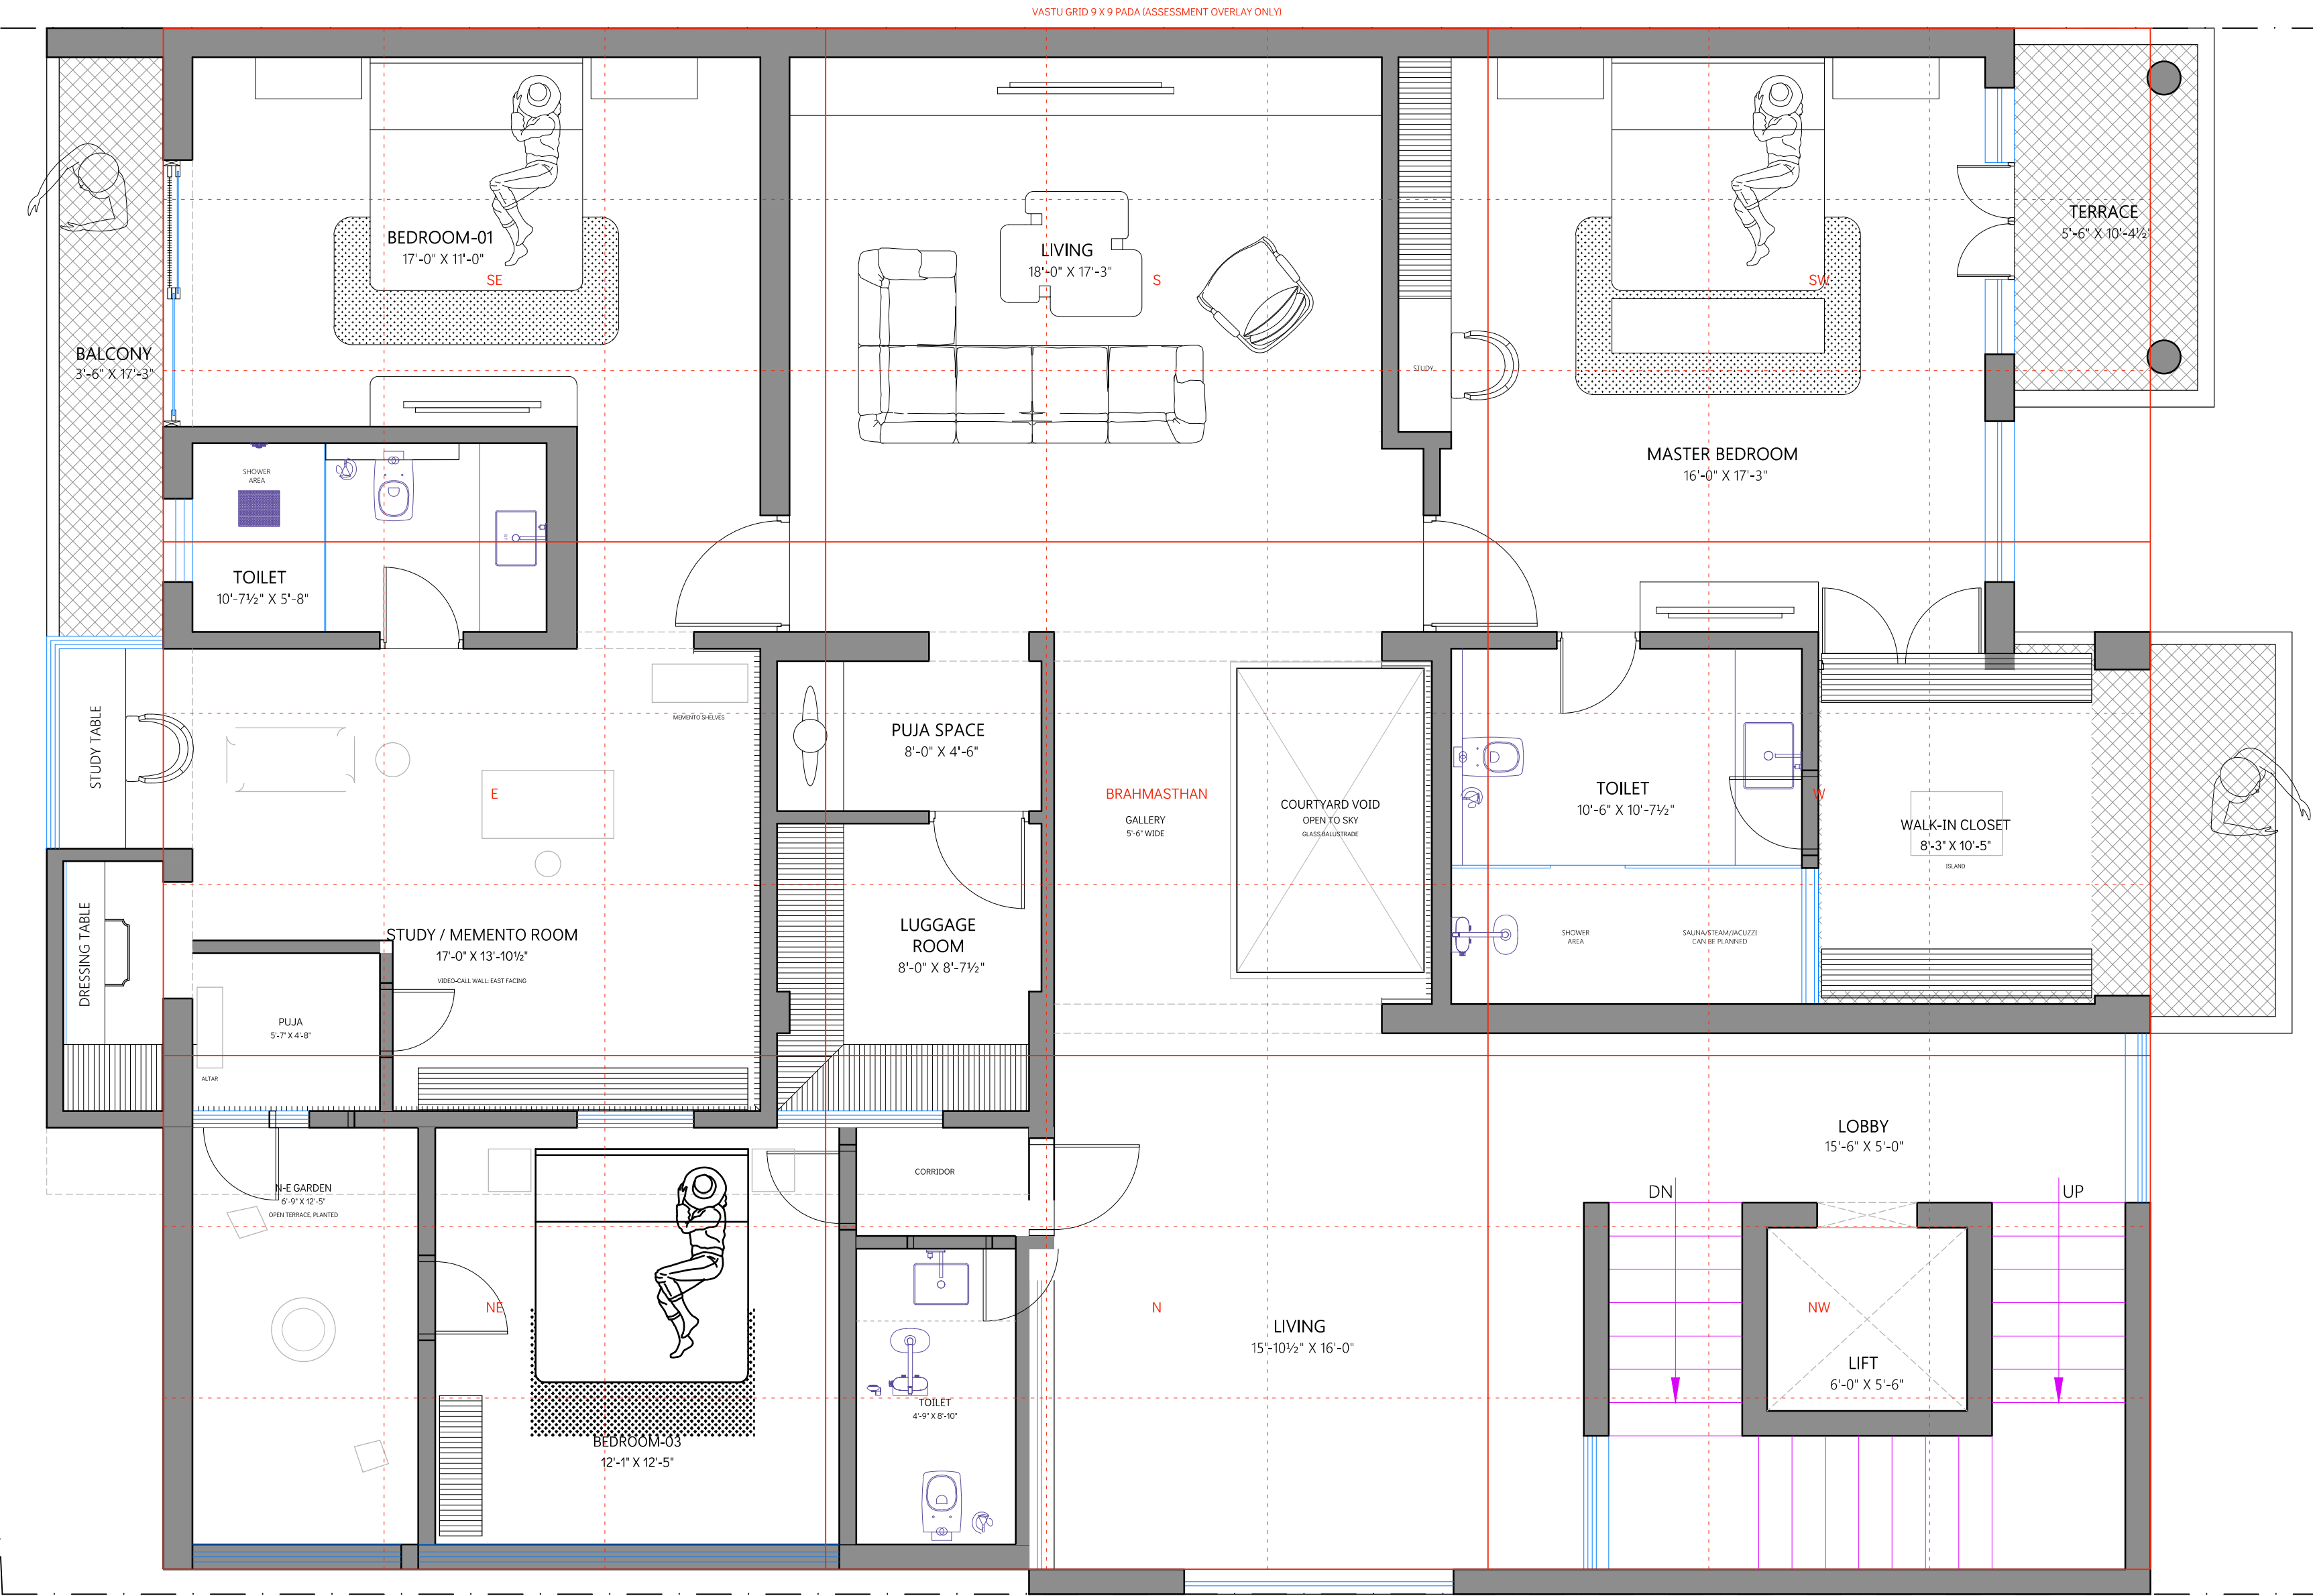

NOTES (FIRST FLOOR, R3):

1. NEW SLAB OVER THE PORCH EXTENDED EAST TO THE HOUSE LINE, SUPPORTED ON THE EXISTING NORTH WALL AND NEW COLUMNS ON THE PORCH LINE, TO STRUCTURAL DESIGN.
2. FORMER WEST TERRACE ENCLOSED AS MASTER WALK-IN CLOSET (LIGHT PARTITIONS ON EXISTING SLAB). 3. NORTH-EAST ROOM RE-PURPOSED AS STUDY WITH PUJA IN ITS NORTH-EAST CORNER.
4. COURTYARD VOID WITHIN THE EXISTING STAIRWELL SHAFT; GLASS BALUSTRADE. 5. VASTU GRID (RED) IS AN ASSESSMENT OVERLAY ONLY.

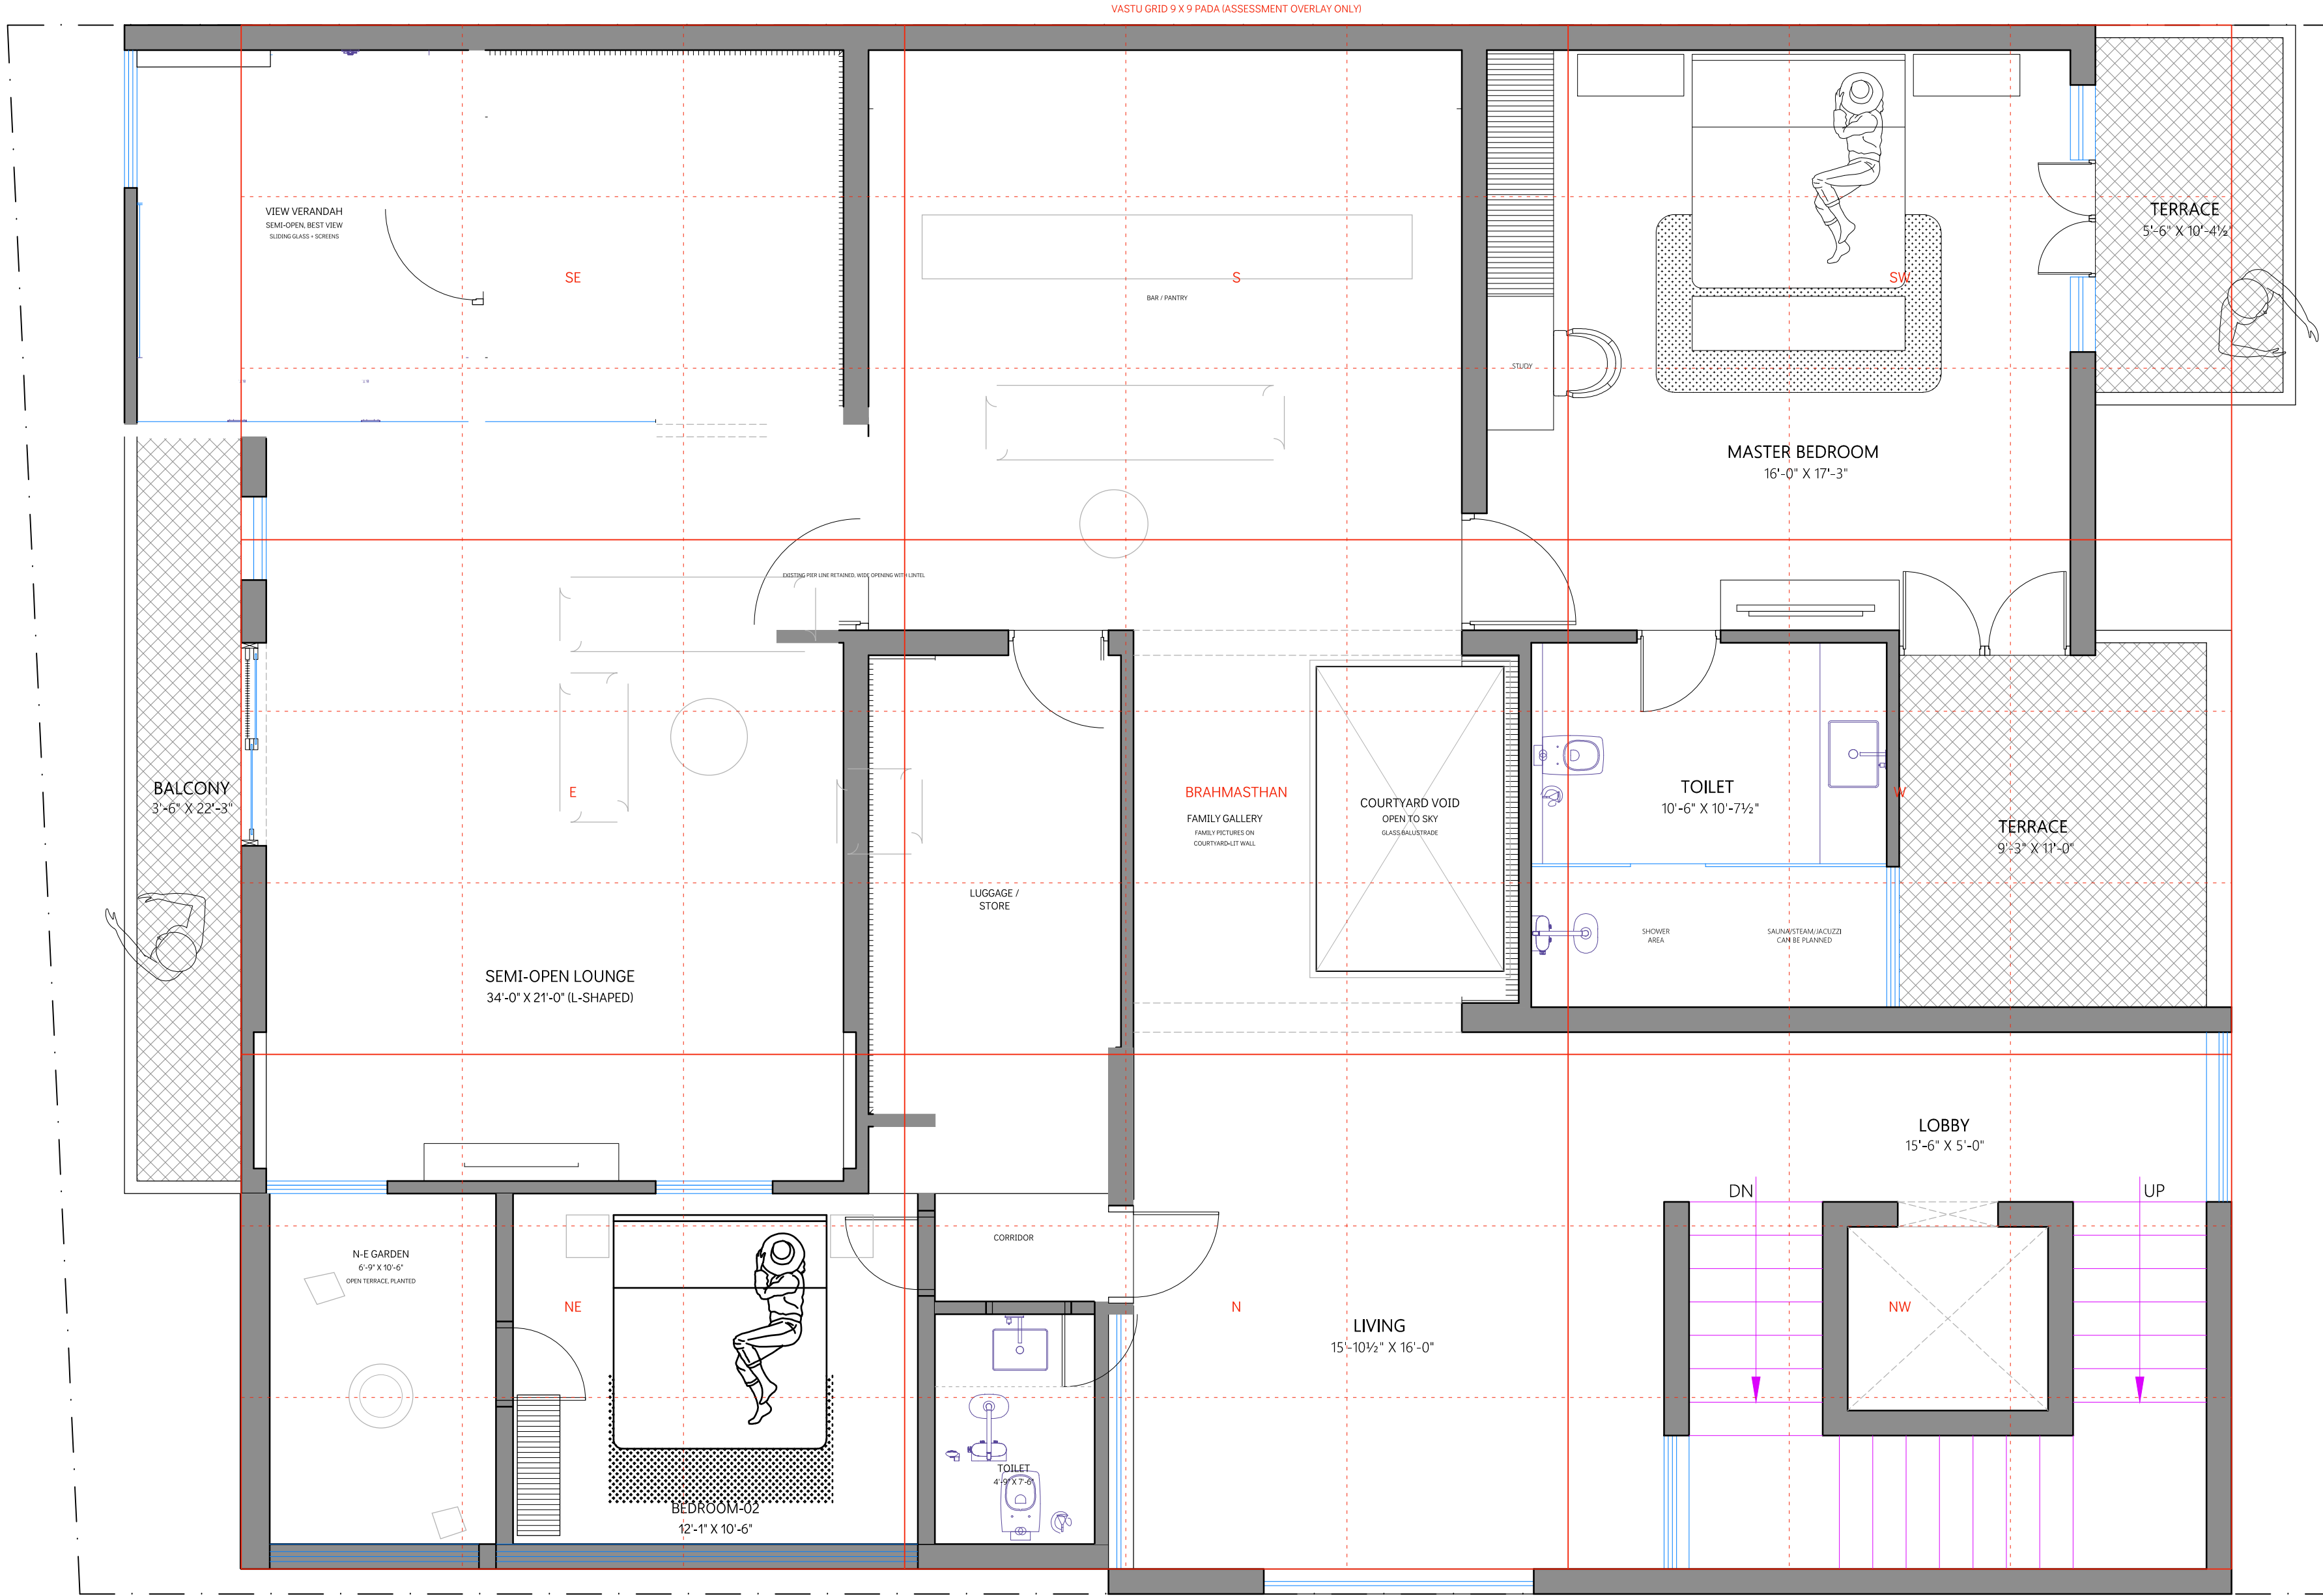


NOTES (SECOND FLOOR, R3):
1. SOUTH-EAST TOILET, WALK-IN CLOSET AND BEDROOM-02 REMOVED; AREA BECOMES A SEMI-OPEN LOUNGE WITH THE VIEW VERANDAH AT THE SOUTH-EAST.
2. BEDROOM-02 AND ITS TOILET RELOCATED TO THE NEW NORTH WING OVER THE PORCH (NORTH ZONE). 3. STRUCTURAL WALL LINES RETAINED AS PIERS; OPENINGS WITH LINTELS.
4. FAMILY GALLERY ALONG THE COURTYARD VOID. 5. VASTU GRID (RED) IS AN ASSESSMENT OVERLAY ONLY.

- NOTES:
1. Read this drawing along with relevant architectural, structural or service drawings.
 2. Do not scale; drawing should be read only.
 3. Any discrepancy to be brought to the notice of the architect before commencement of work.
 4. This drawing is a property of Ar. Akash Purohit and shall not be used or reproduced in any manner without the permission of the architects.

PROJECT:
17- CHANDRA PATH

SHEET TITLE:
SECOND FLOOR- LAYOUT

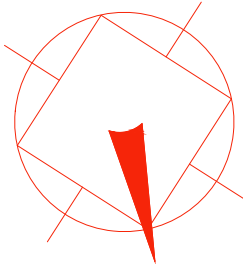

DRAWING NO:
SF-PP-01

DEALT BY:
KAPIL

CHECKED BY:
AKASH


SCALE:
N.T.S.

DATE:
15-09-2026

FILE PATH:

studio sqft

AR. AKASH PUROHIT
ar.akashpurohit@gmail.com
9784784226

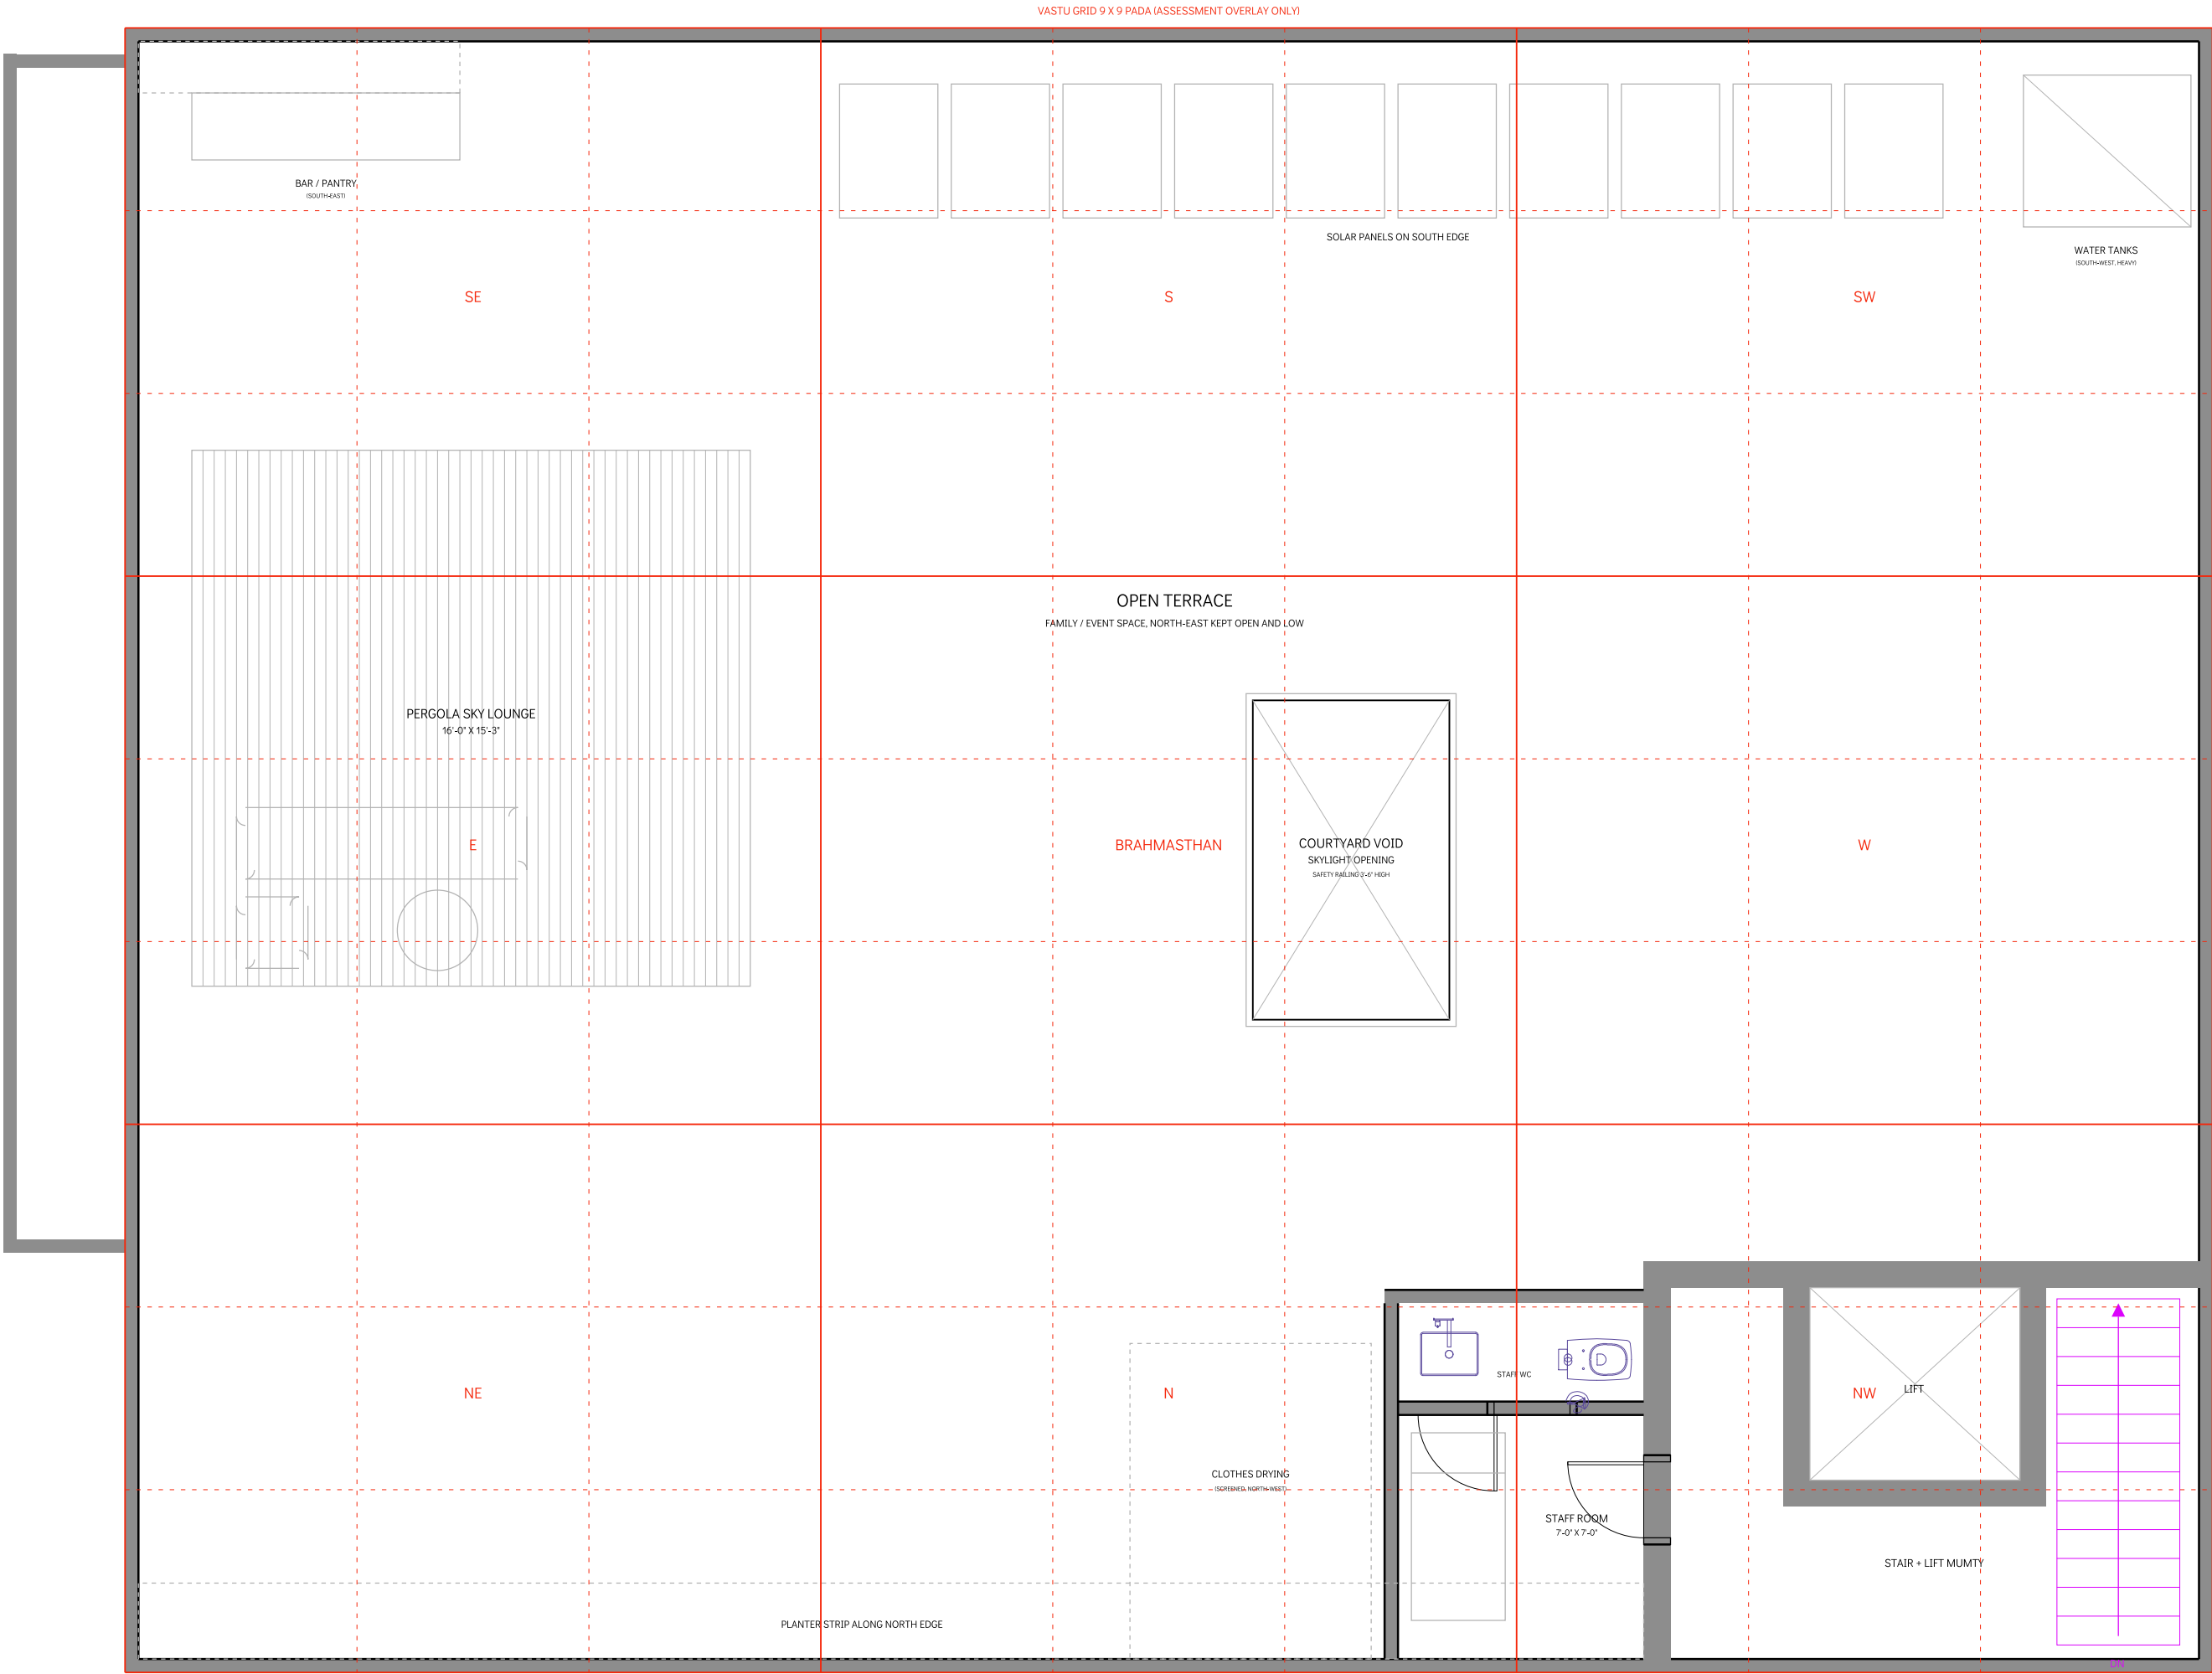

TERRACE FLOOR - LAYOUT

TF-PP-01

NOTES (TERRACE, R3):
1. PARAPET 3'-6" HIGH ALL ROUND; COURTYARD VOID RAILED; 2. WATER TANKS AND PLANT IN THE SOUTH-WEST; SOLAR ARRAY ALONG THE SOUTH PARAPET; NORTH-EAST KEPT OPEN AND LOW (VASTU).
3. PERGOLA LOUNGE ON THE EAST; BAR AT THE SOUTH-EAST; 4. STAFF ROOM, WC AND SCREENED DRYING YARD BESIDE THE MUMTY (NORTH-WEST); 5. WATERPROOFING AND SLOPES TO NORTH-EAST DRAIN POINTS; 6. VASTU GRID (RED) IS AN ASSESSMENT OVERLAY ONLY.