



BASEMENT -
RENOVATION LAYOUT

BF-PP-01

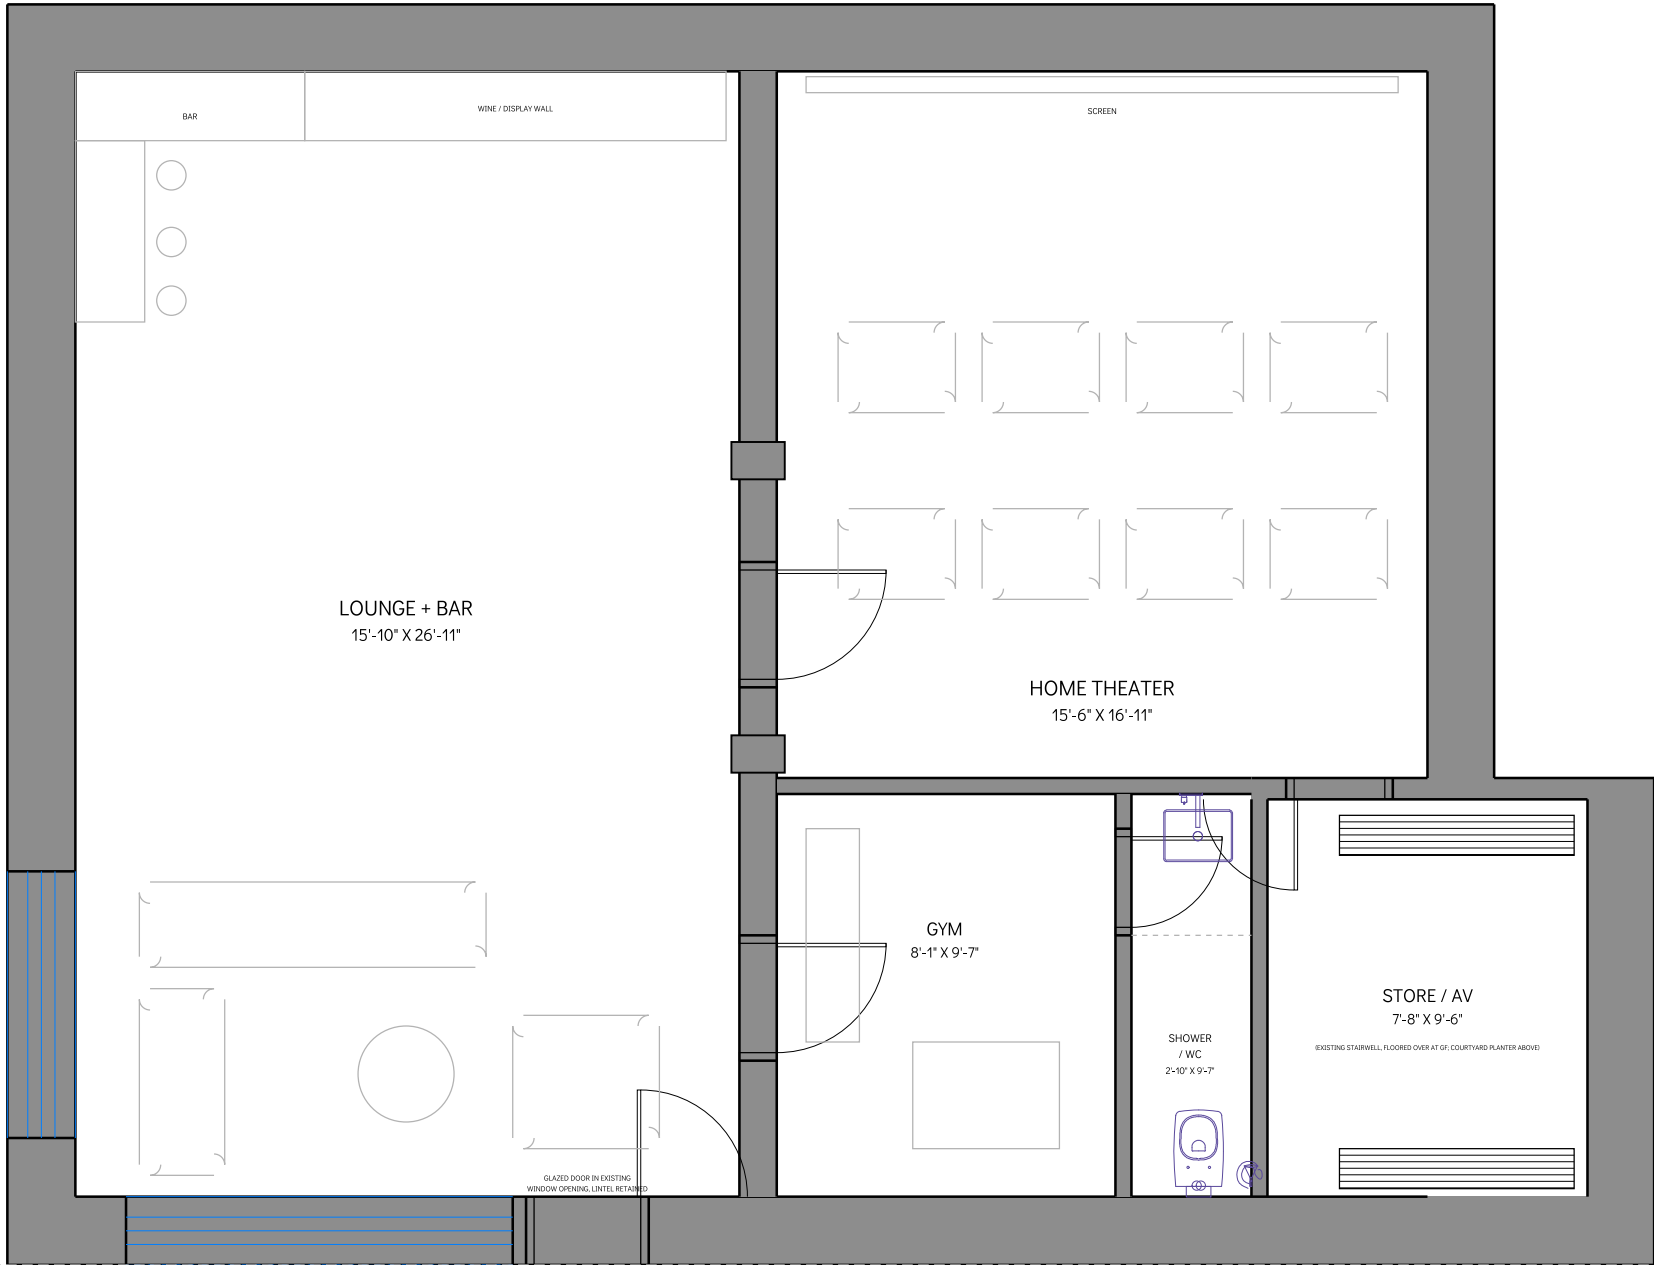

- NOTES (BASEMENT):
- Existing stairwell floored over at ground floor level; the well below is the store / AV room; the courtyard planter above it is waterproofed. The Brahmasthan above stays open.
 - Basement entry by the stair in the west part of the existing north light well (north padas 3-4, outside the Brahmasthan and the north-east); north window opening converted to a glazed door, sill masonry removed, lintel retained.
 - The servant room is at grade on the east side (see GF-PP-01), not at this level.
 - Existing ceiling height 8'-6". Existing RCC columns and hidden beam on the centre line are retained; theater partition is non-load-bearing.
 - No new opening in the ground floor slab. Existing basement windows and walls otherwise unchanged.

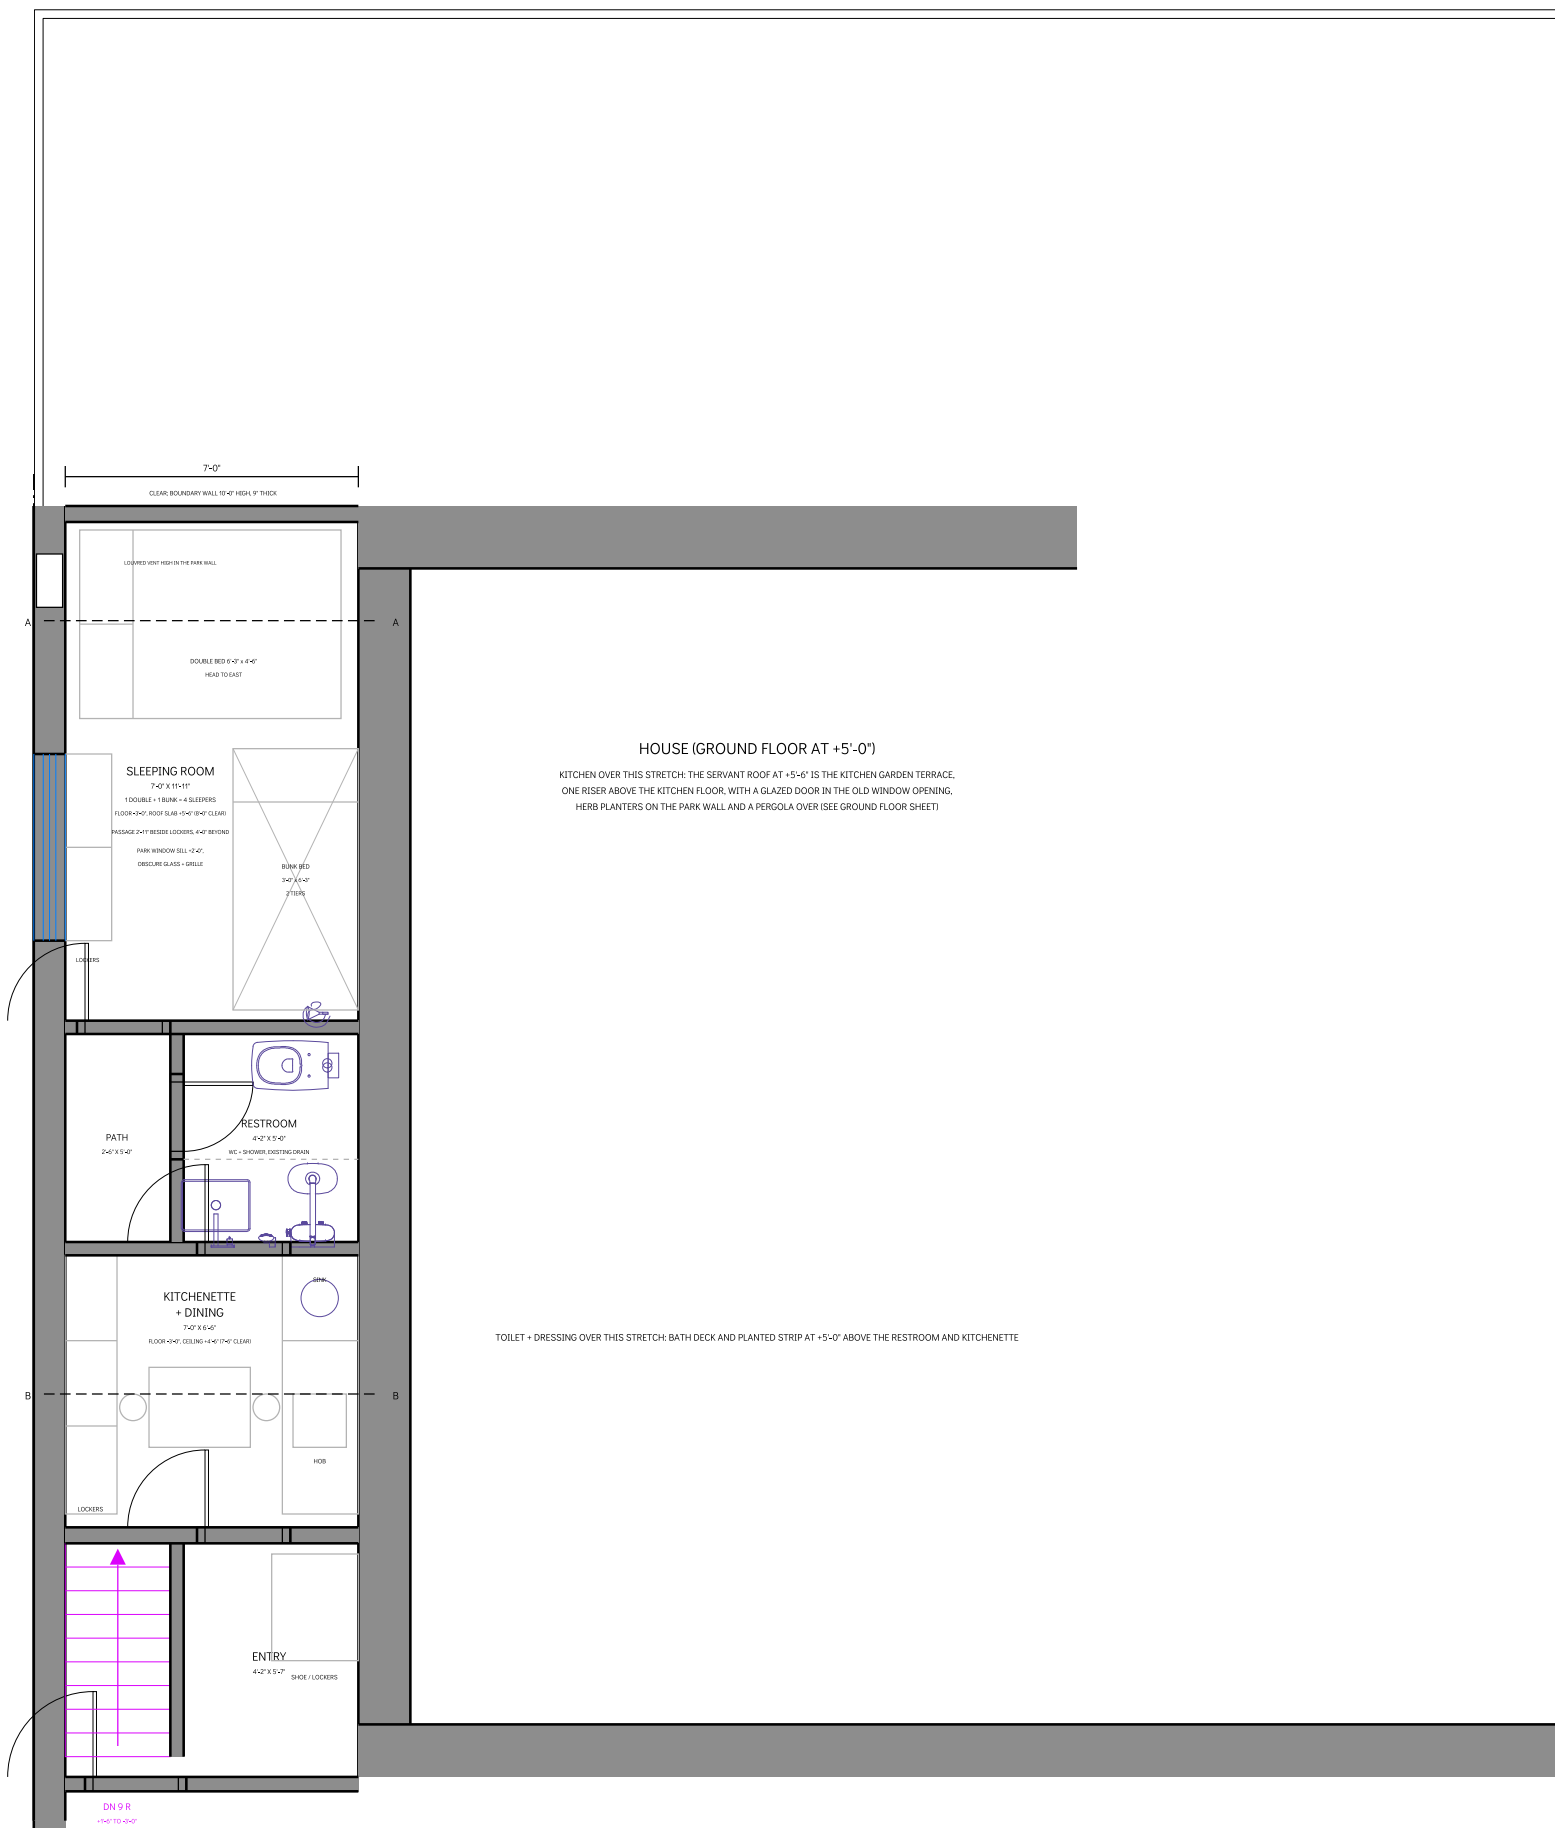

HOUSE (GROUND FLOOR AT +5'-0")



KITCHEN OVER THIS STRETCH THE SERVANT RESTROOM AT +5'-0" IS THE KITCHEN GARDEN TERRACE, ONE RISER ABOVE THE KITCHEN FLOOR, WITH A GLAZED DOOR IN THE OLD WINDOW OPENING, HERB PLANTERS ON THE PARK WALL AND A PERGOLA OVER (SEE GROUND FLOOR SHEET).

TOILET + DRESSING OVER THIS STRETCH: BATH DECK AND PLANTED STRIP AT -5'-0" ABOVE THE RESTROOM AND KITCHENETTE

PORCH (+1'-6")

NOTES (SERVANT QUARTERS):

1. EXISTING SERVANT ROOM AND RESTROOM DEMOLISHED; STRIP REBUILT WITH ITS FLOOR AT -3'-0" THROUGHOUT (RETAINING WALLS, WATERPROOFED, SUMP + PUMP FOR DRAINAGE).
2. ENTRY FROM THE PORCH END ONLY, 9 RISERS DOWN INSIDE THE DOOR; NO DOOR INTO THE HOUSE.
3. SLEEPING ROOM: ONE DOUBLE BED ACROSS THE SOUTH WALL AND ONE TWO-TIER BUNK ALONG THE HOUSE WALL (4 SLEEPERS); 4'-0" PASSAGE WITH LOCKERS UNDER THE PARK WINDOW. SINGLE HEIGHT: FLOOR -3'-0"; ROOF SLAB AT +5'-6" (8'-0" CLEAR); THE ROOF IS THE KITCHEN GARDEN TERRACE, DESIGNED FOR TERRACE LIVE LOAD AND PLANTERS, WATERPROOFED, LOUVRED VENT HIGH IN THE PARK WALL FOR CROSS-VENTILATION WITH THE DOOR.
4. RESTROOM AND KITCHENETTE SIT UNDER THE GROUND-FLOOR BATH DECK AND PLANTED STRIP (+5'-0"), 7'-4" CLEAR; RESTROOM ON THE EXISTING DRAIN, HIGH-LEVEL VENT TO THE PATH.
5. PATH 2'-6" ALONG THE BOUNDARY WALL, OPEN ABOVE WHERE NO DECK; WINDOW TO THE PARK IN THE SLEEPING ROOM AS EXISTING, SILL +2'-0" (5'-0" ABOVE THE SERVANT FLOOR), OBSCURE GLASS WITH A GRILLE. ALL DIMENSIONS ARE CLEAR INTERNAL SIZES.

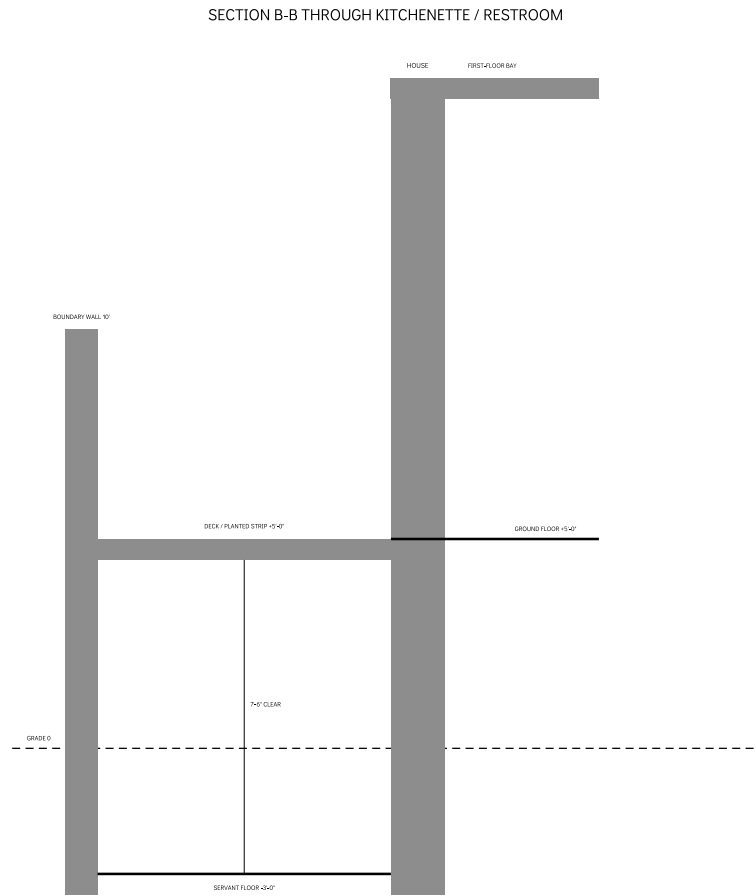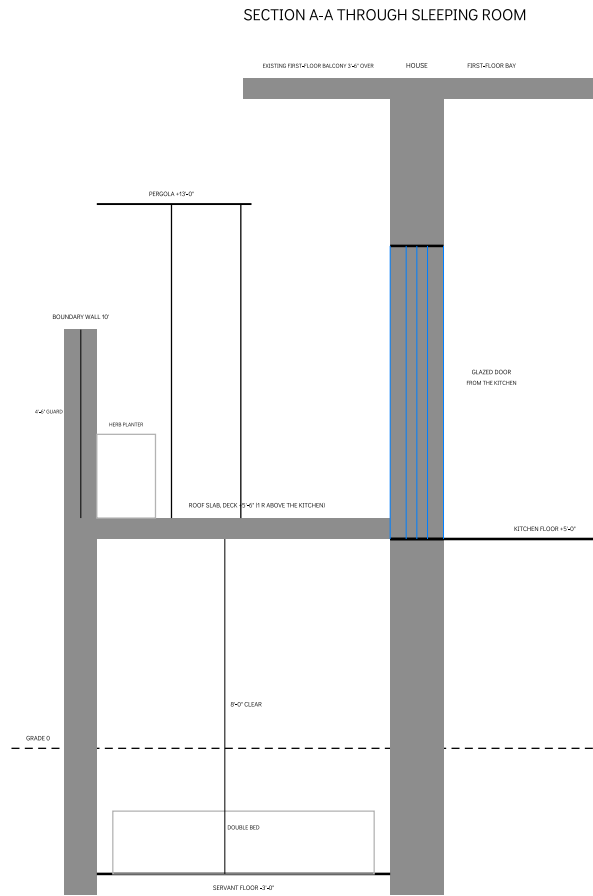

SERVANT QUARTERS - GRADE LEVEL LAYOUT

SQ-PP-03


1. Read this drawing along with relevant architectural, structural or service drawings.

3. Any discrepancy to be brought to the notice of the architect before commencement of work.

4. This drawing is a property of Ar. Akash Purohit and shall not be used or reproduced in any manner without the permission of the architects.

SHEET TITLE:

**GROUND FLOOR -
RENOVATION LAYOUT**

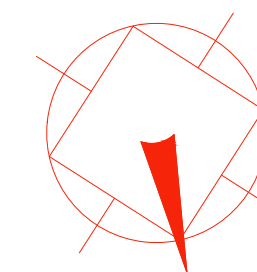DEALT BY:
KAPIL

CHECKED BY:
AKASH


SCALE:
N.T.S.

DATE:
15-09-2026

FILE PATH:

studio sqft


AR. AKASH PUROHIT
ar.akashpurohit@gmail.com
9784784226

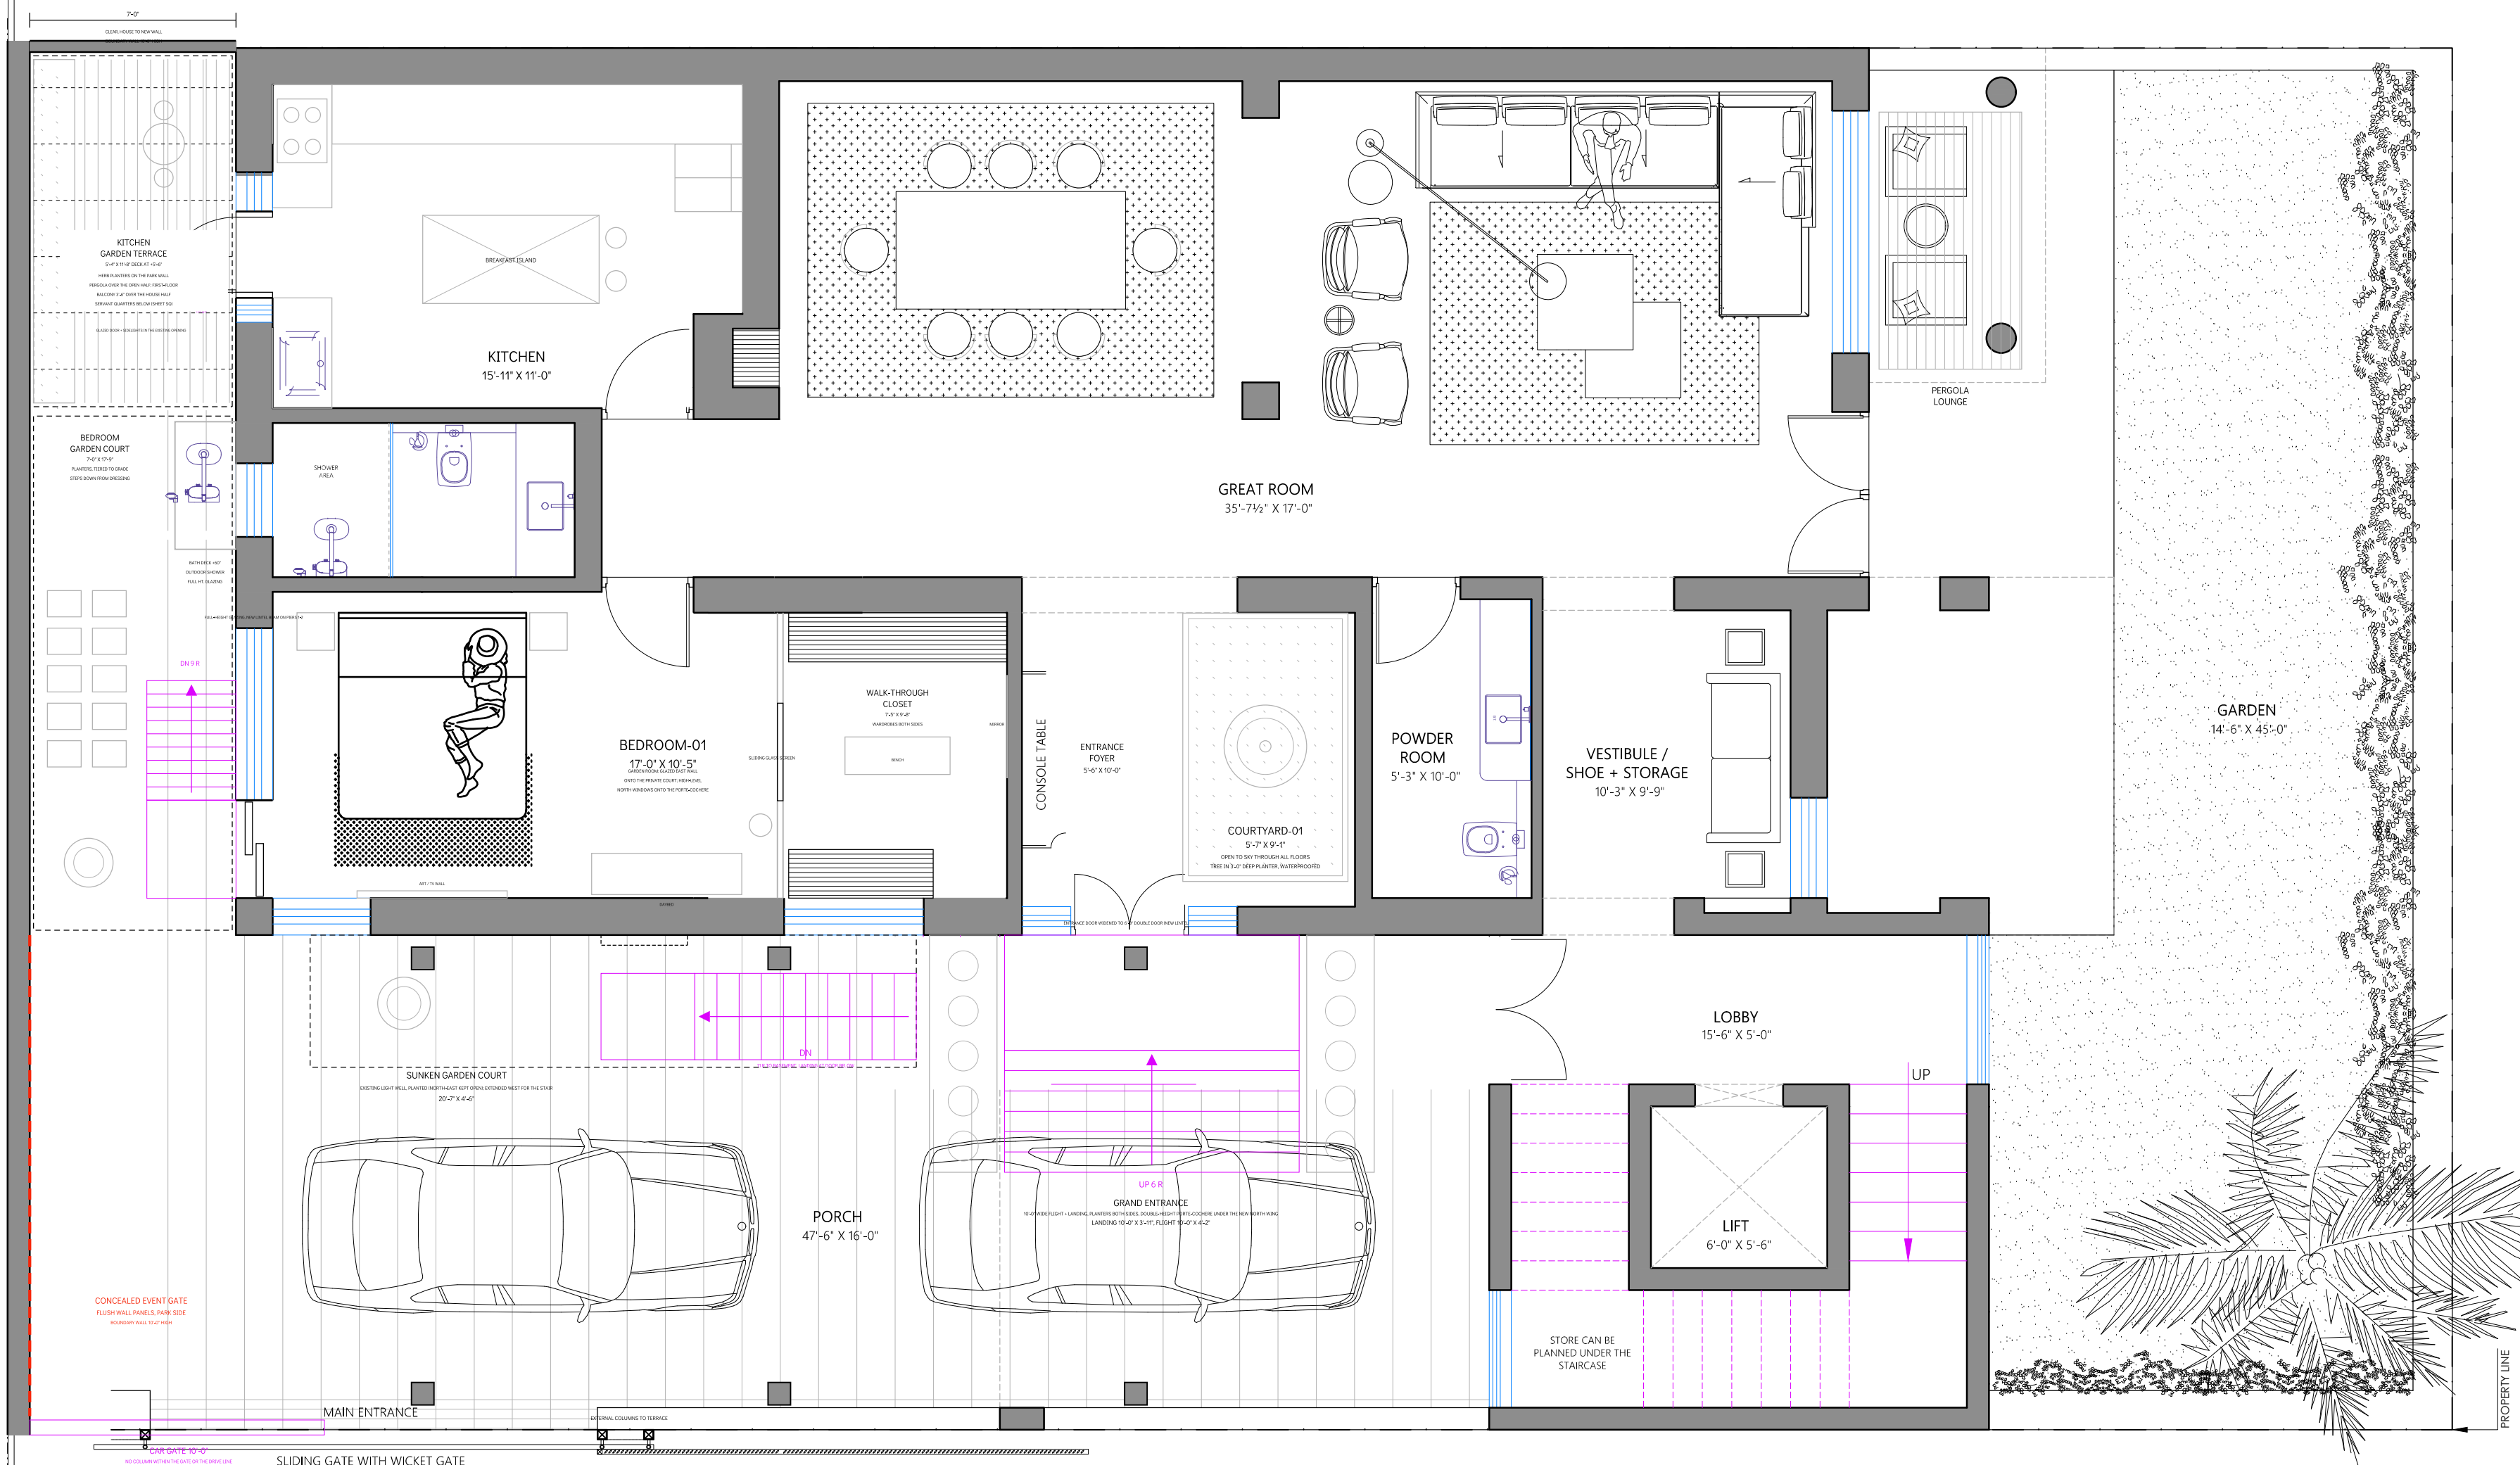

A. EAST SIDE: 7'-0" CLEAR BETWEEN THE HOUSE AND THE NEW STRAIGHT 10'-0" HIGH BOUNDARY WALL (9" THICK), FULL LENGTH. NO OPENINGS TO THE PARK EXCEPT THE EVENT GATE; CAR GATE 10'-0" AT THE EAST END OF THE NORTH BOUNDARY. CONCEALED EVENT GATE IN THE EAST BOUNDARY WALL FROM THE HOUSE CORNER TO THE FRONT BOUNDARY; FLUSH WALL-FINISHED PANELS ON CONCEALED PIVOTS. OPENED ONLY FOR EVENTS.

5 EAST SERVICE SERVANT QUARTERS WITH PLASTER SKIN. SOLI THEIR KITCHEN AT +5-8'5" THE KITCHEN GARDEN ENTRANCE, ONE RISE ABOVE THE KITCHEN FLOOR GRAZED DOOR. THE OLD WINDOW OPENING, BELOW PLASTER SKIN ALONG THE PARK WALL 14'-0" OF WALL ABOVE THE DECK AS GUARD, PENGLA OVER THE OPEN HALL (THE EXISTING 3'-8" FIRST FLOOR BALCONY COVERS THE HOUSE HALL, BUILT DESIGNED FOR TERRACE LOUD). THE KITCHEN IS EAST MORNING LIGHT AND CROSS-VENTILATION, NORTH OF IT THE STAIR IS BEDROOMS PRIVATE GARDEN COURT; WITH DECK AT +6' WITH THE OUTDOOR SHOWER, TERRED PLASTER, STEPS DOWN FROM THE BEDROOM DOORS. THE BEDROOM DOORS ARE NORTH-WEST.


F. ALL ROOM DIMENSIONS ARE CLEAR INTERNAL SIZES TAKEN FROM THE DRAWN WALLS. SHEET ORIENTATION: TOP = SOUTH, BOTTOM = NORTH, LEFT = EAST, RIGHT = WEST

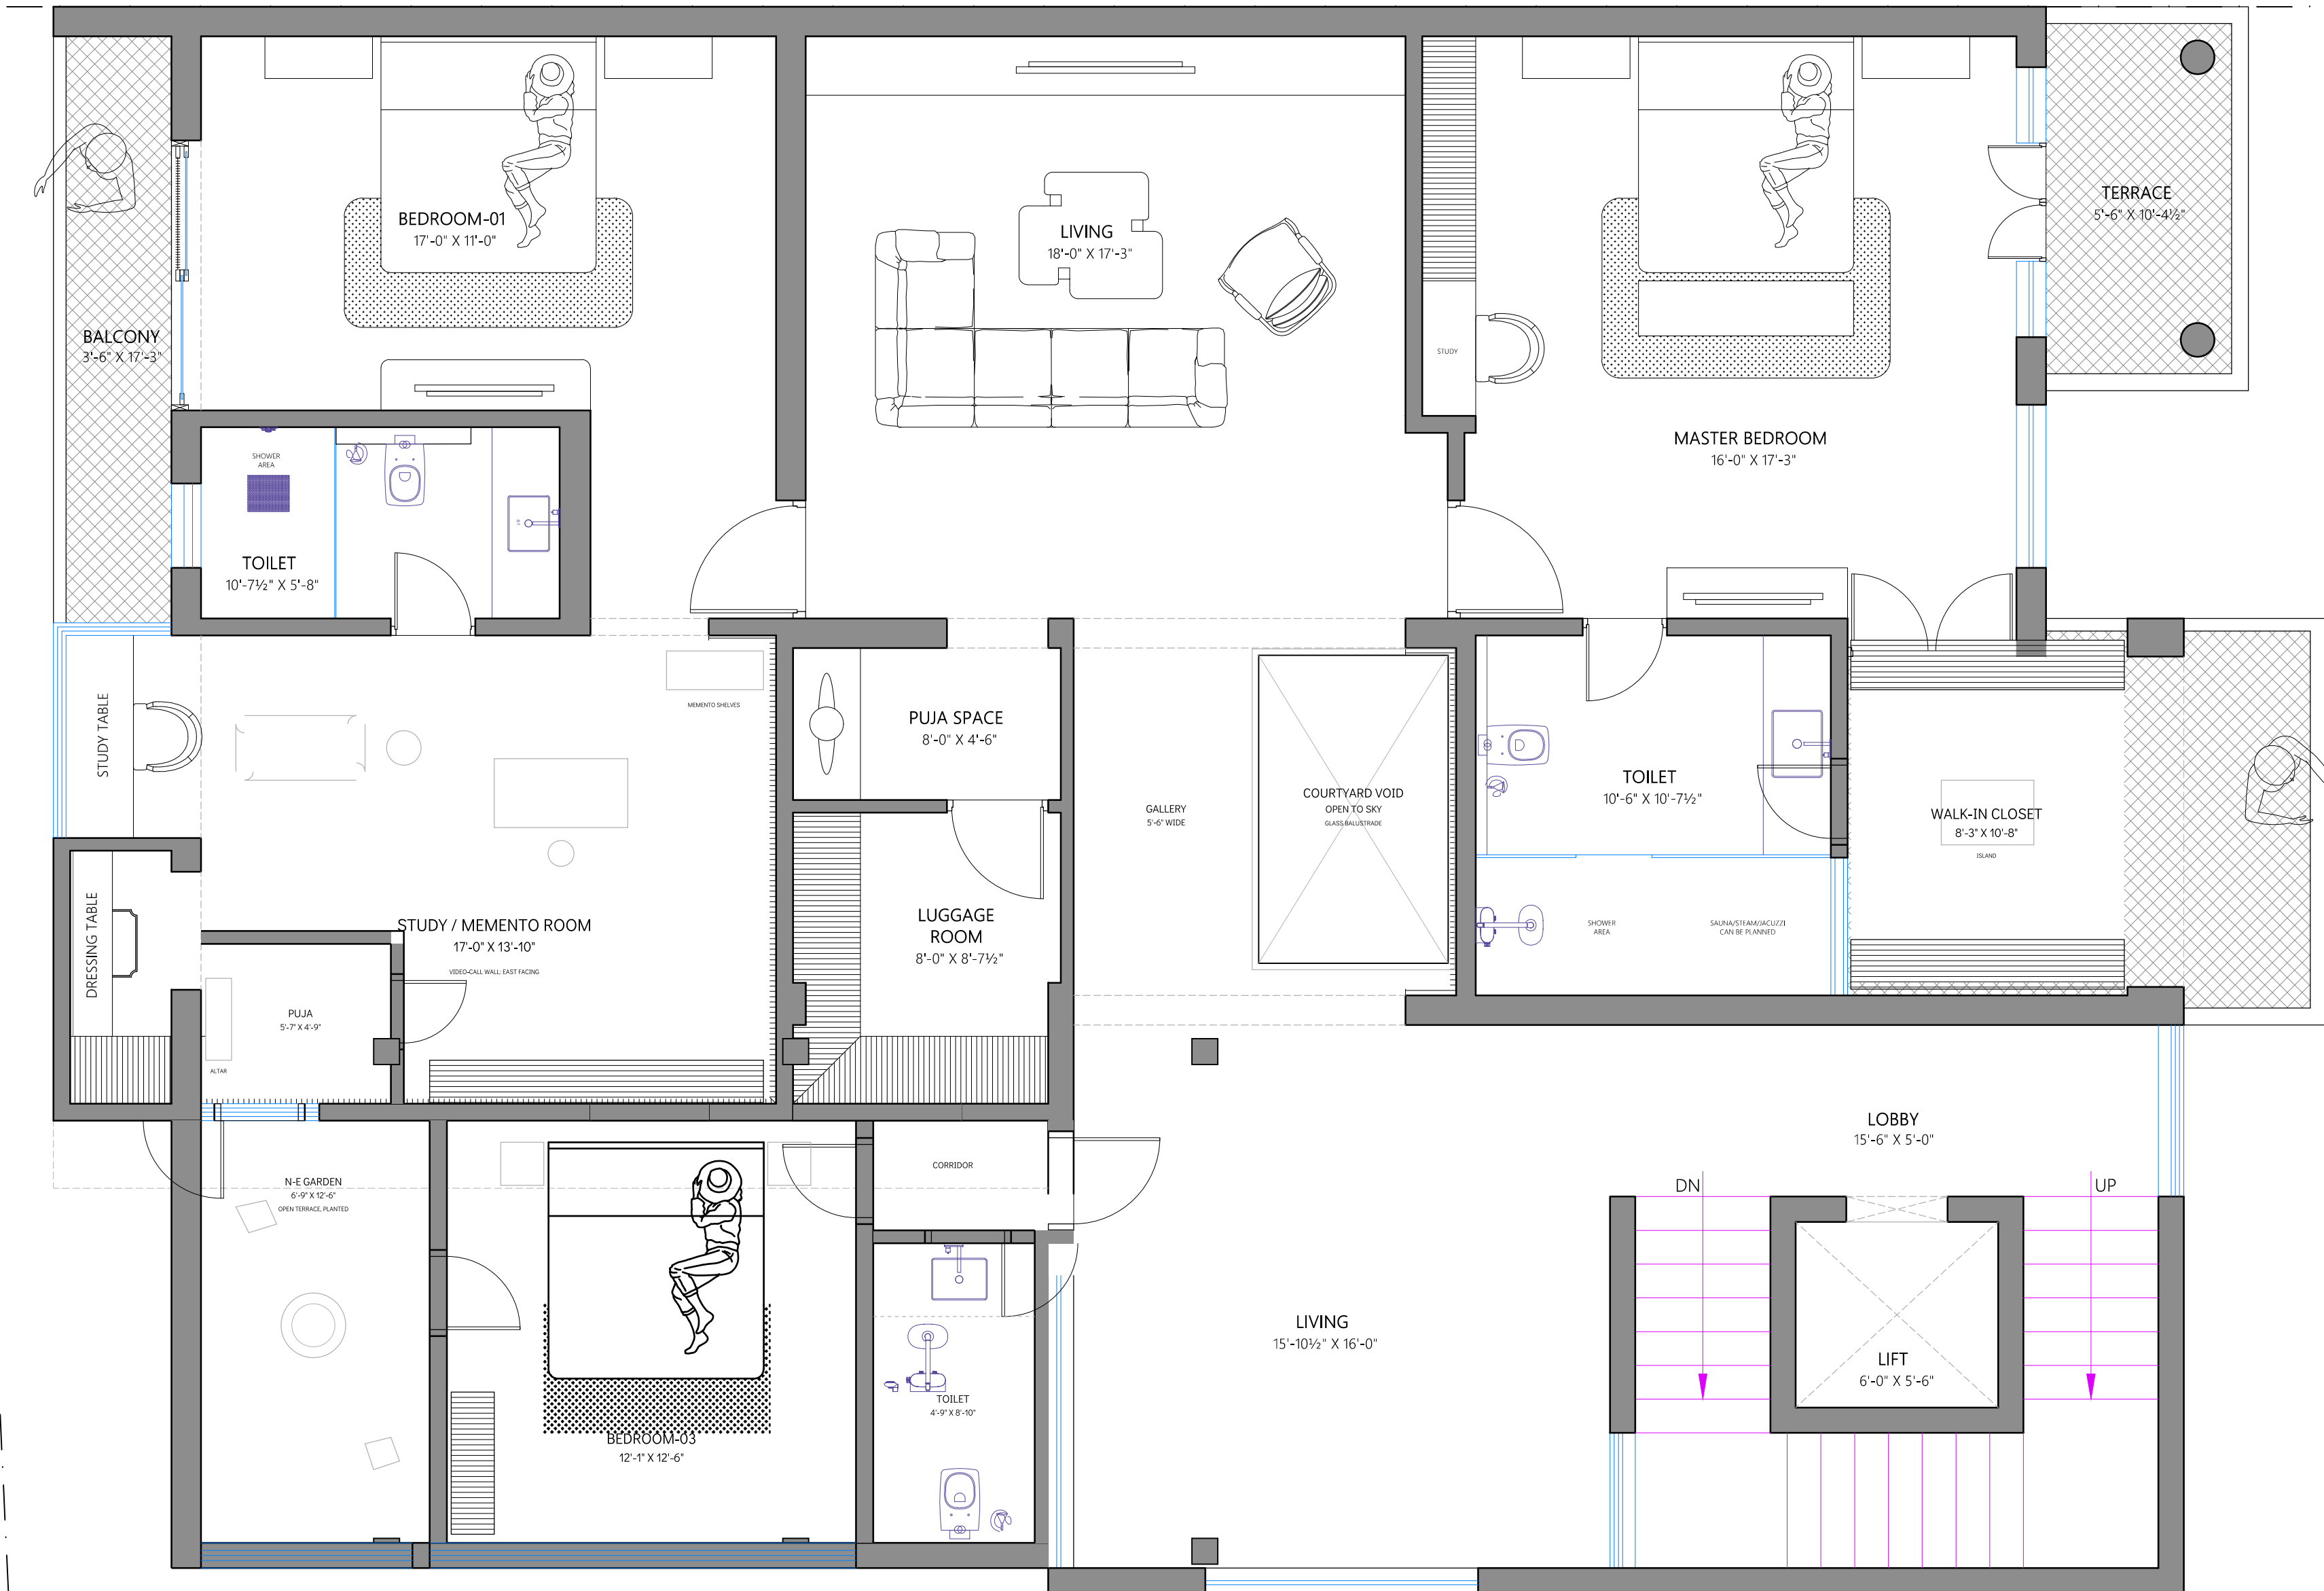

- NOTES:
1. Read this drawing along with relevant architectural, structural or service drawings.
 2. Do not scale; drawing should be read only.
 3. Any discrepancy to be brought to the notice of the architect before commencement of work.
 4. This drawing is a property of Ar. Akash Purohit and shall not be used or reproduced in any manner without the permission of the architects.

PROJECT:
17- CHANDRA PATH

SHEET TITLE:
**FIRST FLOOR -
RENOVATION LAYOUT**

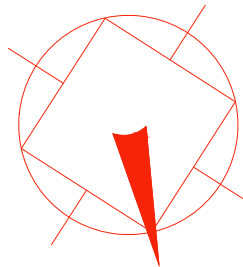

DRAWING NO:
FF-PP-01

DEALT BY:
KAPIL

CHECKED BY:
AKASH

SCALE:
N.T.S.


DATE:
15-09-2026

FILE PATH:

studio sqft

AR. AKASH PUROHIT
ar.akashpurohit@gmail.com
9784784226

NOTES (FIRST FLOOR, R3):
1. THE BLOCK OVER THE PORCH IS REBUILT FROM SCRATCH ON RCC COLUMNS FROM FOUNDATION TO TERRACE (THREE ON THE PORCH LINE, THREE AT THE BACK AGAINST THE NORTH WALL, NONE WITHIN THE 10'-0" CAR GATE OR THE DRIVE LINE), INDEPENDENT OF THE STONE WALLS; TO STRUCTURAL DESIGN.
2. FORMER WEST TERRACE ENCLOSED AS MASTER WALK-IN CLOSET (LIGHT PARTITIONS ON EXISTING SLAB); 3. NORTH-EAST ROOM RE-PURPOSED AS STUDY WITH PUJA IN ITS NORTH-EAST CORNER.
4. COURTYARD VOID WITHIN THE EXISTING STAIRWELL SHAFT; GLASS BALUSTRADE; 5. ROOM DIMENSIONS ARE CLEAR INTERNAL SIZES FROM THE DRAWN WALLS.

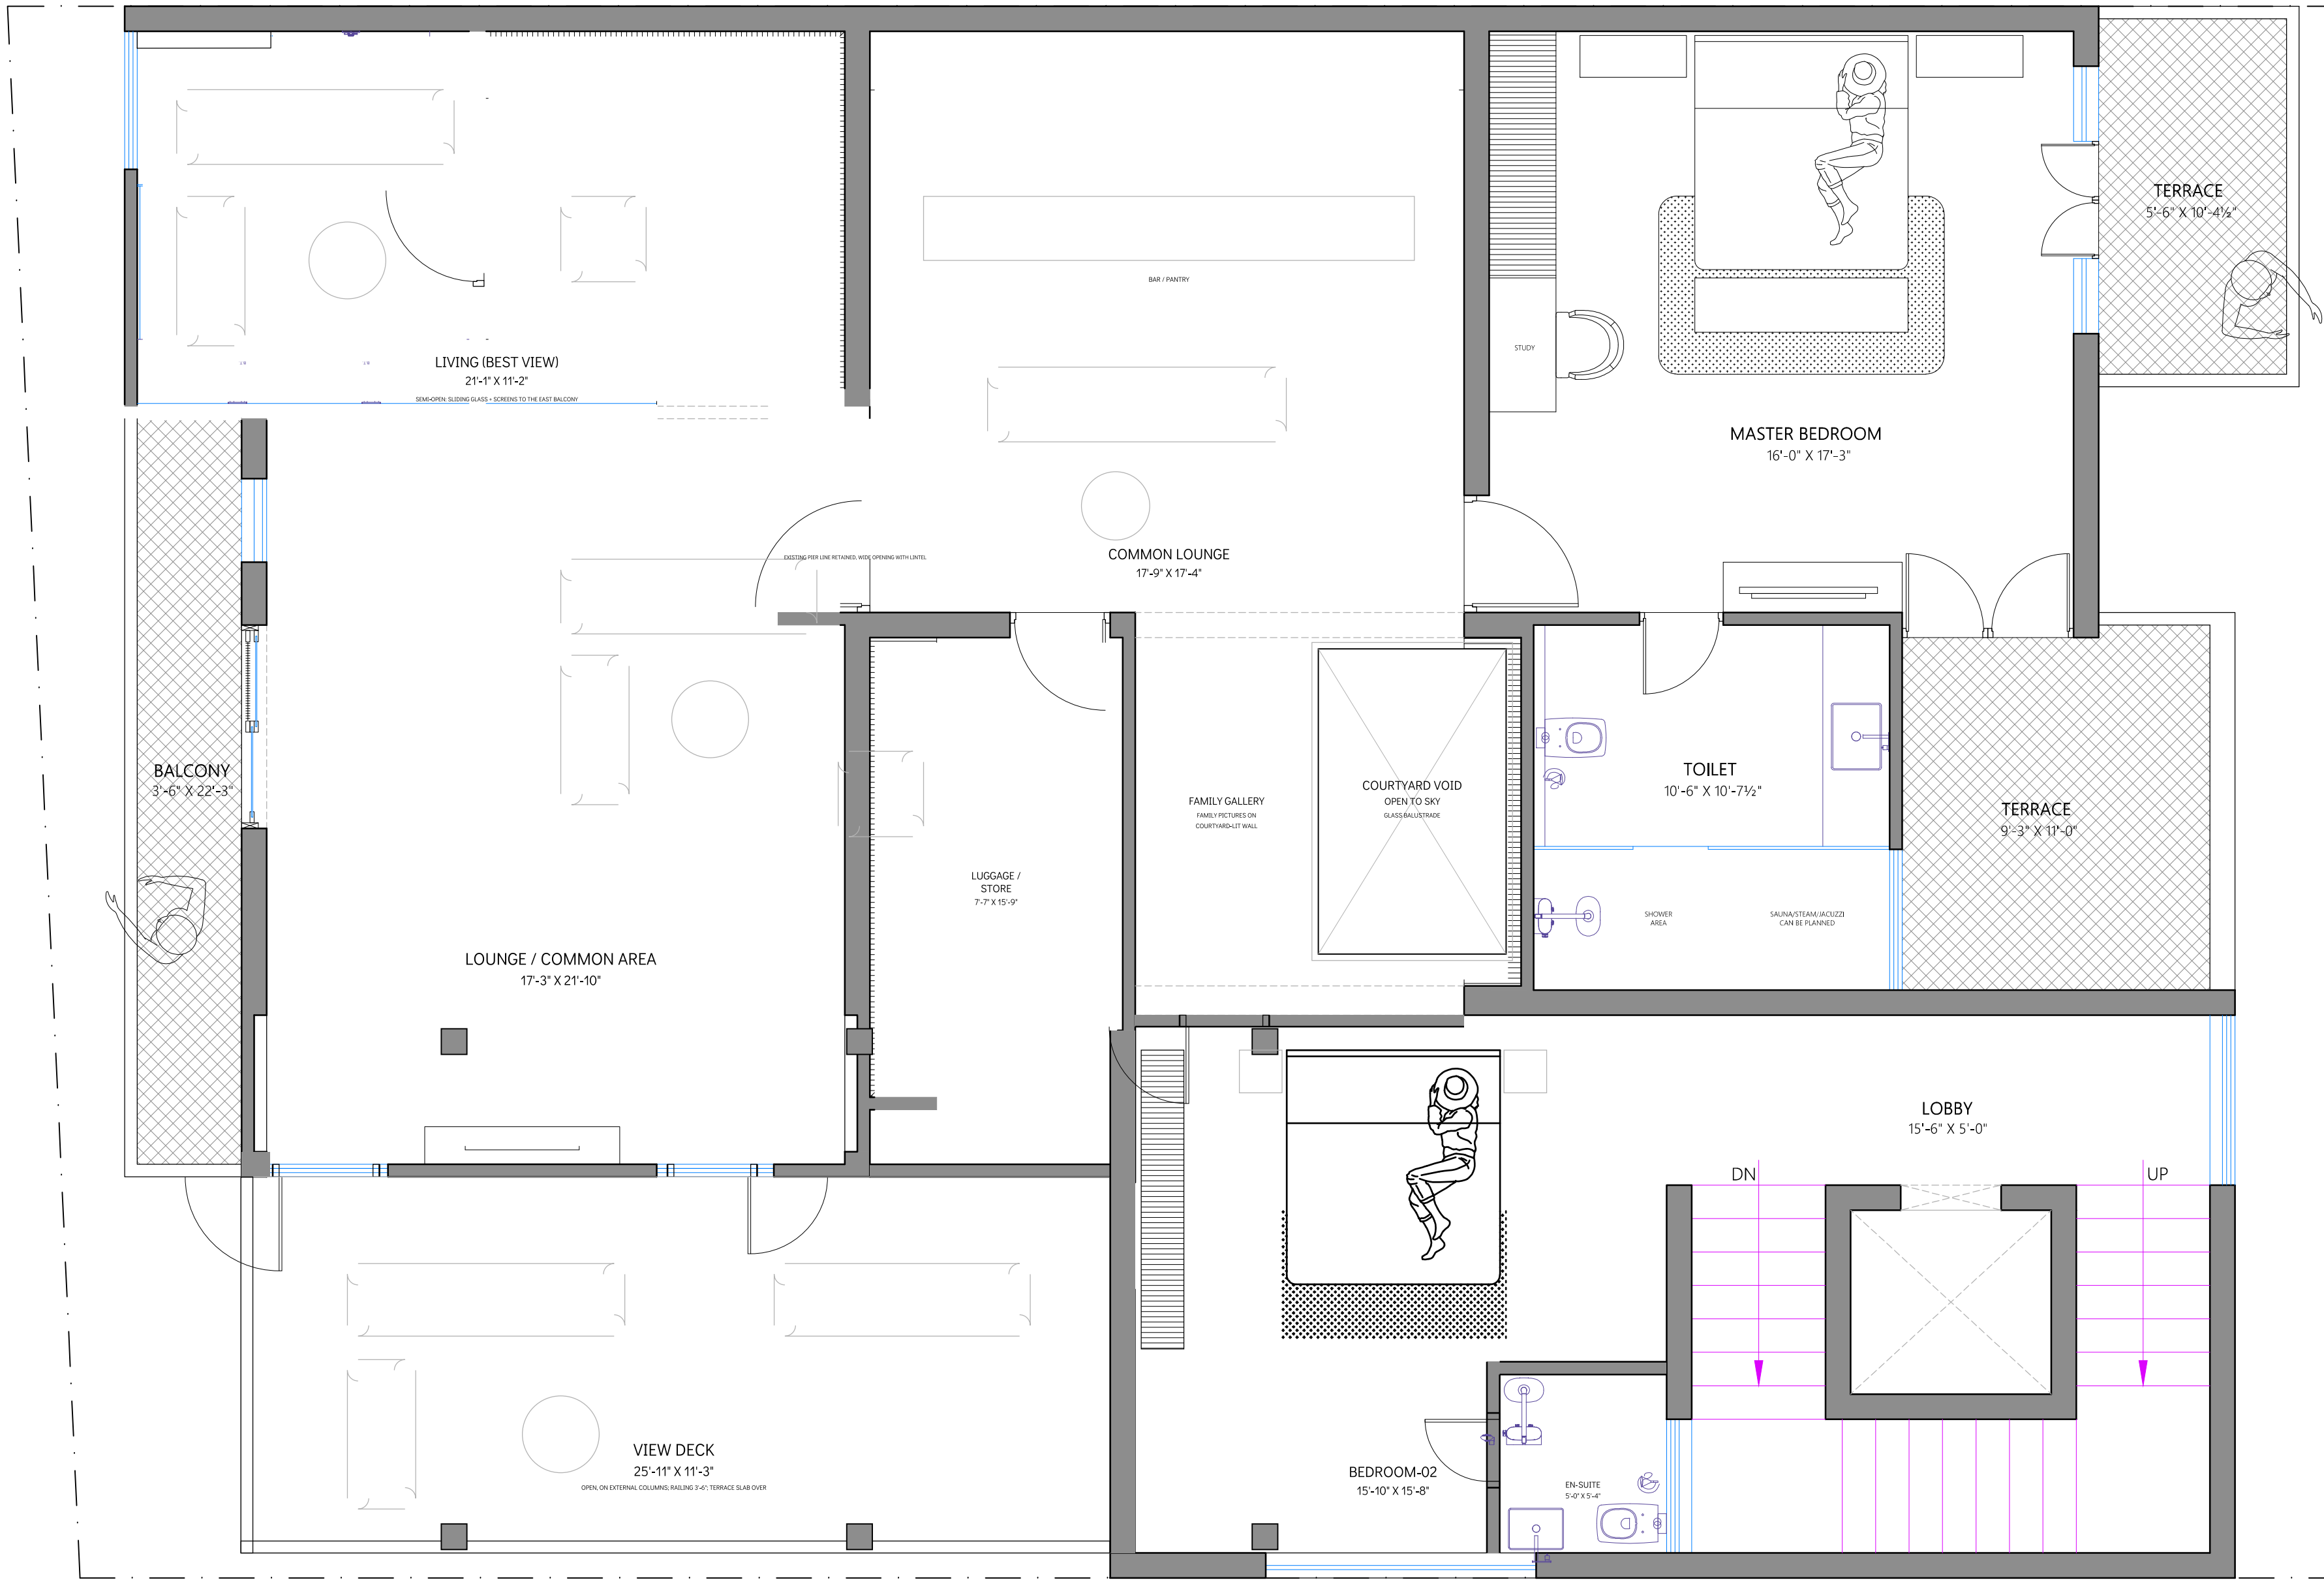


NOTES (SECOND FLOOR, R3):
1. SOUTH-EAST TOILET, WALK-IN CLOSET AND BEDROOM-02 REMOVED; THE SOUTH-EAST CORNER WITH THE BEST VIEW BECOMES THE LIVING ROOM, THE REST A COMMON LOUNGE. FORMER NORTH WINDOWS BECOME DOORS TO THE GARDEN AND BEDROOM-02, OR ARE INFILLED.
2. BEDROOM-02 WITH EN-SUITE IN THE FORMER LIVING OVER THE PORCH (NORTH-WEST); THE NEW EAST WING AT THIS LEVEL IS AN OPEN VIEW DECK ON EXTERNAL COLUMNS, NO WALLS. 3. STRUCTURAL WALL LINES RETAINED AS PIERS; OPENINGS WITH LINTELS.
4. FAMILY GALLERY ALONG THE COURTYARD VOID. 5. ROOM DIMENSIONS ARE CLEAR INTERNAL SIZES FROM THE DRAWN WALLS.

- NOTES:
1. Read this drawing along with relevant architectural, structural or service drawings.
 2. Do not scale; drawing should be read only.
 3. Any discrepancy to be brought to the notice of the architect before commencement of work.
 4. This drawing is a property of Ar. Akash Purohit and shall not be used or reproduced in any manner without the permission of the architects.

PROJECT:
17- CHANDRA PATH

SHEET TITLE:
SECOND FLOOR- LAYOUT

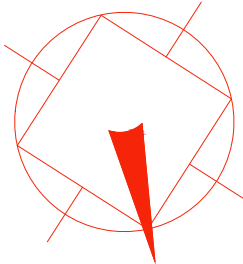

DRAWING NO:
SF-PP-01


DEALT BY: KAPIL	CHECKED BY: AKASH
--------------------	----------------------

SCALE: N.T.S.	DATE: 15-09-2026
------------------	---------------------

FILE PATH:

studio sqft

AR. AKASH PUROHIT
ar.akashpurohit@gmail.com
9784784226

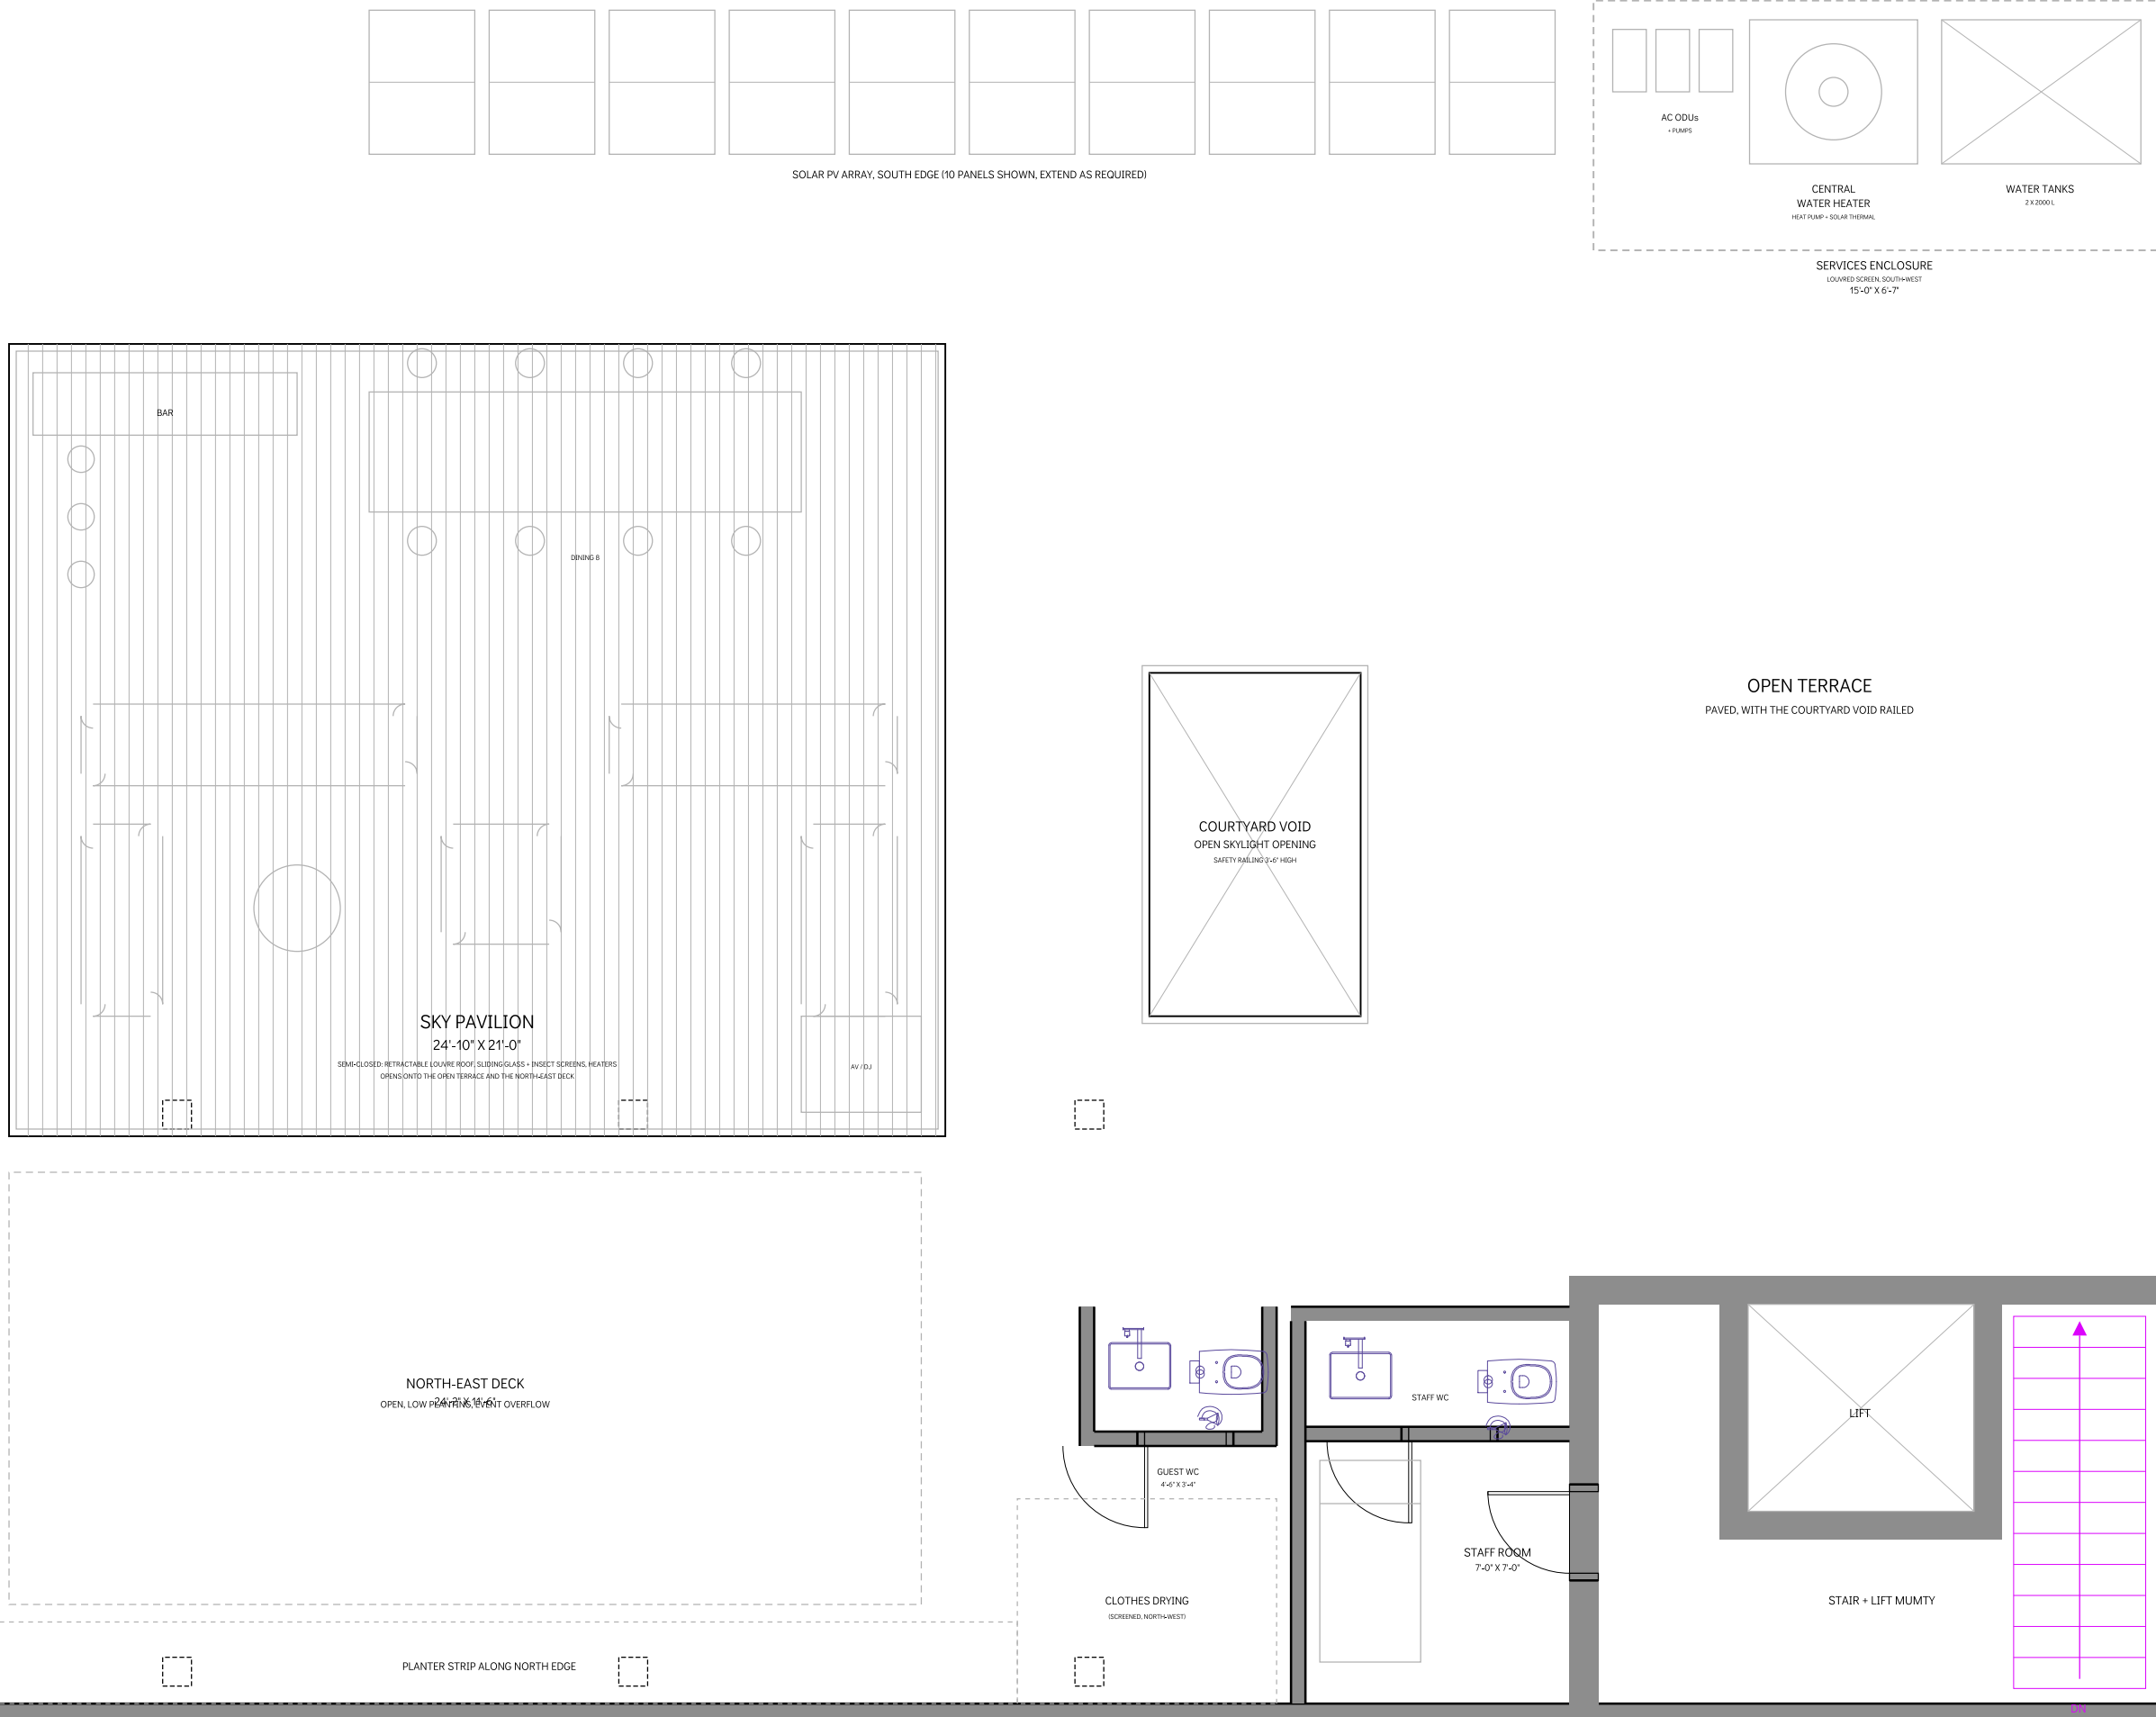

TERRACE FLOOR -
LAYOUT

TF-PP-01

NOTES (TERRACE, R5):
1. PARAPET 3'-6" HIGH ALL ROUND; COURTYARD VOID RAILED. 2. WATER TANKS, CENTRAL WATER HEATER, AC OUTDOOR UNITS AND PUMPS IN A LOUVRED SERVICES ENCLOSURE IN THE SOUTH-WEST; SOLAR PV ALONG THE SOUTH PARAPET; NORTH-EAST KEPT OPEN AND LOW (VASTU).
3. SKY PAVILION ON THE EAST: STEEL FRAME, RETRACTABLE LOUVRE ROOF, SLIDING GLASS WITH INSECT SCREENS, BAR, DINING AND LOUNGE; POWER AND WATER TO THE BAR. 4. STAFF ROOM, WC, GUEST WC AND SCREENED DRYING YARD BESIDE THE MUMTY (NORTH-WEST).
5. TERRACE SLAB OVER THE NORTH WING CARRIED ON THE EXTERNAL COLUMNS (DASHED); PAVILION AND SERVICES LOADS TO BE CHECKED BY THE STRUCTURAL ENGINEER. 6. WATERPROOFING AND SLOPES TO NORTH-EAST DRAIN POINTS.

EMENT STAIR IN THE