


EXISTING PLANT ROOM AREA ON THE EAST SIDE, KITCHEN ON WEST
KEEPS ITS OWN ENTRY FROM THE GROUND

VASTU GRID 9 X 9 PADA (ASSESSMENT OVERLAY ONLY)

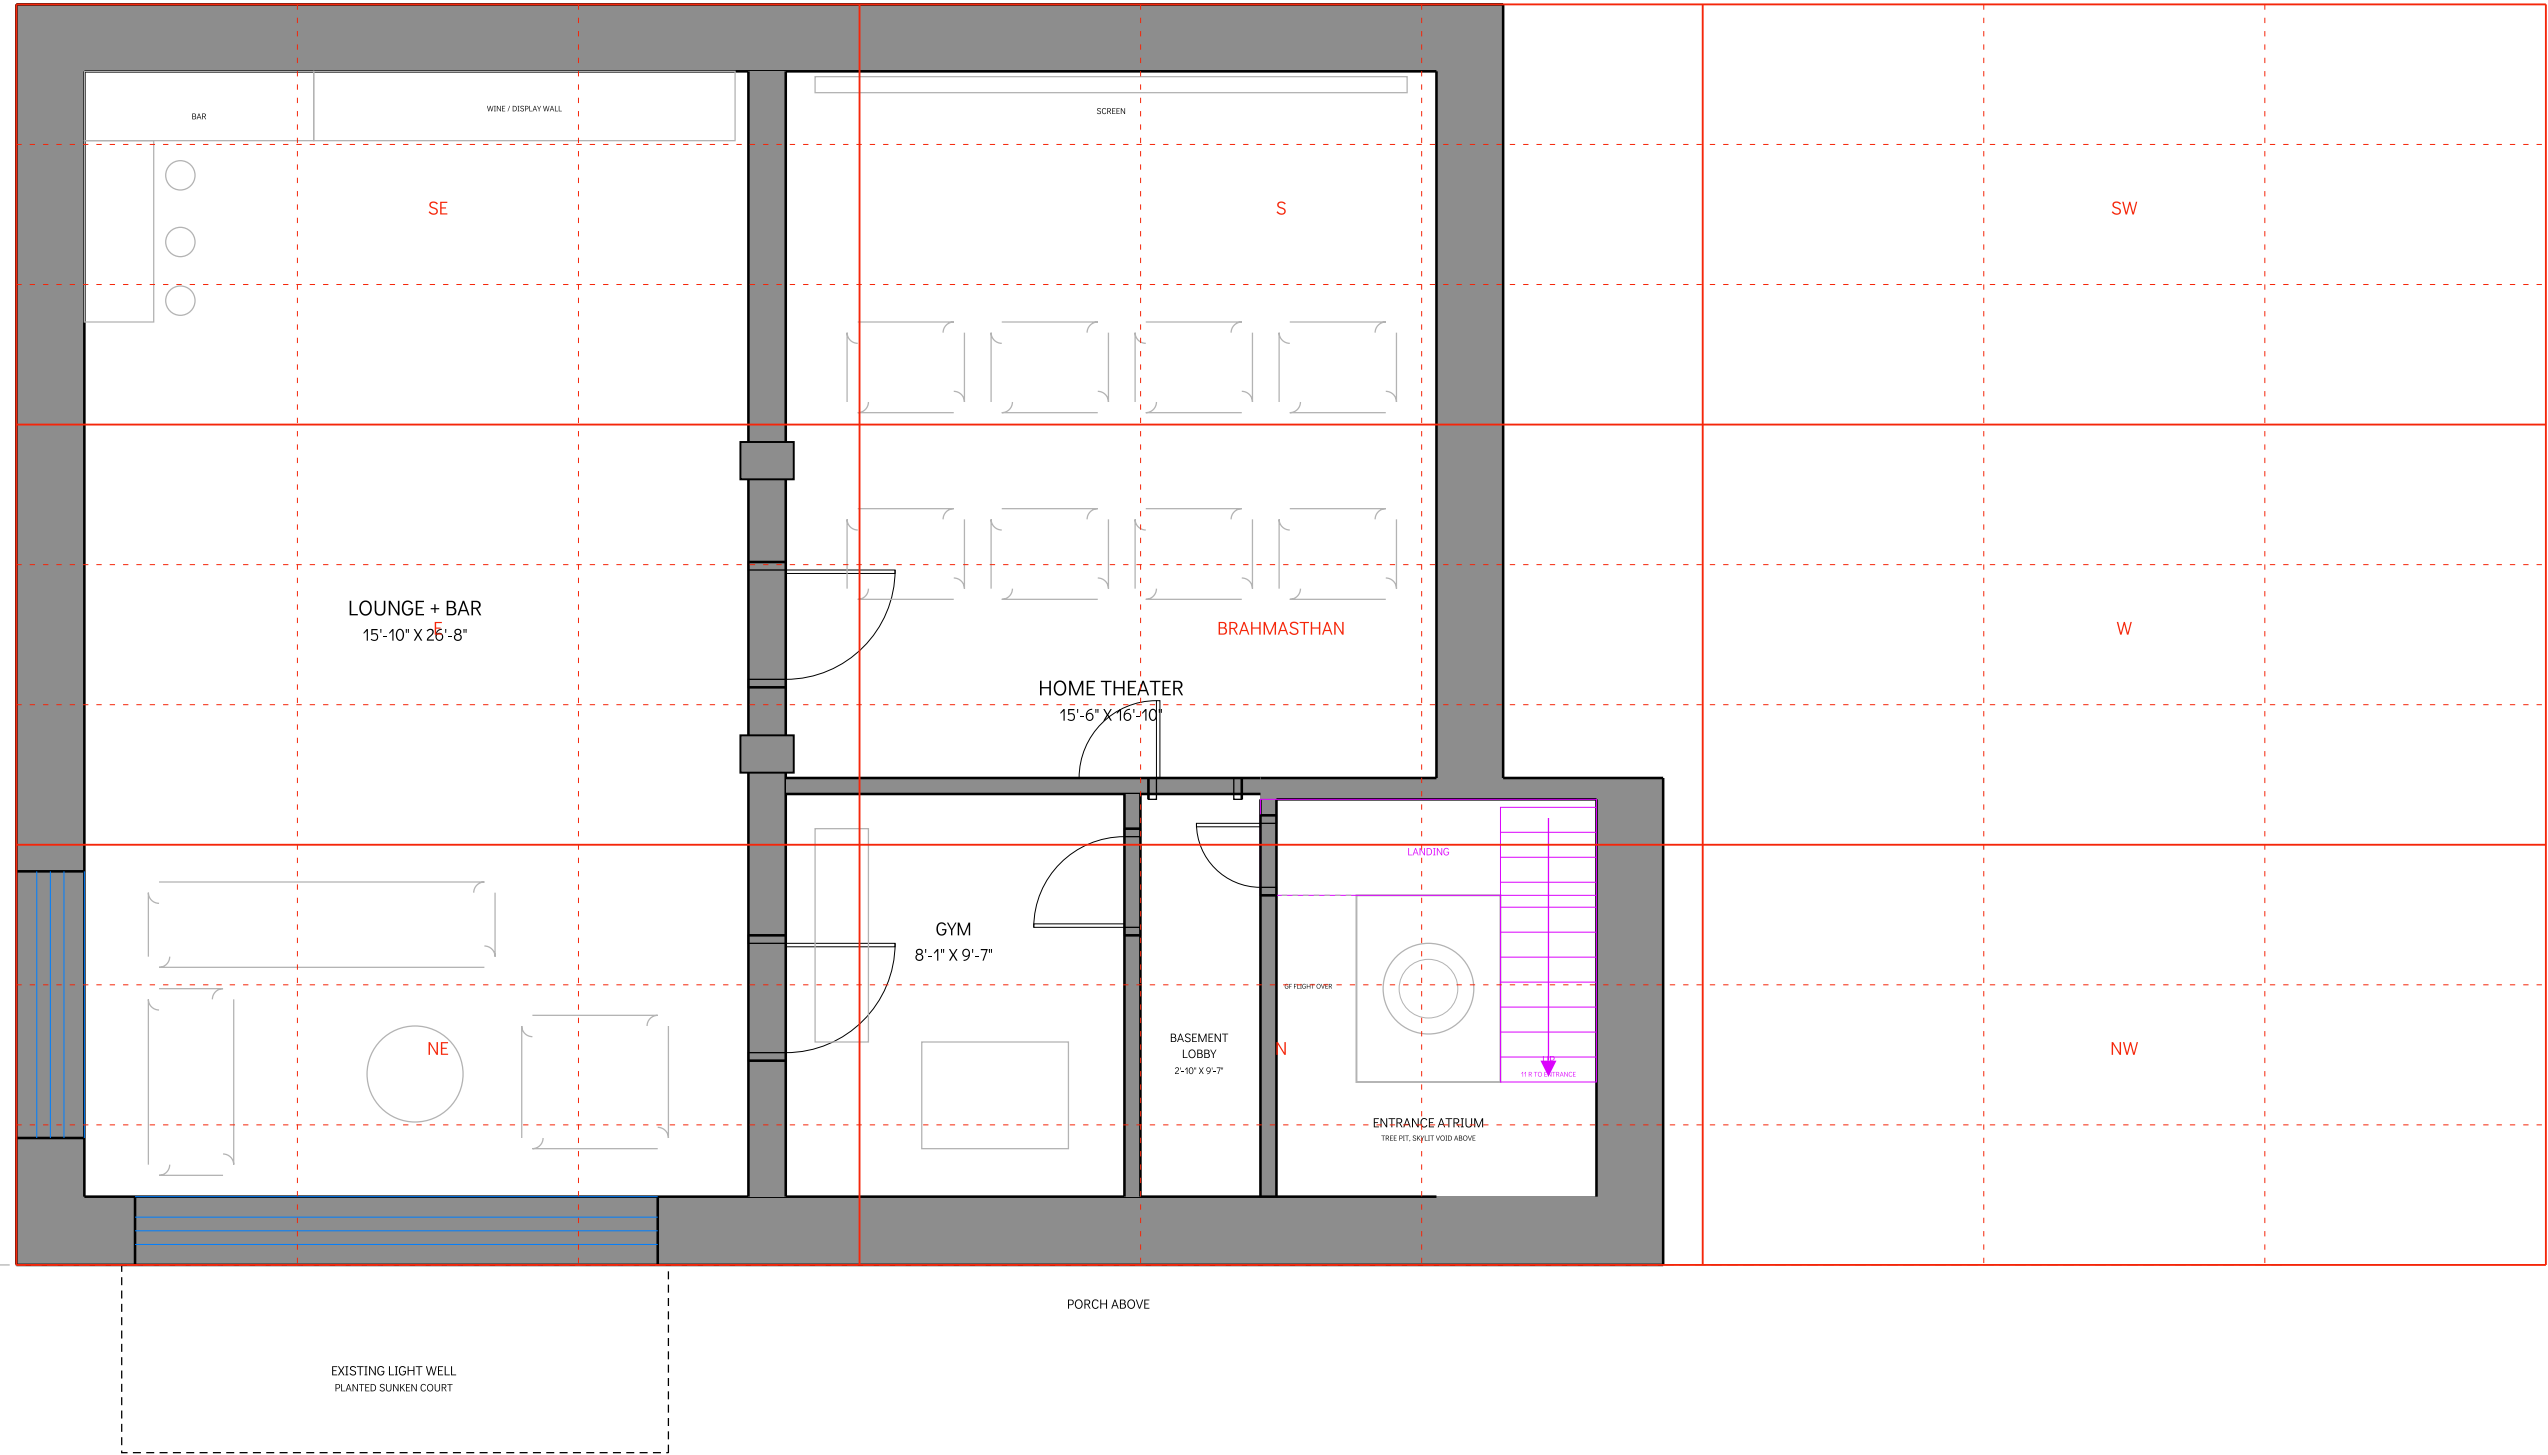

- NOTES (BASEMENT):
- Existing stairwell re-used as the entrance atrium: entrance door at porch level, 6 risers up to the ground floor and 11 down to this level, tree pit between the flights, basement lobby with doors to the gym and theater.
 - No external basement stair; the light well on the north stays a planted sunken court with its window unchanged.
 - Existing servant room area on the east side keeps its own entry, position to be verified on site.
 - Existing ceiling height 8'-6". Existing RCC columns and hidden beam on the centre line are retained; theater partition is non-load-bearing.
 - No new opening in the ground floor slab. Existing basement windows and walls otherwise unchanged.


BASEMENT - RENOVATION LAYOUT

BF-PP-01

1. Read this drawing along with relevant architectural, structural or service drawings.
2. Do not scale; drawing should be read only.
3. Any discrepancy to be brought to the notice of the architect before commencement of work.
4. This drawing is a property of Ar. Akash Purohit and shall not be used or reproduced in any manner without the permission of the architects.

SHEET TITLE:


**GROUND FLOOR -
RENOVATION LAYOUT**

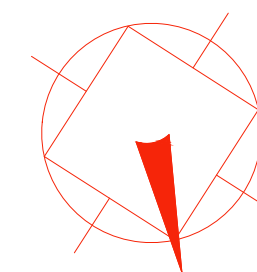

FILE PATH:

studio sqft

AR. AKASH PUROHIT
ar.akashpurohit@gmail.com
9784784226

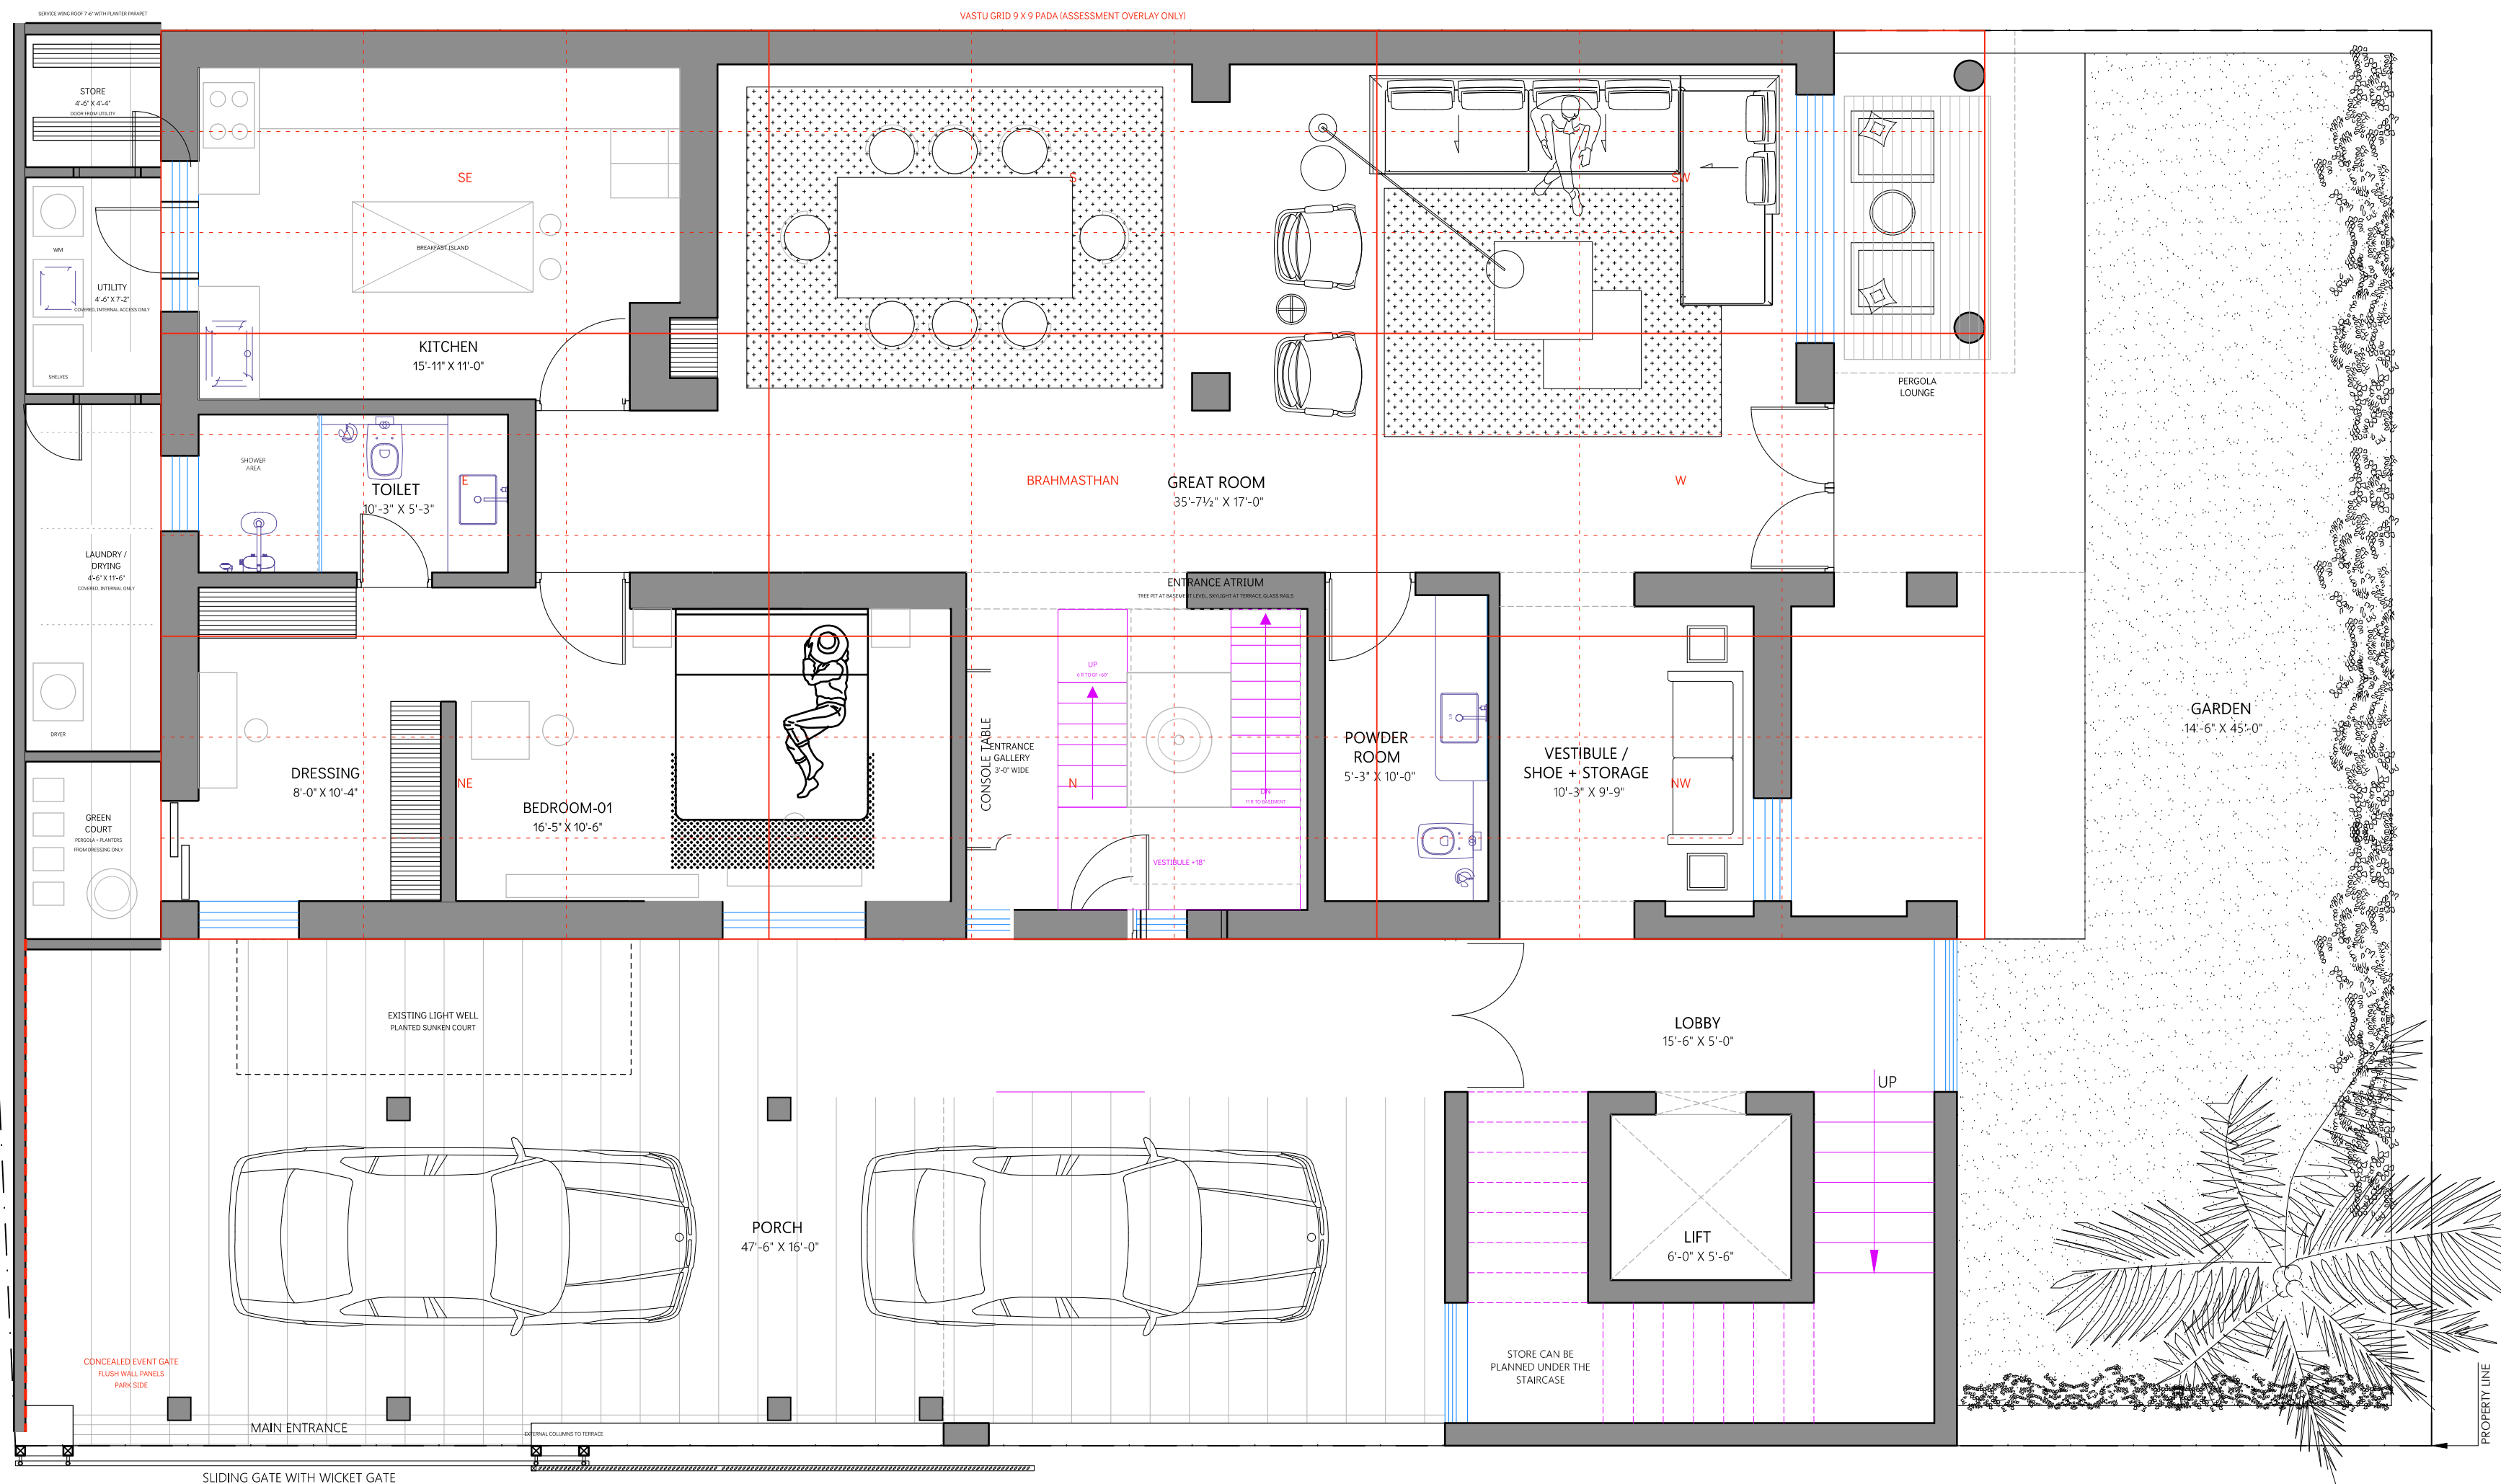

NOTES (REVISION #3):

A. EAST BOUNDARY WALL REBUILT STRAIGHT AND PARALLEL TO THE HOUSE (DRAWN AT THE WIDEST EXISTING OFFSET, TO BE CONFIRMED BY SURVEY). NO OPENINGS TO THE PARK SIDE EXCEPT THE EVENT GATE.

B. CONCEALED EVENT GATE IN THE EAST BOUNDARY WALL FROM THE HOUSE CORNER TO THE FRONT BOUNDARY: FLUSH WALL-FINISHED PANELS ON CONCEALED PIVOTS, OPENED ONLY FOR EVENTS.

C. ENTRANCE ATRIUM IN THE EXISTING STAIRWELL SHAFT: NEW DOOR AT PORCH LEVEL, NEW LINTEL, OLD DOOR OPENING INFILLED, 5 RISERS UP TO THE GROUND FLOOR AND 1 DOWN TO THE BASEMENT INSIDE THE HOUSE, PLANTED PIT BETWEEN THE HOUSE, VOID THROUGH ALL FLOORS UNDER A GLAZED SKYLIGHT; NO NEW SLAB OPENINGS, NO STEPS IN THE PORCH-ENCLOSED SERVICE WING ALONG THE EAST SIDE AT GROUND FLOOR LEVEL, ENTERED ONLY FROM THE KITCHEN: STORE DOOR FROM UTILITY, UTILITY, COVERED LAUNDRY, GREEN COURT FOR THE DRESSING, KITCHEN-UTILITY DOOR CUT BELOW THE EXISTING WINDOW, LINTEL RETAINED.

D. SERVICE WING ROOFED AT 7'-6" WITH A PLANTER PARAPET; BATHROOM EAST WINDOW IN OBTUSE GLASS, VERANDAH REMOVED, PORCH PAVING PATTERN REMOVED, STAFF ROOM ON THE TERRACE (17F-PP-01); EXISTING SERVICE ROOM AREA ON THE EAST SIDE KEEPS ITS OWN ENTRY (VERIFY ON SITE).

F. VASTI (GR10R) IS AN ASSESSMENT OVER ANY OTHER SUEFIT ORIENTATION: TOP = SOUTH, BOTTOM = NORTH, LEFT = EAST, RIGHT = WEST.

- NOTES:
1. Read this drawing along with relevant architectural, structural or service drawings.
 2. Do not scale; drawing should be read only.
 3. Any discrepancy to be brought to the notice of the architect before commencement of work.
 4. This drawing is a property of Ar. Akash Purohit and shall not be used or reproduced in any manner without the permission of the architects.

PROJECT:
17- CHANDRA PATH

SHEET TITLE:
**FIRST FLOOR -
RENOVATION LAYOUT**

DRAWING NO:
FF-PP-01


DEALT BY: KAPIL	CHECKED BY: AKASH
--------------------	----------------------

SCALE: N.T.S.	DATE: 15-09-2026
------------------	---------------------

FILE PATH:


studio sqft

AR. AKASH PUROHIT
ar.akashpurohit@gmail.com
9784784226

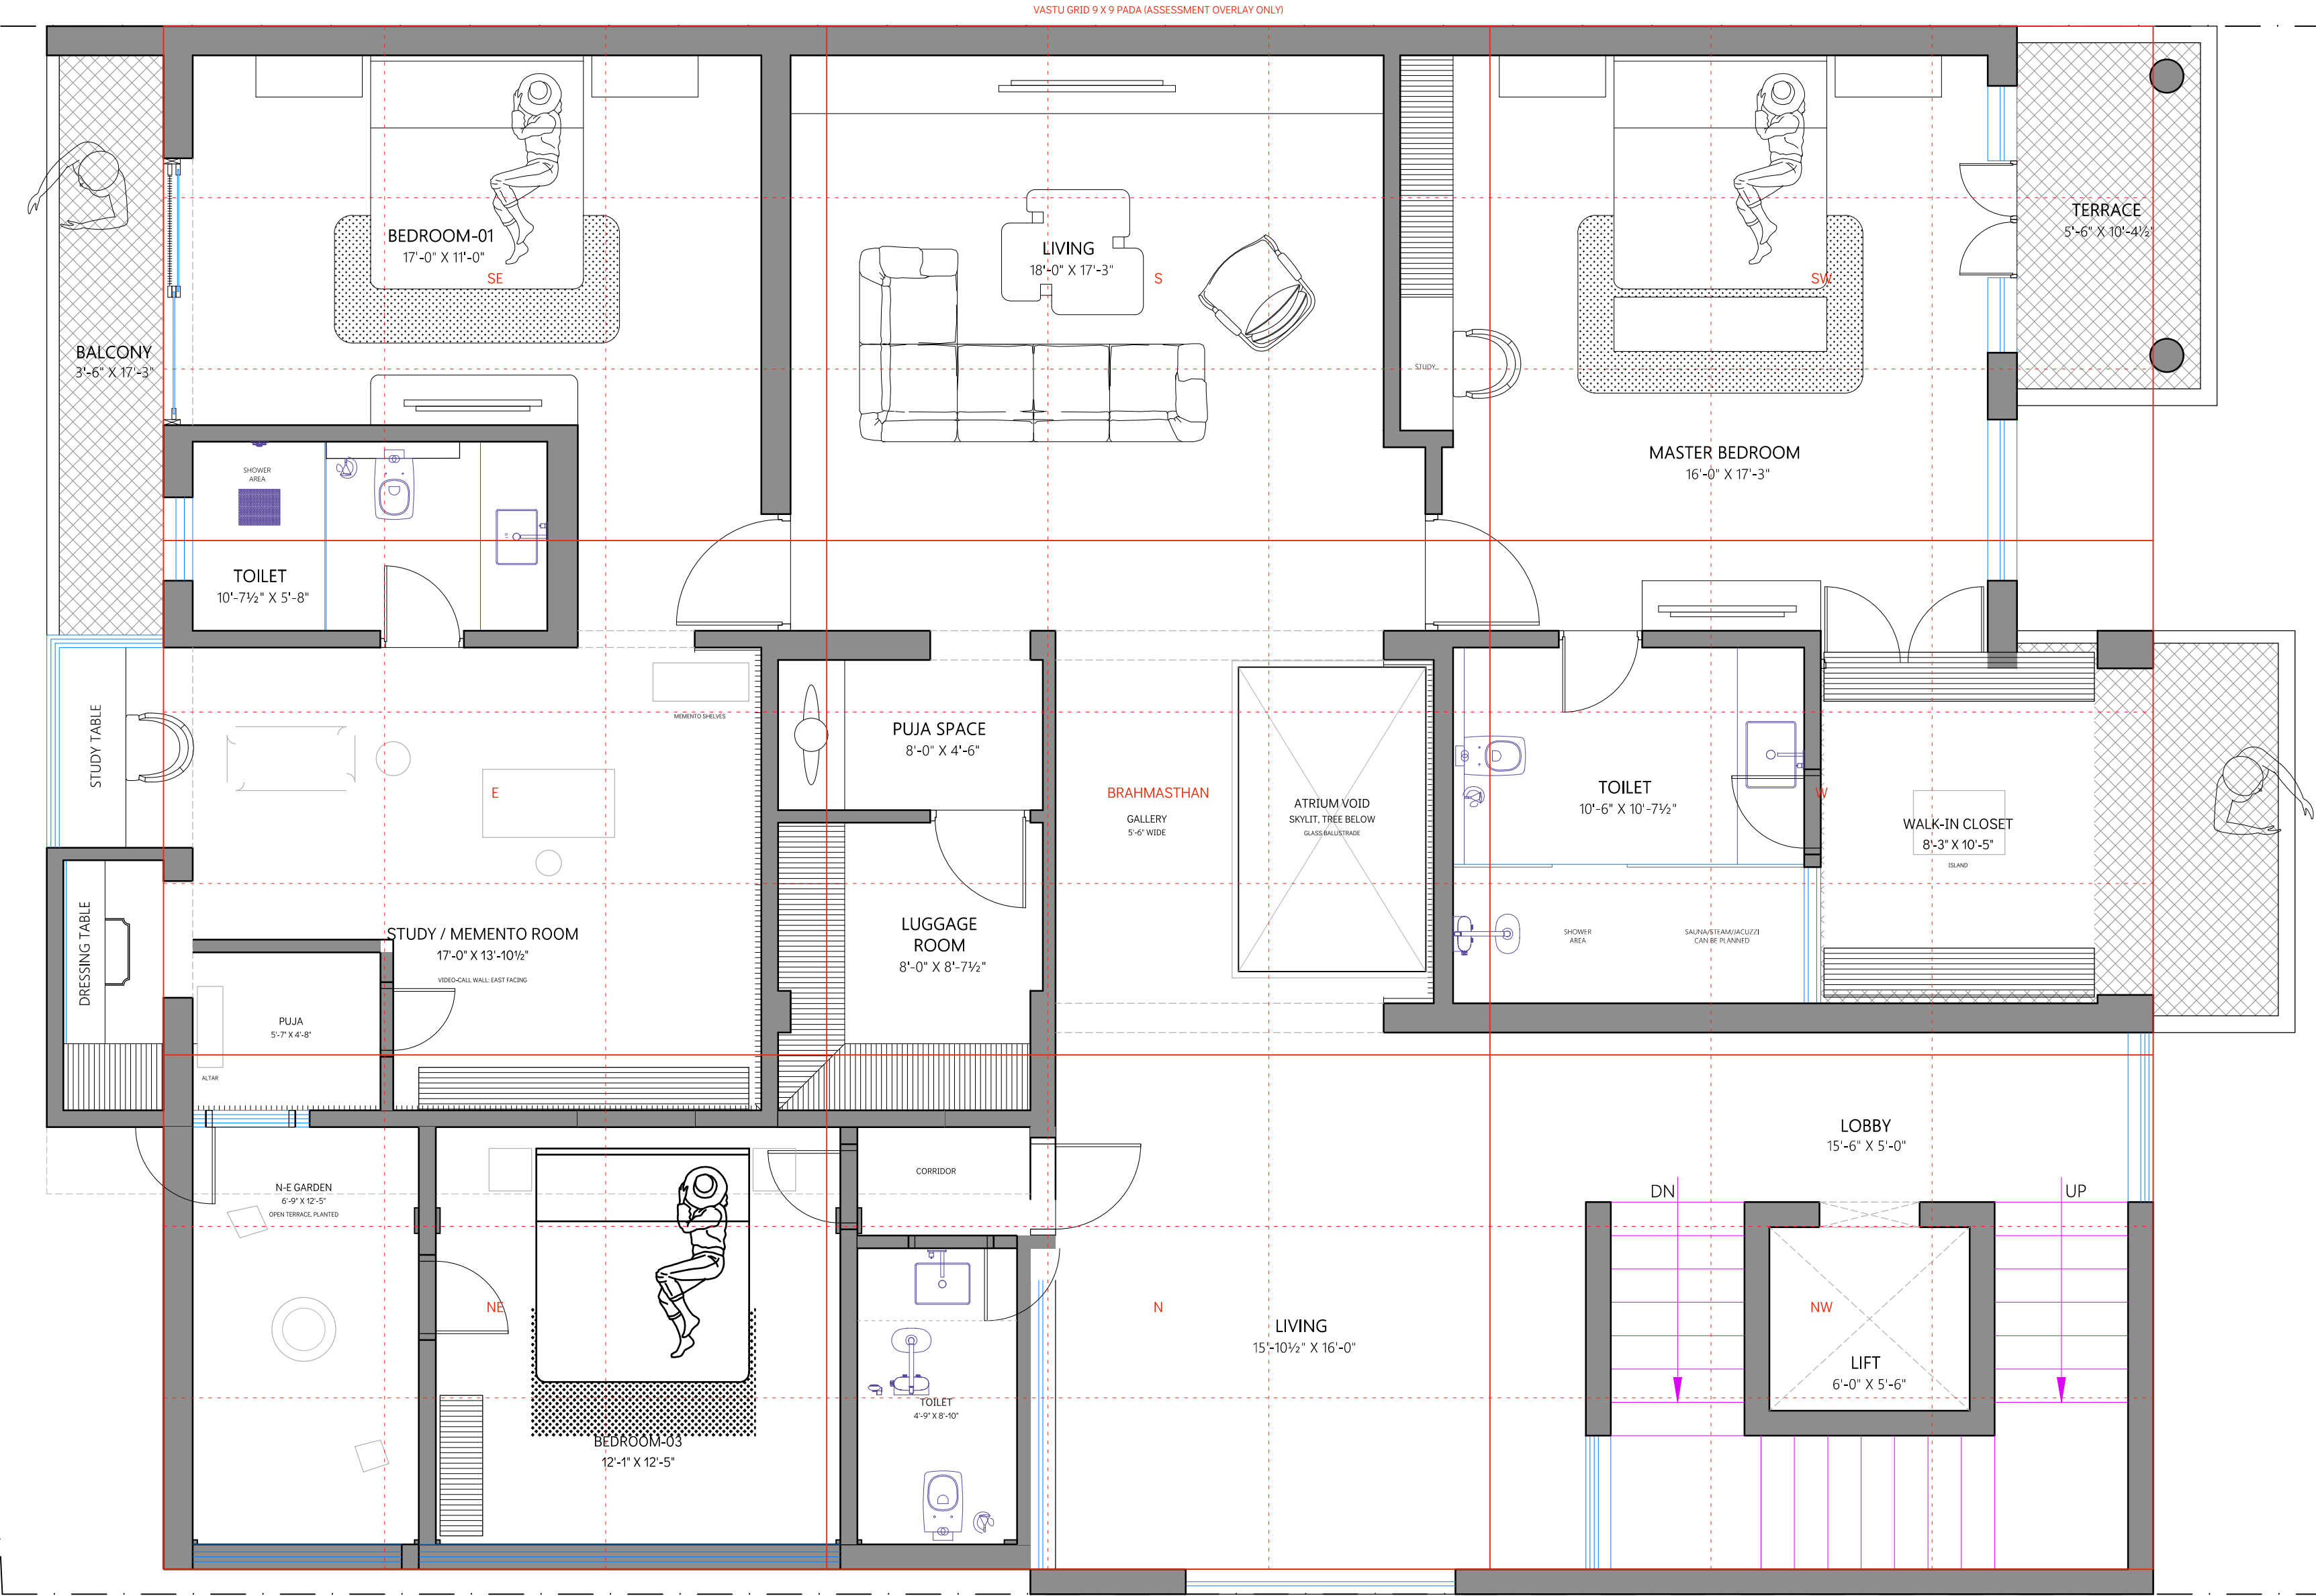

NOTES (FIRST FLOOR, R3):

1. NEW SLABS OVER THE PORCH CARRIED ON EXTERNAL RCC COLUMNS FROM FOUNDATION TO TERRACE (FOUR ON THE PORCH LINE, TWO AT THE BACK AGAINST THE NORTH WALL), INDEPENDENT OF THE STONE WALLS; TO STRUCTURAL DESIGN.
2. FORMER WEST TERRACE ENCLOSED AS MASTER WALK-IN CLOSET (LIGHT PARTITIONS ON EXISTING SLAB). 3. NORTH-EAST ROOM RE-PURPOSED AS STUDY WITH PUJA IN ITS NORTH-EAST CORNER.
4. COURTYARD VOID WITHIN THE EXISTING STAIRWELL SHAFT; GLASS BALUSTRADE. 5. VASTU GRID (RED) IS AN ASSESSMENT OVERLAY ONLY.

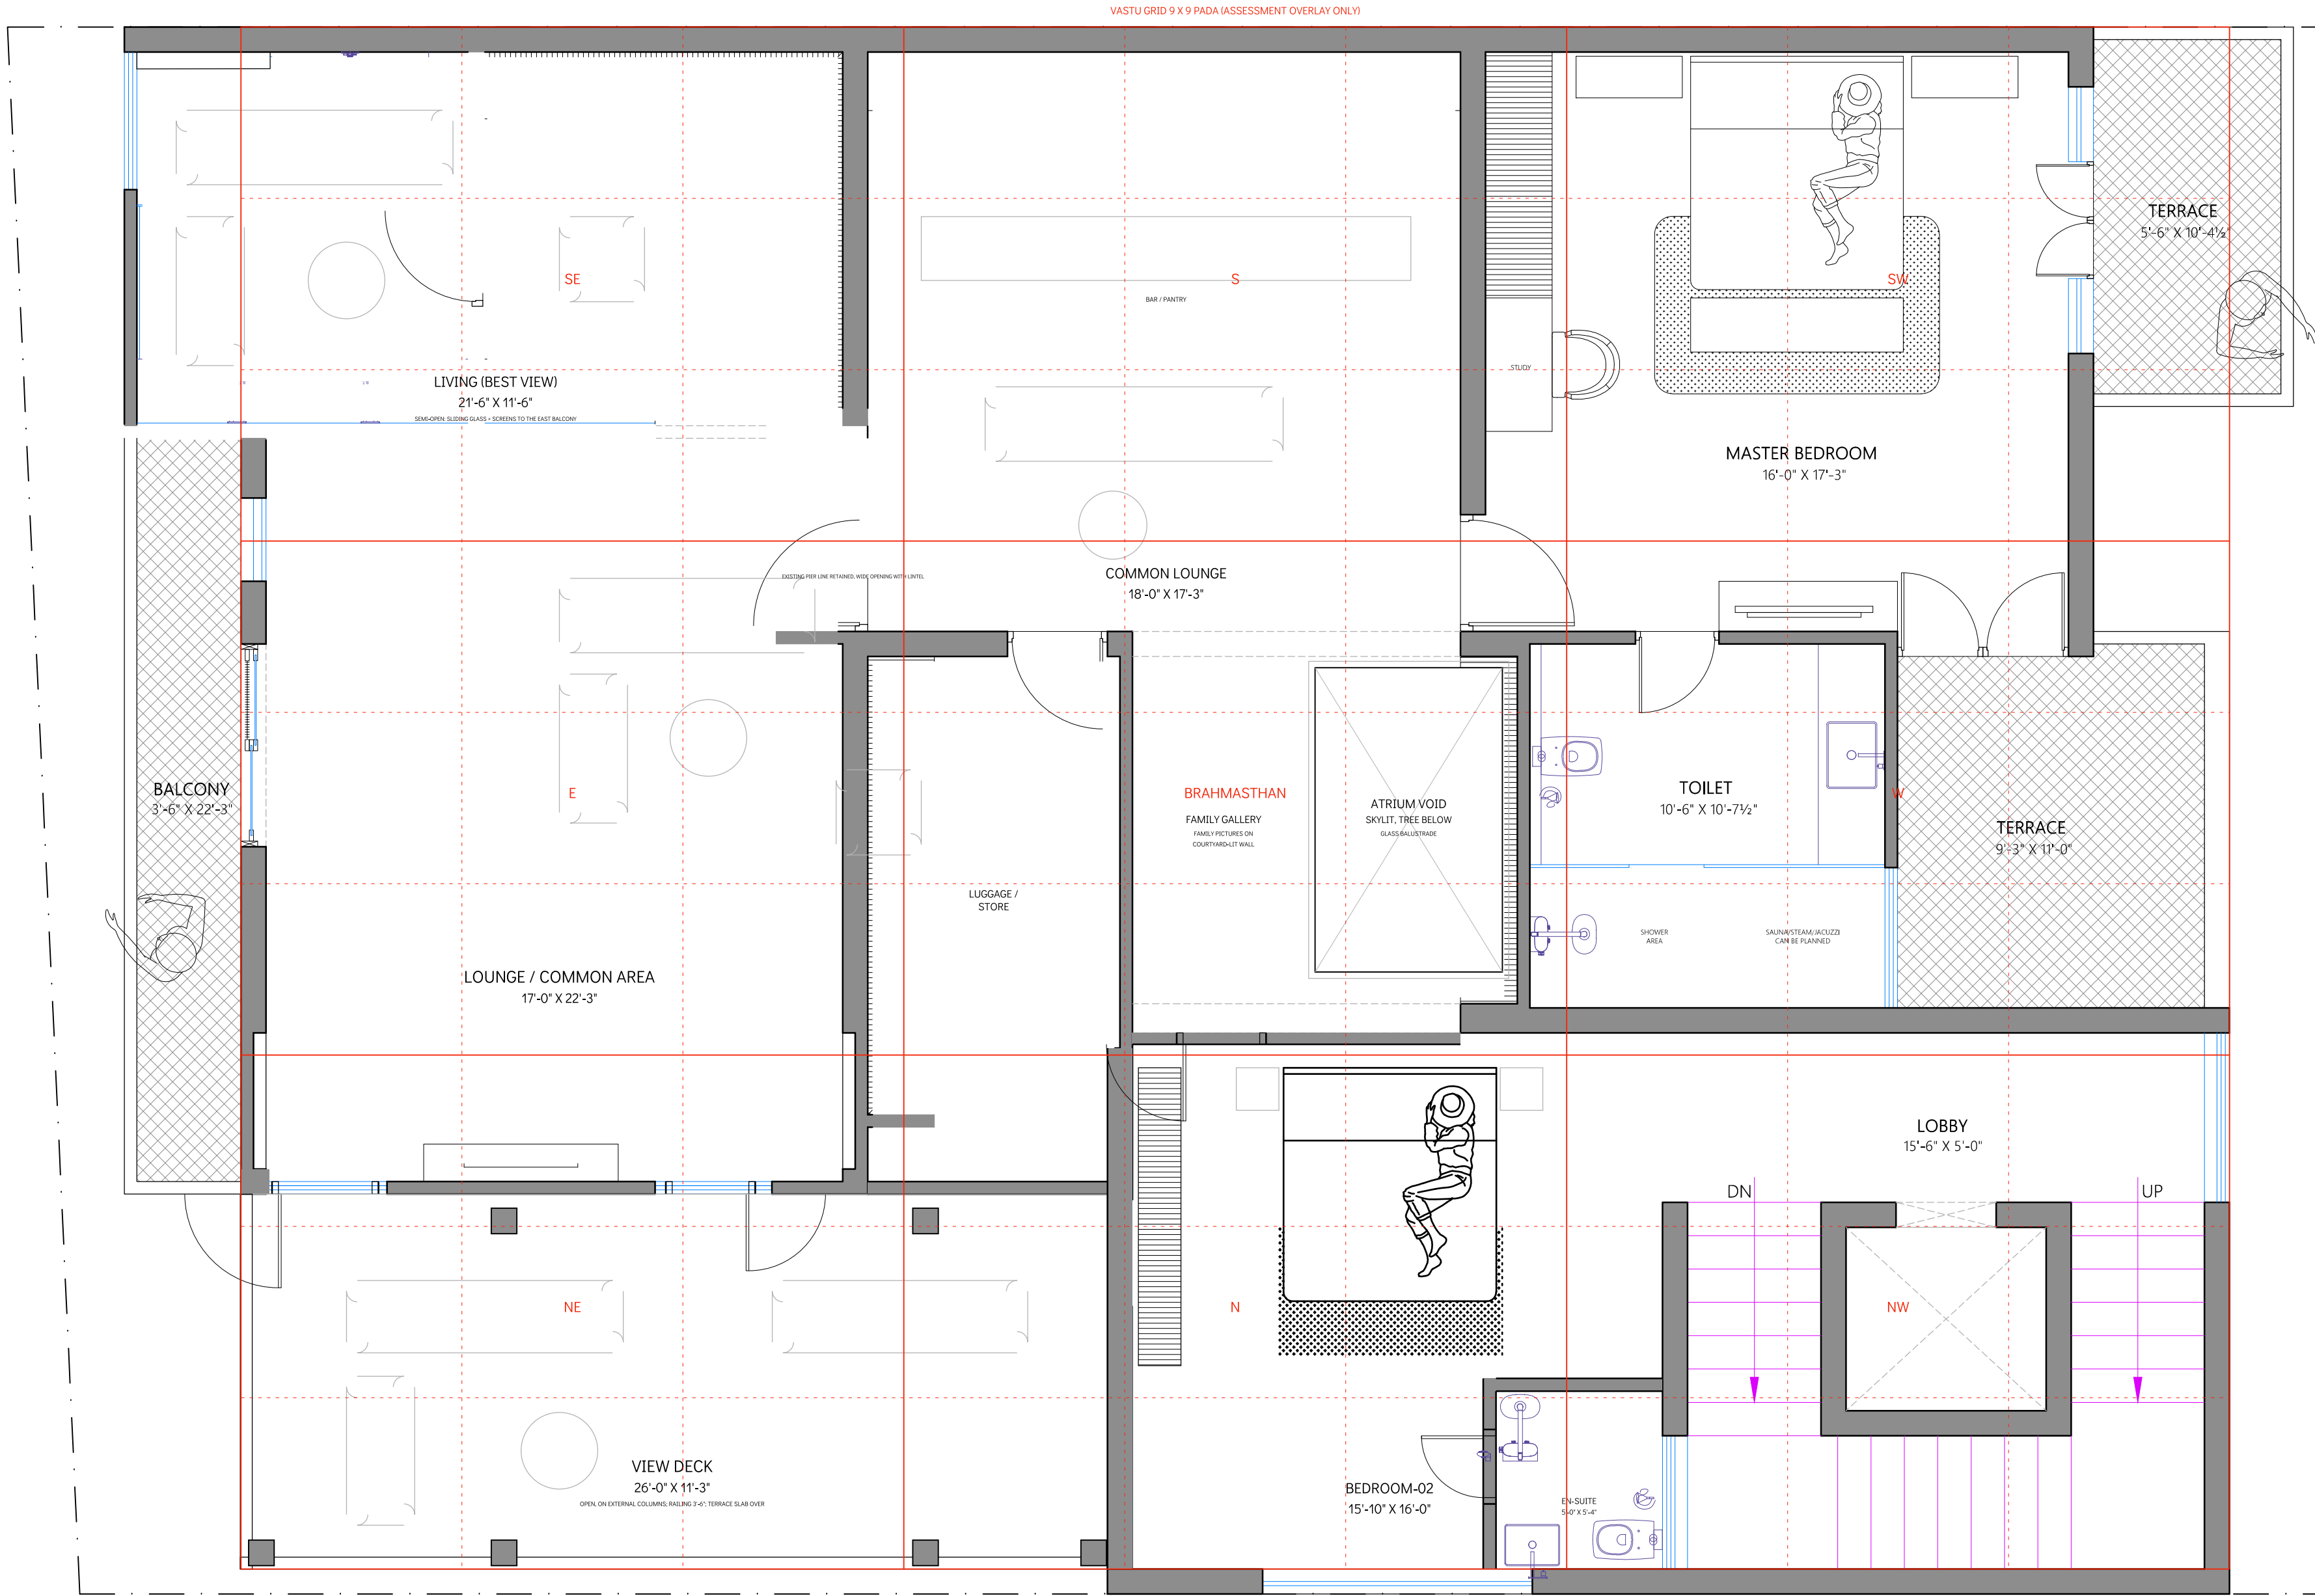

NOTES (SECOND FLOOR, R3):

1. SOUTH-EAST TOILET, WALK-IN CLOSET AND BEDROOM-02 REMOVED; THE SOUTH-EAST CORNER WITH THE BEST VIEW BECOMES THE LIVING ROOM, THE REST A COMMON LOUNGE. FORMER NORTH WINDOWS BECOME DOORS TO THE GARDEN AND BEDROOM-02, OR ARE INFILLED.

2. BEDROOM-02 WITH EN-SUITE IN THE FORMER LIVING OVER THE PORCH (NORTH-WEST); THE NEW EAST WING AT THIS LEVEL IS AN OPEN VIEW DECK ON EXTERNAL COLUMNS, NO WALLS. 3. STRUCTURAL WALL LINES RETAINED AS PIERS; OPENINGS WITH LINTELS.

4. FAMILY GALLERY ALONG THE COURTYARD VOID. 5. VASTU GRID (RED) IS AN ASSESSMENT OVERLAY ONLY.

- NOTES:
1. Read this drawing along with relevant architectural, structural or service drawings.
 2. Do not scale; drawing should be read only.
 3. Any discrepancy to be brought to the notice of the architect before commencement of work.
 4. This drawing is a property of Ar. Akash Purohit and shall not be used or reproduced in any manner without the permission of the architects.

PROJECT:
17- CHANDRA PATH

SHEET TITLE:
SECOND FLOOR- LAYOUT

DRAWING NO:
SF-PP-01

DEALT BY:
KAPIL

CHECKED BY:
AKASH


SCALE:
N.T.S.

DATE:
15-09-2026

FILE PATH:

studio sqft

AR. AKASH PUROHIT
ar.akashpurohit@gmail.com
9784784226

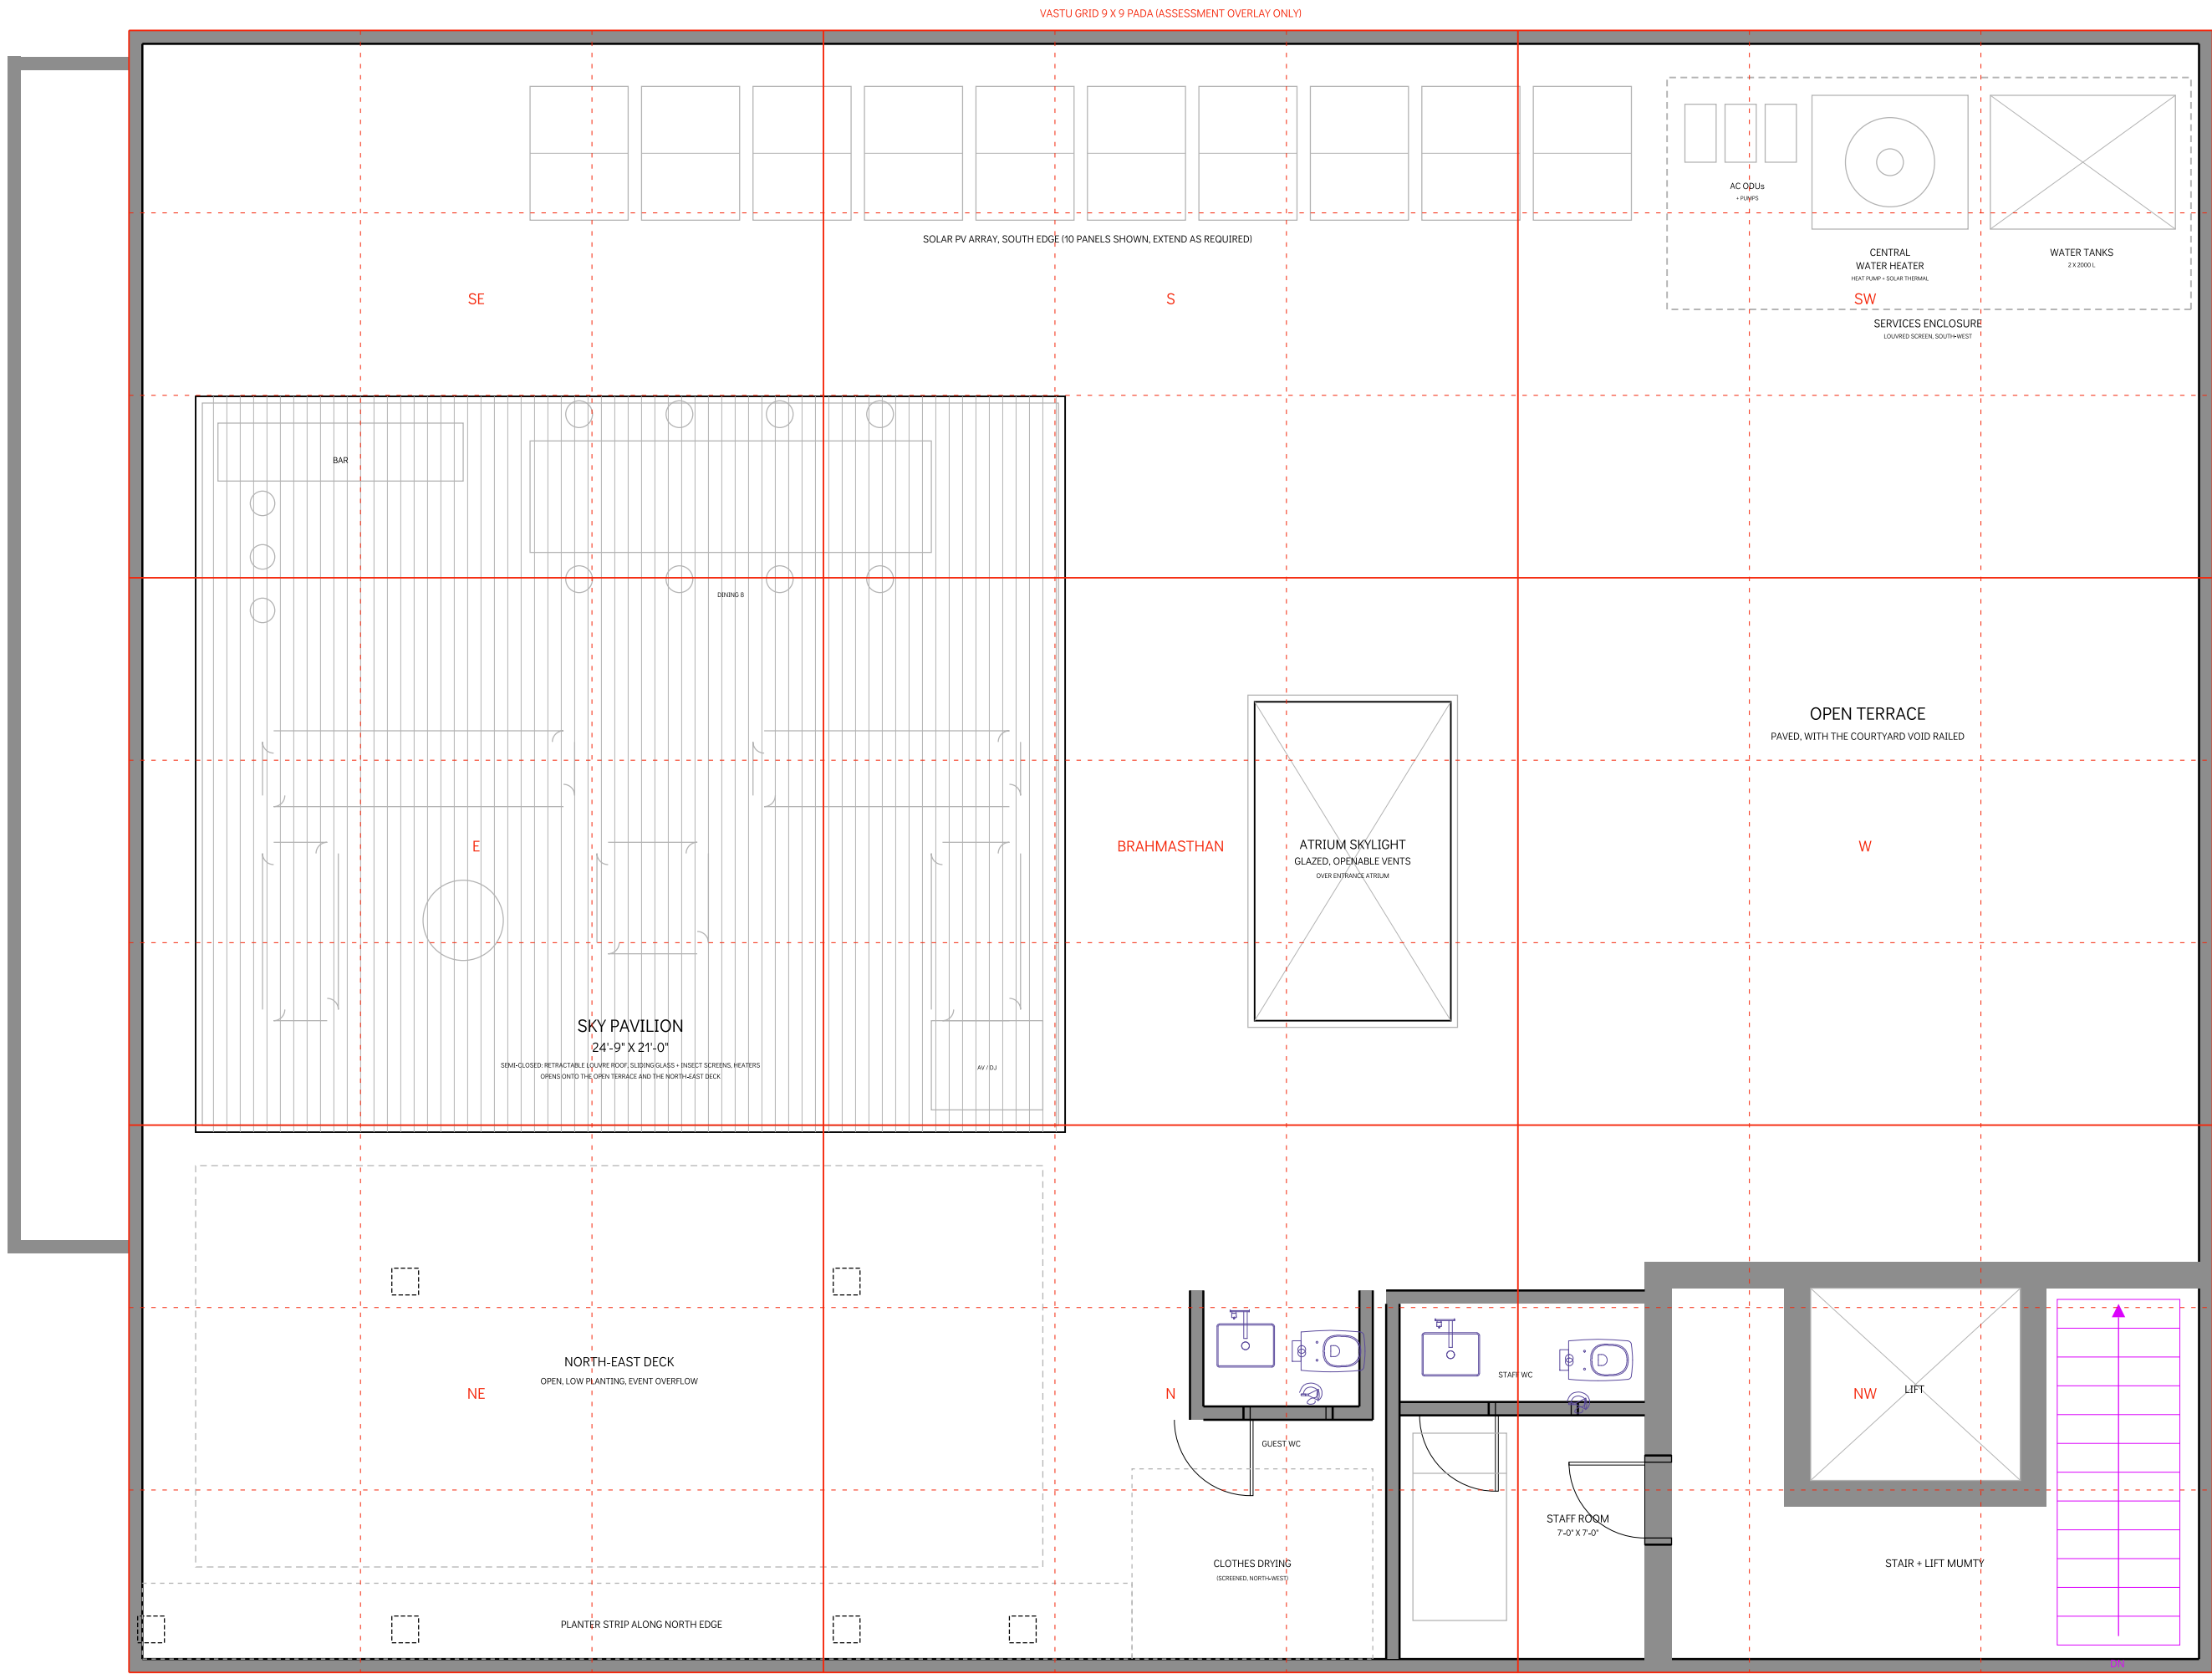

TERRACE FLOOR - LAYOUT

TF-PP-01

NOTES (TERRACE, R5):
1. PARAPET 3'-6" HIGH ALL ROUND; COURTYARD VOID RAILED. 2. WATER TANKS, CENTRAL WATER HEATER, AC OUTDOOR UNITS AND PUMPS IN A LOUVRED SERVICES ENCLOSURE IN THE SOUTH-WEST; SOLAR PV ALONG THE SOUTH PARAPET; NORTH-EAST KEPT OPEN AND LOW (VASTU).
3. SKY PAVILION ON THE EAST: STEEL FRAME, RETRACTABLE LOUVER ROOF, SLIDING GLASS WITH INSECT SCREENS, BAR, DINING AND LOUNGE; POWER AND WATER TO THE BAR. 4. STAFF ROOM, WC, GUEST WC AND SCREENED DRYING YARD BESIDE THE MUMTY (NORTH-WEST).
5. TERRACE SLAB OVER THE NORTH WING CARRIED ON THE EXTERNAL COLUMNS (DASHED); PAVILION AND SERVICES LOADS TO BE CHECKED BY THE STRUCTURAL ENGINEER. 6. WATERPROOFING AND SLOPES TO NORTH-EAST DRAIN POINTS. 7. VASTU GRID (RED) IS AN ASSESSMENT OVERLAY ONLY.