


BASEMENT -
RENOVATION LAYOUT


BF-PP-01

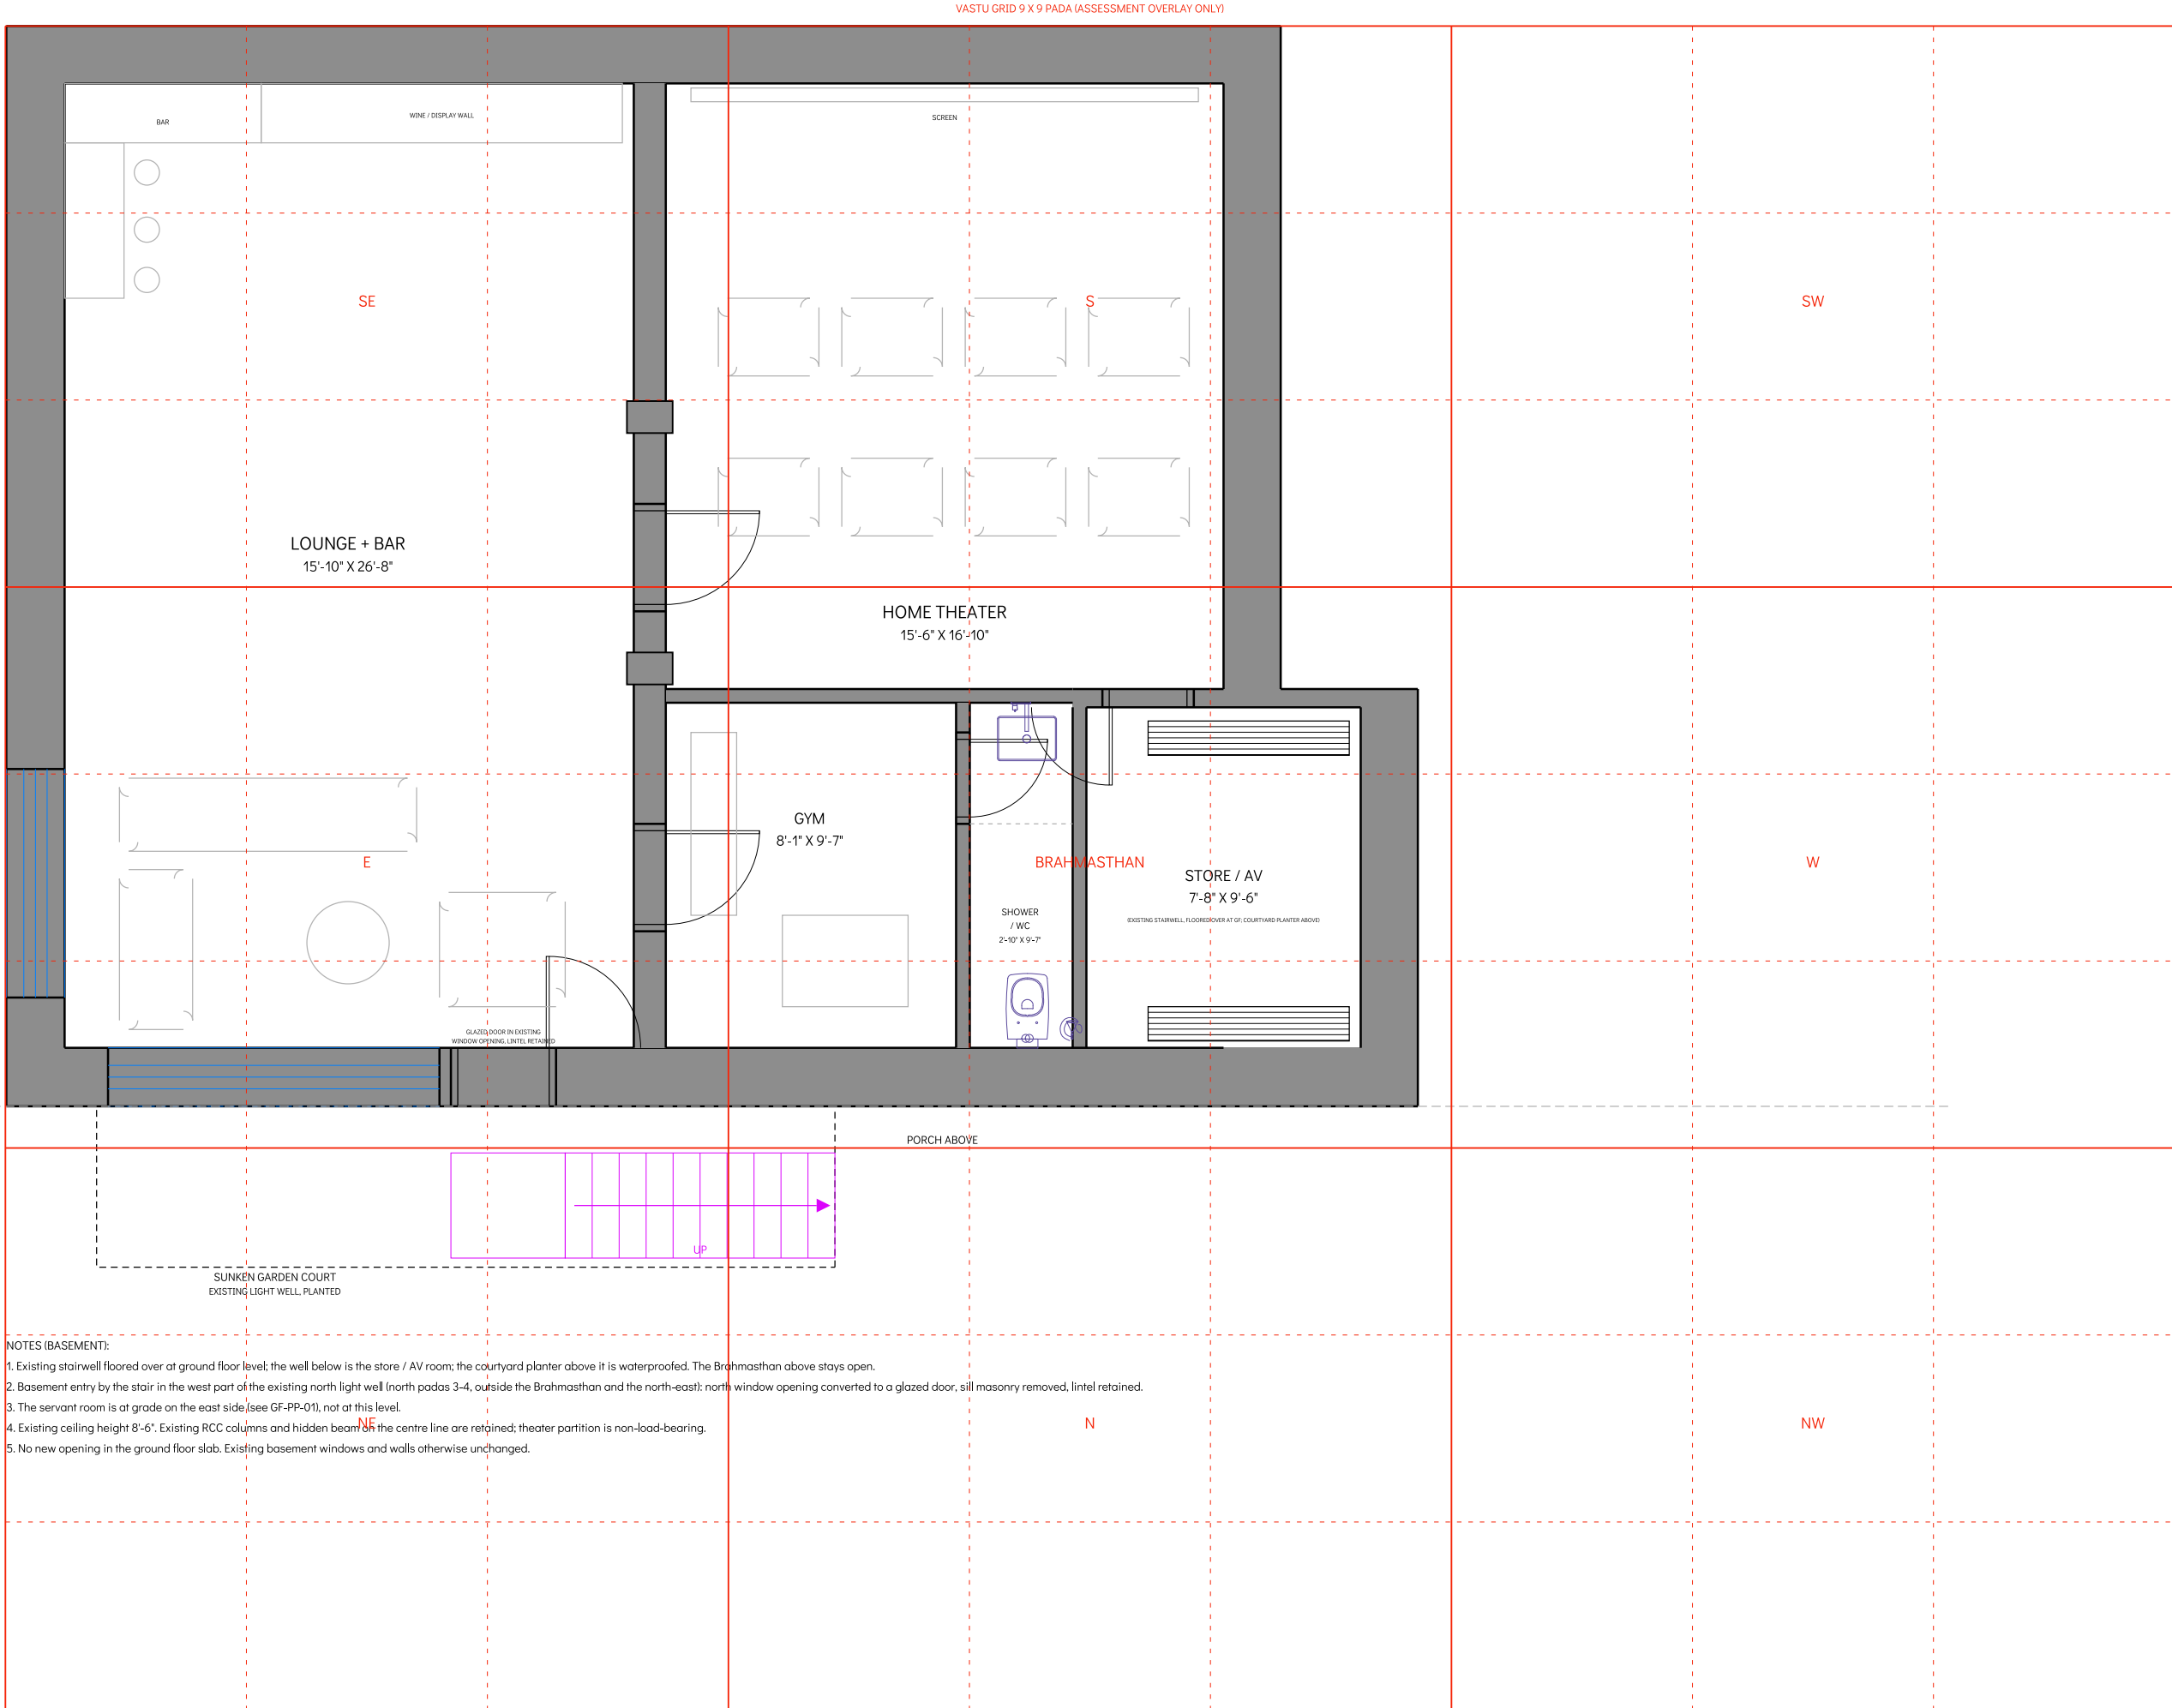

- NOTES:
1. Read this drawing along with relevant architectural, structural or service drawings.
 2. Do not scale; drawing should be read only.
 3. Any discrepancy to be brought to the notice of the architect before commencement of work.
 4. This drawing is a property of Ar. Akash Purohit and shall not be used or reproduced in any manner without the permission of the architects.

PROJECT:
17- CHANDRA PATH

SHEET TITLE:
**GROUND FLOOR -
RENOVATION LAYOUT**

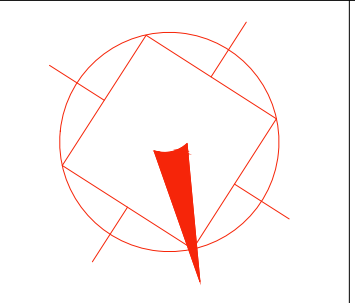

DRAWING NO:
GF-PP-01


DEALT BY: KAPIL	CHECKED BY: AKASH
--------------------	----------------------

SCALE: N.T.S.	DATE: 15-09-2026
------------------	---------------------

FILE PATH:

studio sqft

AR. AKASH PUROHIT
ar.akashpurohit@gmail.com
9784784226

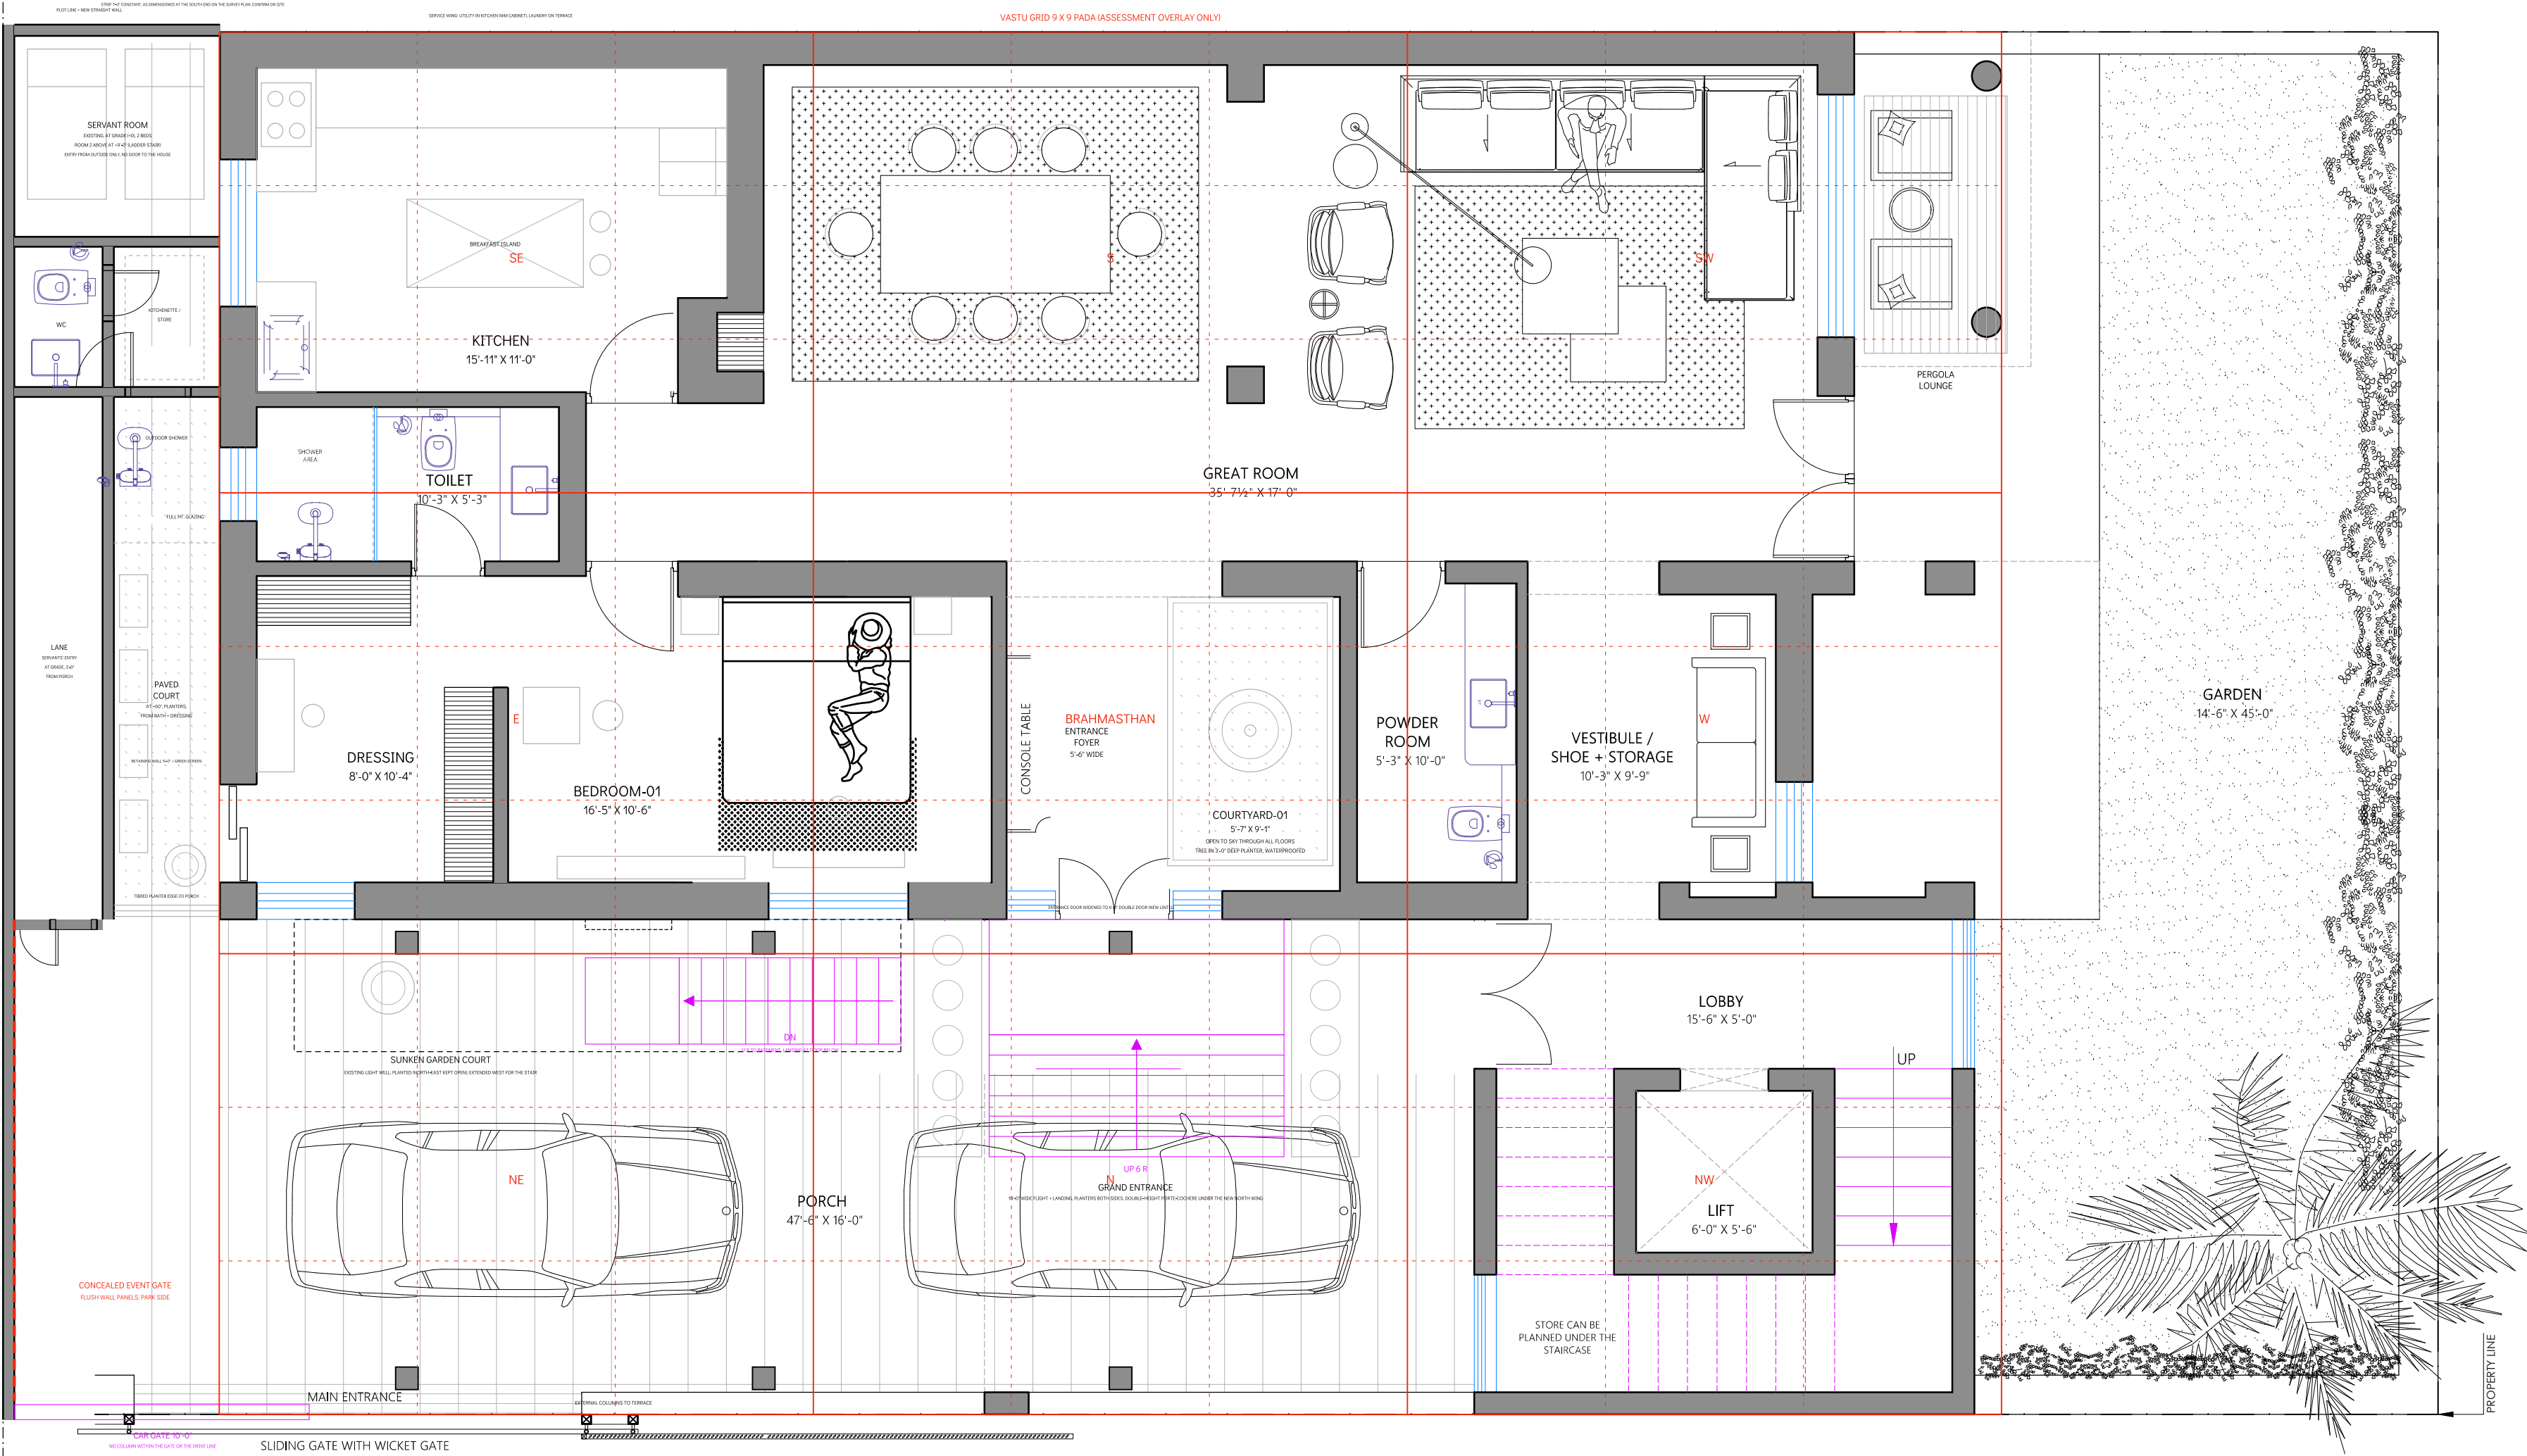


NOTES (REVISION R3):
A. EAST BOUNDARY WALL REBUILT STRAIGHT ON THE SOUTH-END LINE, TAKING THE SLANTED STRIP FROM THE PARK SIDE: 7'-0" STRIP FULL LENGTH, NO OPENINGS TO THE PARK EXCEPT THE EVENT GATE; CAR GATE 10'-0" AT THE EAST END OF THE NORTH BOUNDARY.
B. CONCEALED EVENT GATE IN THE EAST BOUNDARY WALL FROM THE HOUSE CORNER TO THE FRONT BOUNDARY: FLUSH WALL-FINISHED PANELS ON CONCEALED PIVOTS, OPENED ONLY FOR EVENTS.
C. COURTYARD-01 IN THE EXISTING STAIRWELL SHAFT, OPEN TO SKY THROUGH ALL FLOORS; THE BRAHMASTHAN CENTRE OF THE WHOLE-HOUSE GRID IS KEPT OPEN AND FREE OF STAIRS, ENTRANCE STEPS ARE A COMPACT 6-RISER FLIGHT OUTSIDE THE EXISTING DOOR; BASEMENT STAIR IN THE WEST PART OF THE EXISTING LIGHT WELL, LIFT GIVES THE STEP-FREE ROUTE.
D. EAST STRIP, SERVANT QUARTERS AT GRADE IN THE SOUTH-EAST EXISTING ROOM + ROOFED EXTENSION TO THE KITCHEN LINE, W.C. SECOND ROOM ABOVE AT +9'-0". ENTERED FROM OUTSIDE ONLY BY A 3'-0" LANE AT GRADE ALONG THE BOUNDARY WALL FROM THE PORCH; NO DOOR INTO THE HOUSE. NORTH OF THE KITCHEN LINE A RAISED PAVED COURT AT -4'-0" WITH PLANTERS AND THE OUTDOOR SHOWER, OPENING FROM THE BATHROOM (FULL-HEIGHT GLAZING) AND THE DRESSING (SLIDING DOOR), TIERED PLANTER EDGE STEPPING DOWN TO THE PORCH.
E. SERVICE WING ROOFED AT 7'-6" WITH A PLANTER PARAPET, BATHROOM EAST WINDOW IN OBSCURE GLASS, GRAND ENTRANCE: 10'-0" FLIGHT CENTRED ON THE WIDENED FRONT DOOR NORTH PADA S, BELOW THE BRAHMASTHAN LINE, BASEMENT STAIR IN THE NORTH LIGHT WELL. THE WHOLE BLOCK OVER THE PORCH LOBBY, LIFT, MAIN STAIR, UPPER LIVING ROOMS/IS DEMOLISHED AND REBUILT ON THE NEW COLUMN GRID; LIFT AND MAIN STAIR STAY IN THE NORTH-WEST.
F. VASTU GRID (RED) COVERS THE WHOLE BUILT HOUSE INCLUDING THE PORCH LEVEL UNDER THE UPPER FLOORS; ASSESSMENT OVERLAY ONLY. SHEET ORIENTATION: TOP = SOUTH, BOTTOM = NORTH, LEFT = EAST, RIGHT = WEST.

- NOTES:
1. Read this drawing along with relevant architectural, structural or service drawings.
 2. Do not scale; drawing should be read only.
 3. Any discrepancy to be brought to the notice of the architect before commencement of work.
 4. This drawing is a property of Ar. Akash Purohit and shall not be used or reproduced in any manner without the permission of the architects.

PROJECT:
17- CHANDRA PATH


SHEET TITLE:
**FIRST FLOOR -
RENOVATION LAYOUT**

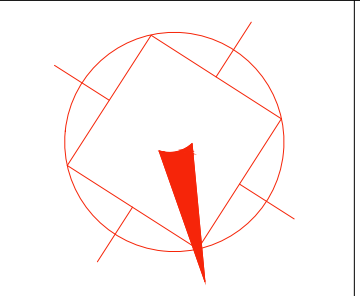

DRAWING NO: FF-PP-01	
DEALT BY: KAPIL	CHECKED BY: AKASH
SCALE: N.T.S.	DATE: 15-09-2026
FILE PATH:	


studio sqft

AR. AKASH PUROHIT
ar.akashpurohit@gmail.com
9784784226

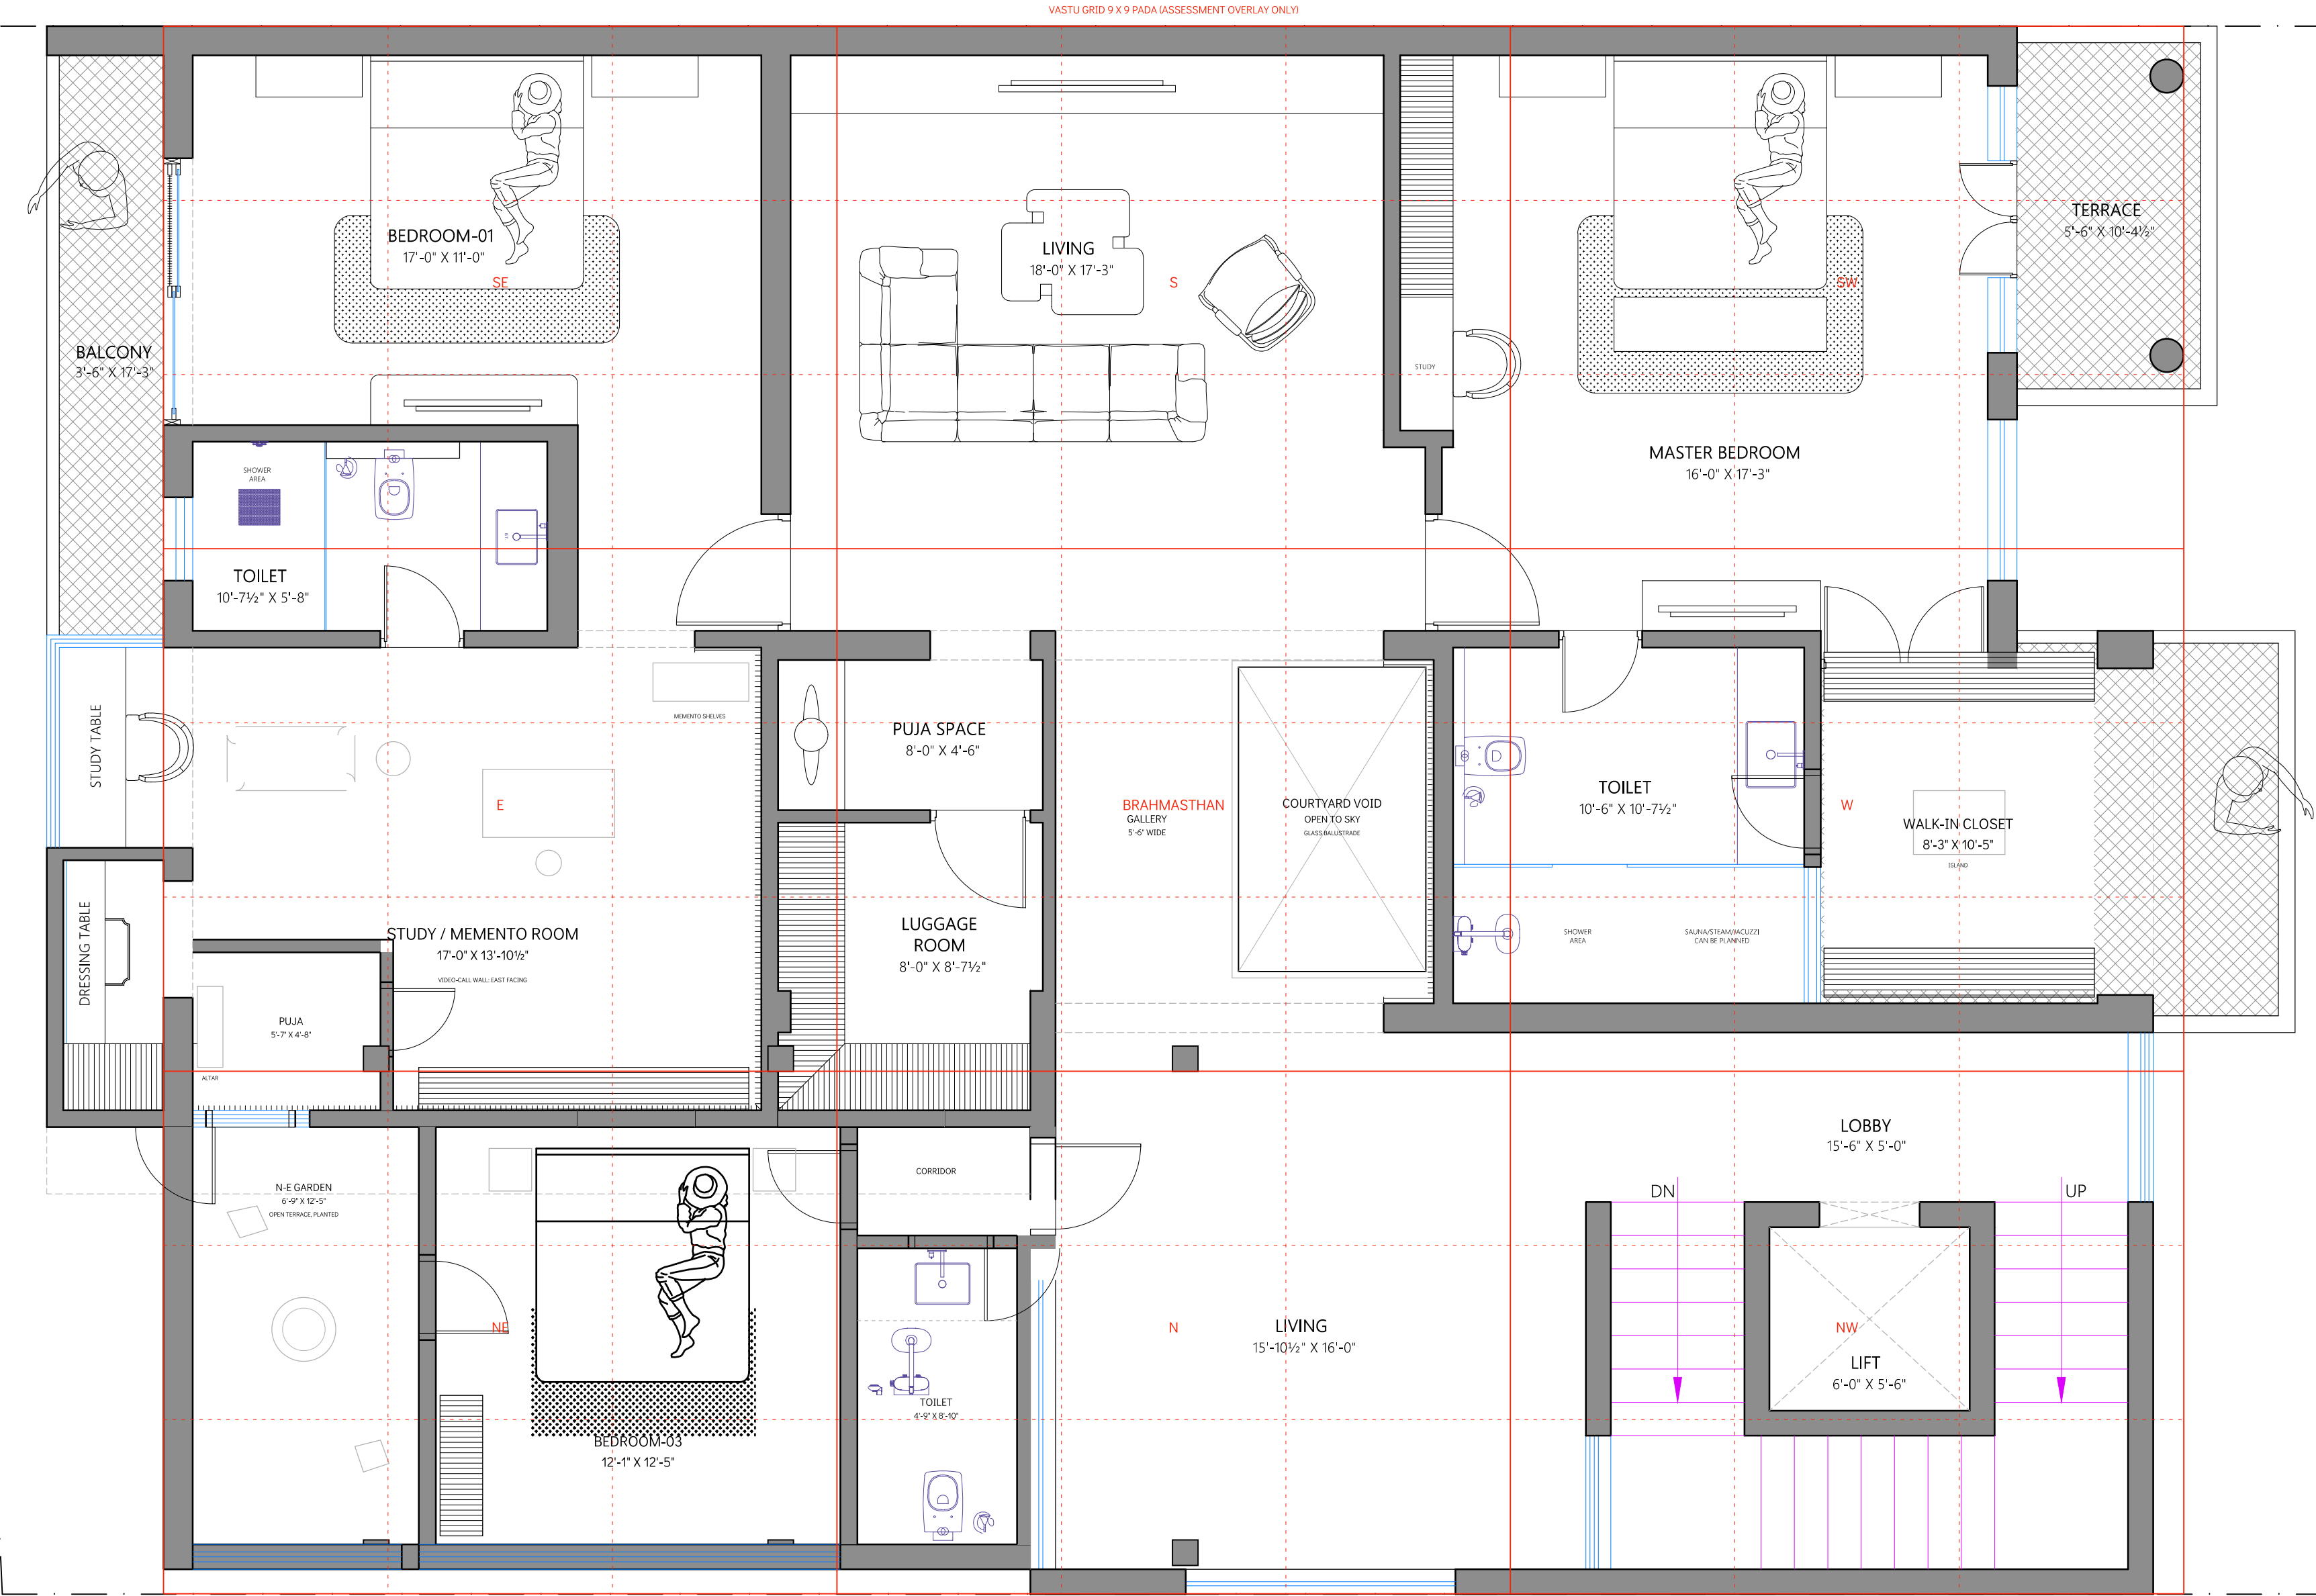

NOTES (FIRST FLOOR, R3):

1. THE BLOCK OVER THE PORCH IS REBUILT FROM SCRATCH ON RCC COLUMNS FROM FOUNDATION TO TERRACE (THREE ON THE PORCH LINE, THREE AT THE BACK AGAINST THE NORTH WALL, NONE WITHIN THE 10'-0" CAR GATE OR THE DRIVE LINE), INDEPENDENT OF THE STONE WALLS; TO STRUCTURAL DESIGN.
2. FORMER WEST TERRACE ENCLOSED AS MASTER WALK-IN CLOSET (LIGHT PARTITIONS ON EXISTING SLAB); 3. NORTH-EAST ROOM RE-PURPOSED AS STUDY WITH PUJA IN ITS NORTH-EAST CORNER.
4. COURTYARD VOID WITHIN THE EXISTING STAIRWELL SHAFT; GLASS BALUSTRADE; 5. VASTU GRID (RED) IS AN ASSESSMENT OVERLAY ONLY.

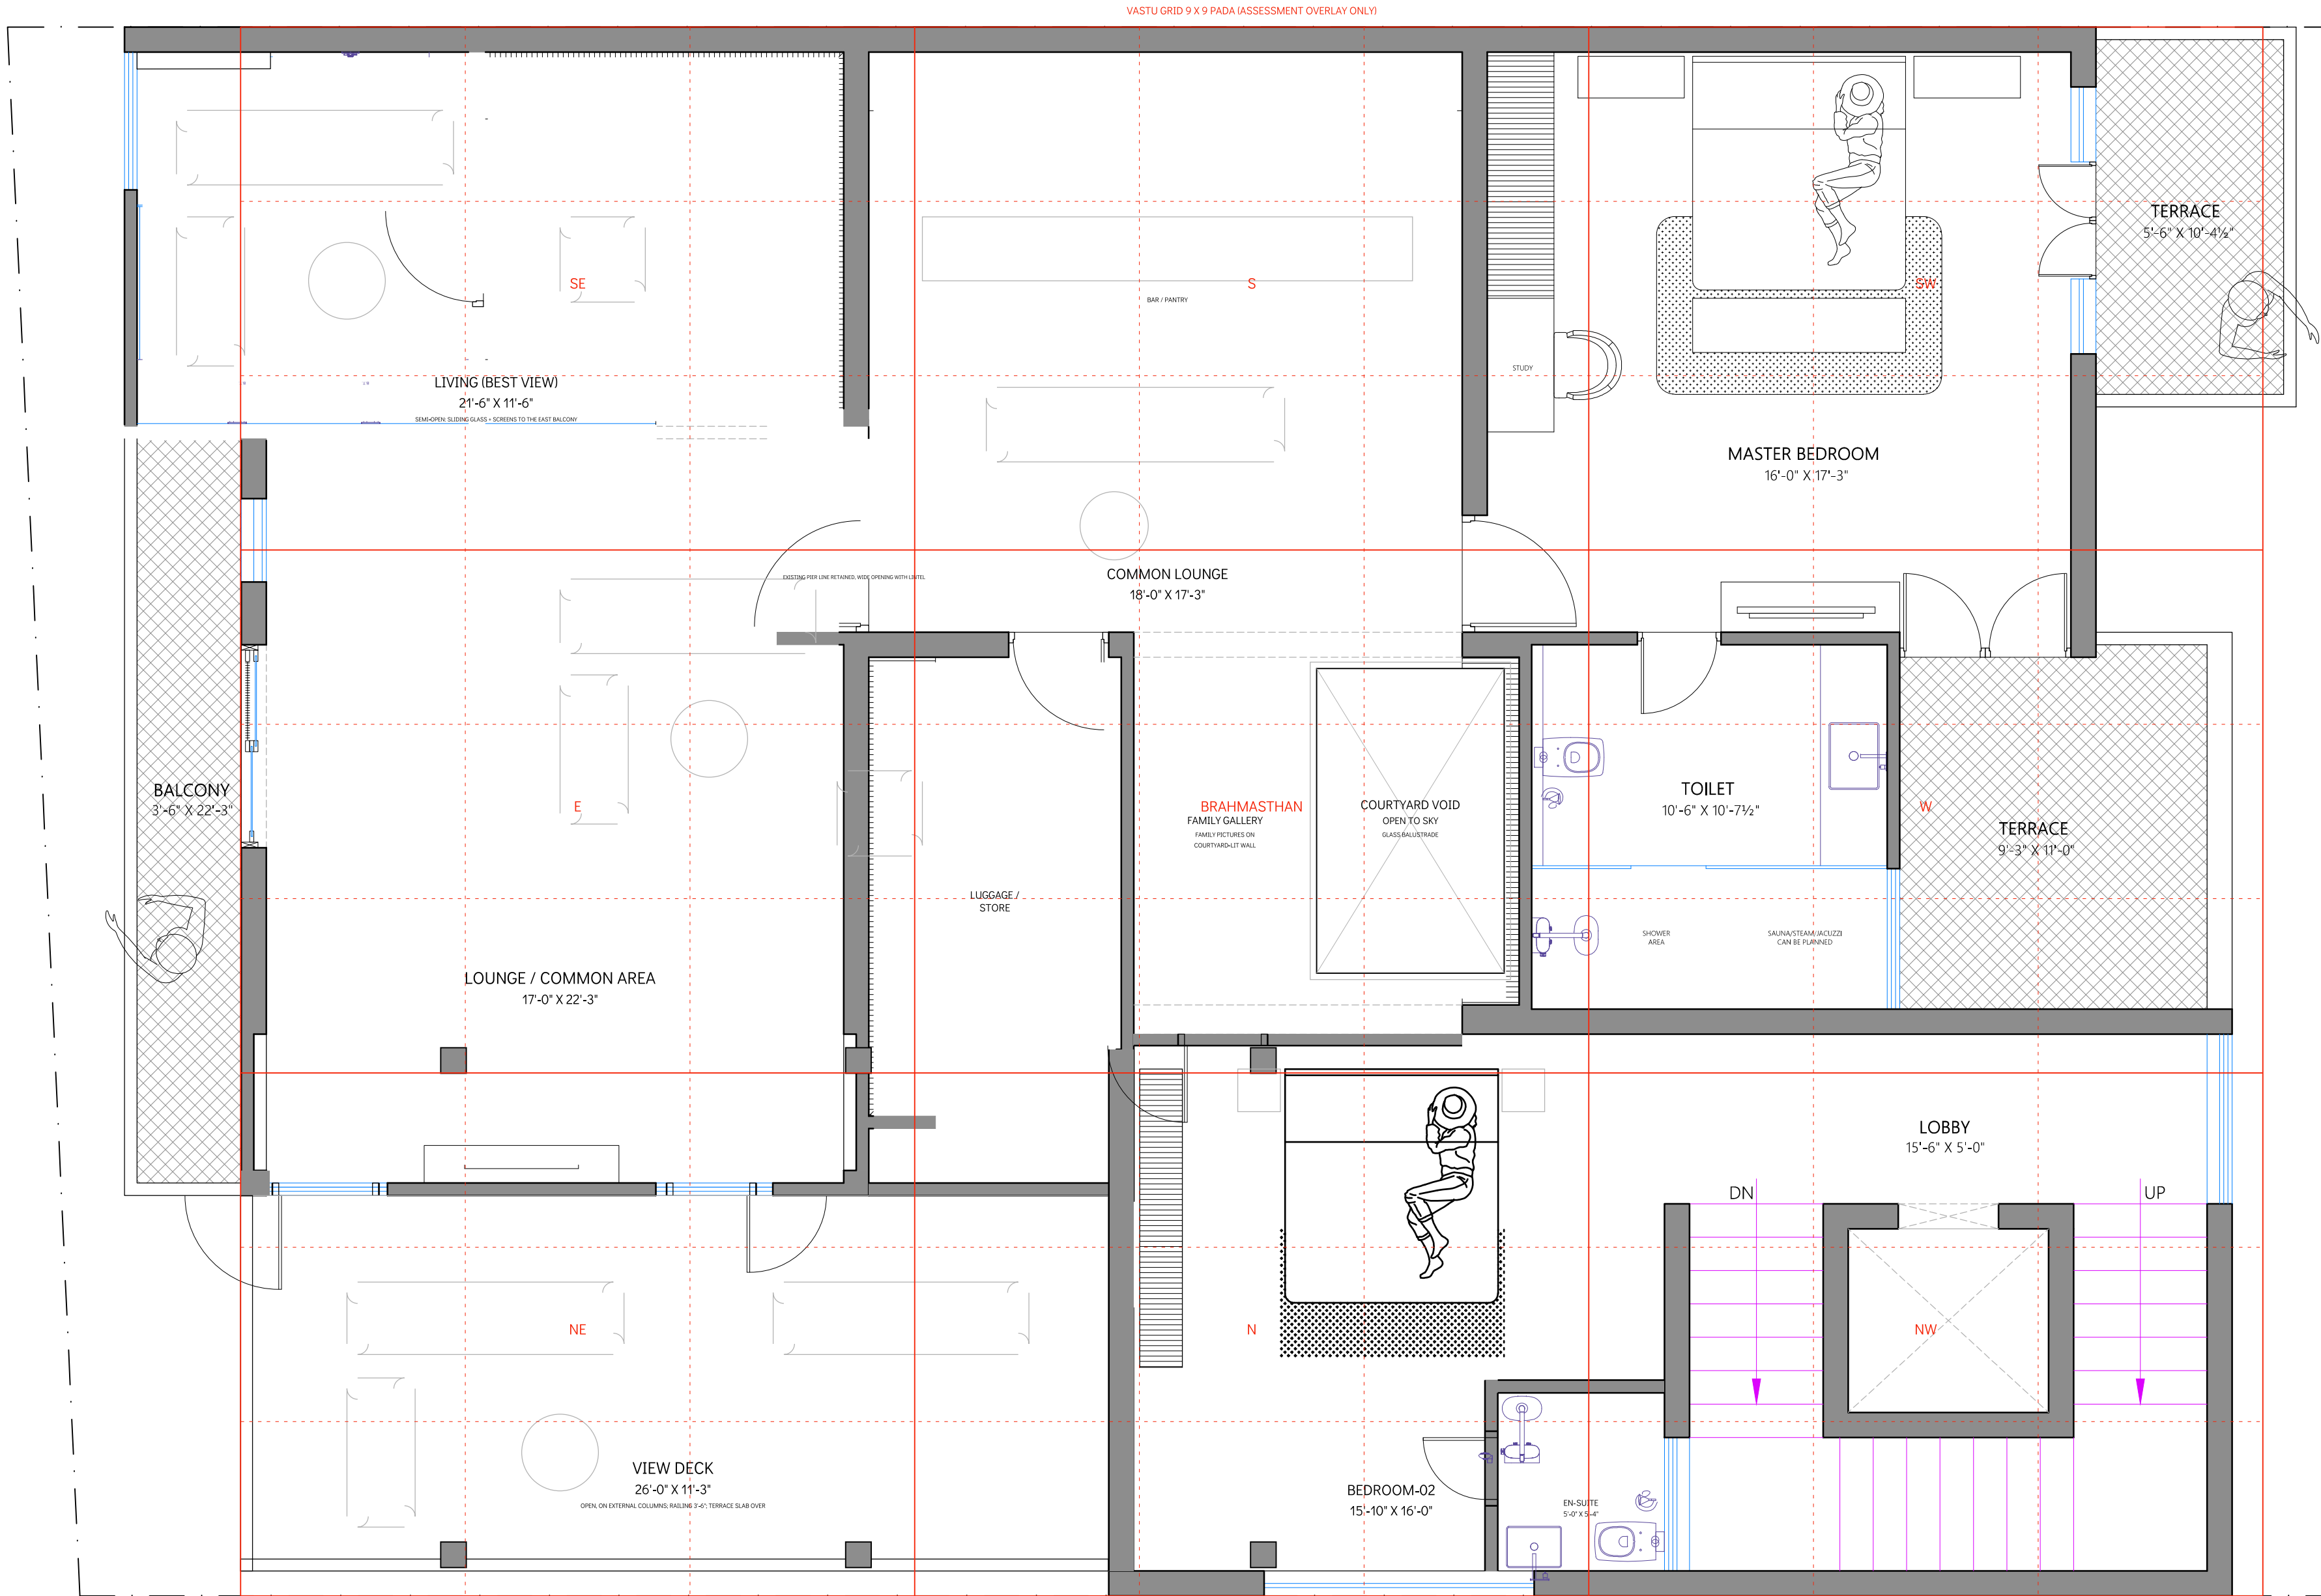

NOTES (SECOND FLOOR, R3):

1. SOUTH-EAST TOILET, WALK-IN CLOSET AND BEDROOM-02 REMOVED; THE SOUTH-EAST CORNER WITH THE BEST VIEW BECOMES THE LIVING ROOM, THE REST A COMMON LOUNGE. FORMER NORTH WINDOWS BECOME DOORS TO THE GARDEN AND BEDROOM-02, OR ARE INFILLED.


2. BEDROOM-02 WITH EN-SUITE IN THE FORMER LIVING OVER THE PORCH (NORTH-WEST); THE NEW EAST WING AT THIS LEVEL IS AN OPEN VIEW DECK ON EXTERNAL COLUMNS, NO WALLS. 3. STRUCTURAL WALL LINES RETAINED AS PIERS; OPENINGS WITH LINTELS.

4. FAMILY GALLERY ALONG THE COURTYARD VOID. 5. VASTU GRID (RED) IS AN ASSESSMENT OVERLAY ONLY.

- NOTES:
1. Read this drawing along with relevant architectural, structural or service drawings.
 2. Do not scale; drawing should be read only.
 3. Any discrepancy to be brought to the notice of the architect before commencement of work.
 4. This drawing is a property of Ar. Akash Purohit and shall not be used or reproduced in any manner without the permission of the architects.

PROJECT:
17- CHANDRA PATH

SHEET TITLE:
SECOND FLOOR- LAYOUT

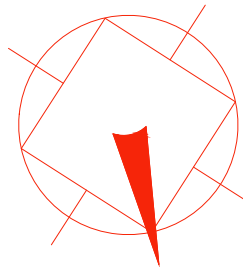

DRAWING NO:
SF-PP-01

DEALT BY:
KAPIL

CHECKED BY:
AKASH


SCALE:
N.T.S.

DATE:
15-09-2026

FILE PATH:

studio sqft

AR. AKASH PUROHIT
ar.akashpurohit@gmail.com
9784784226

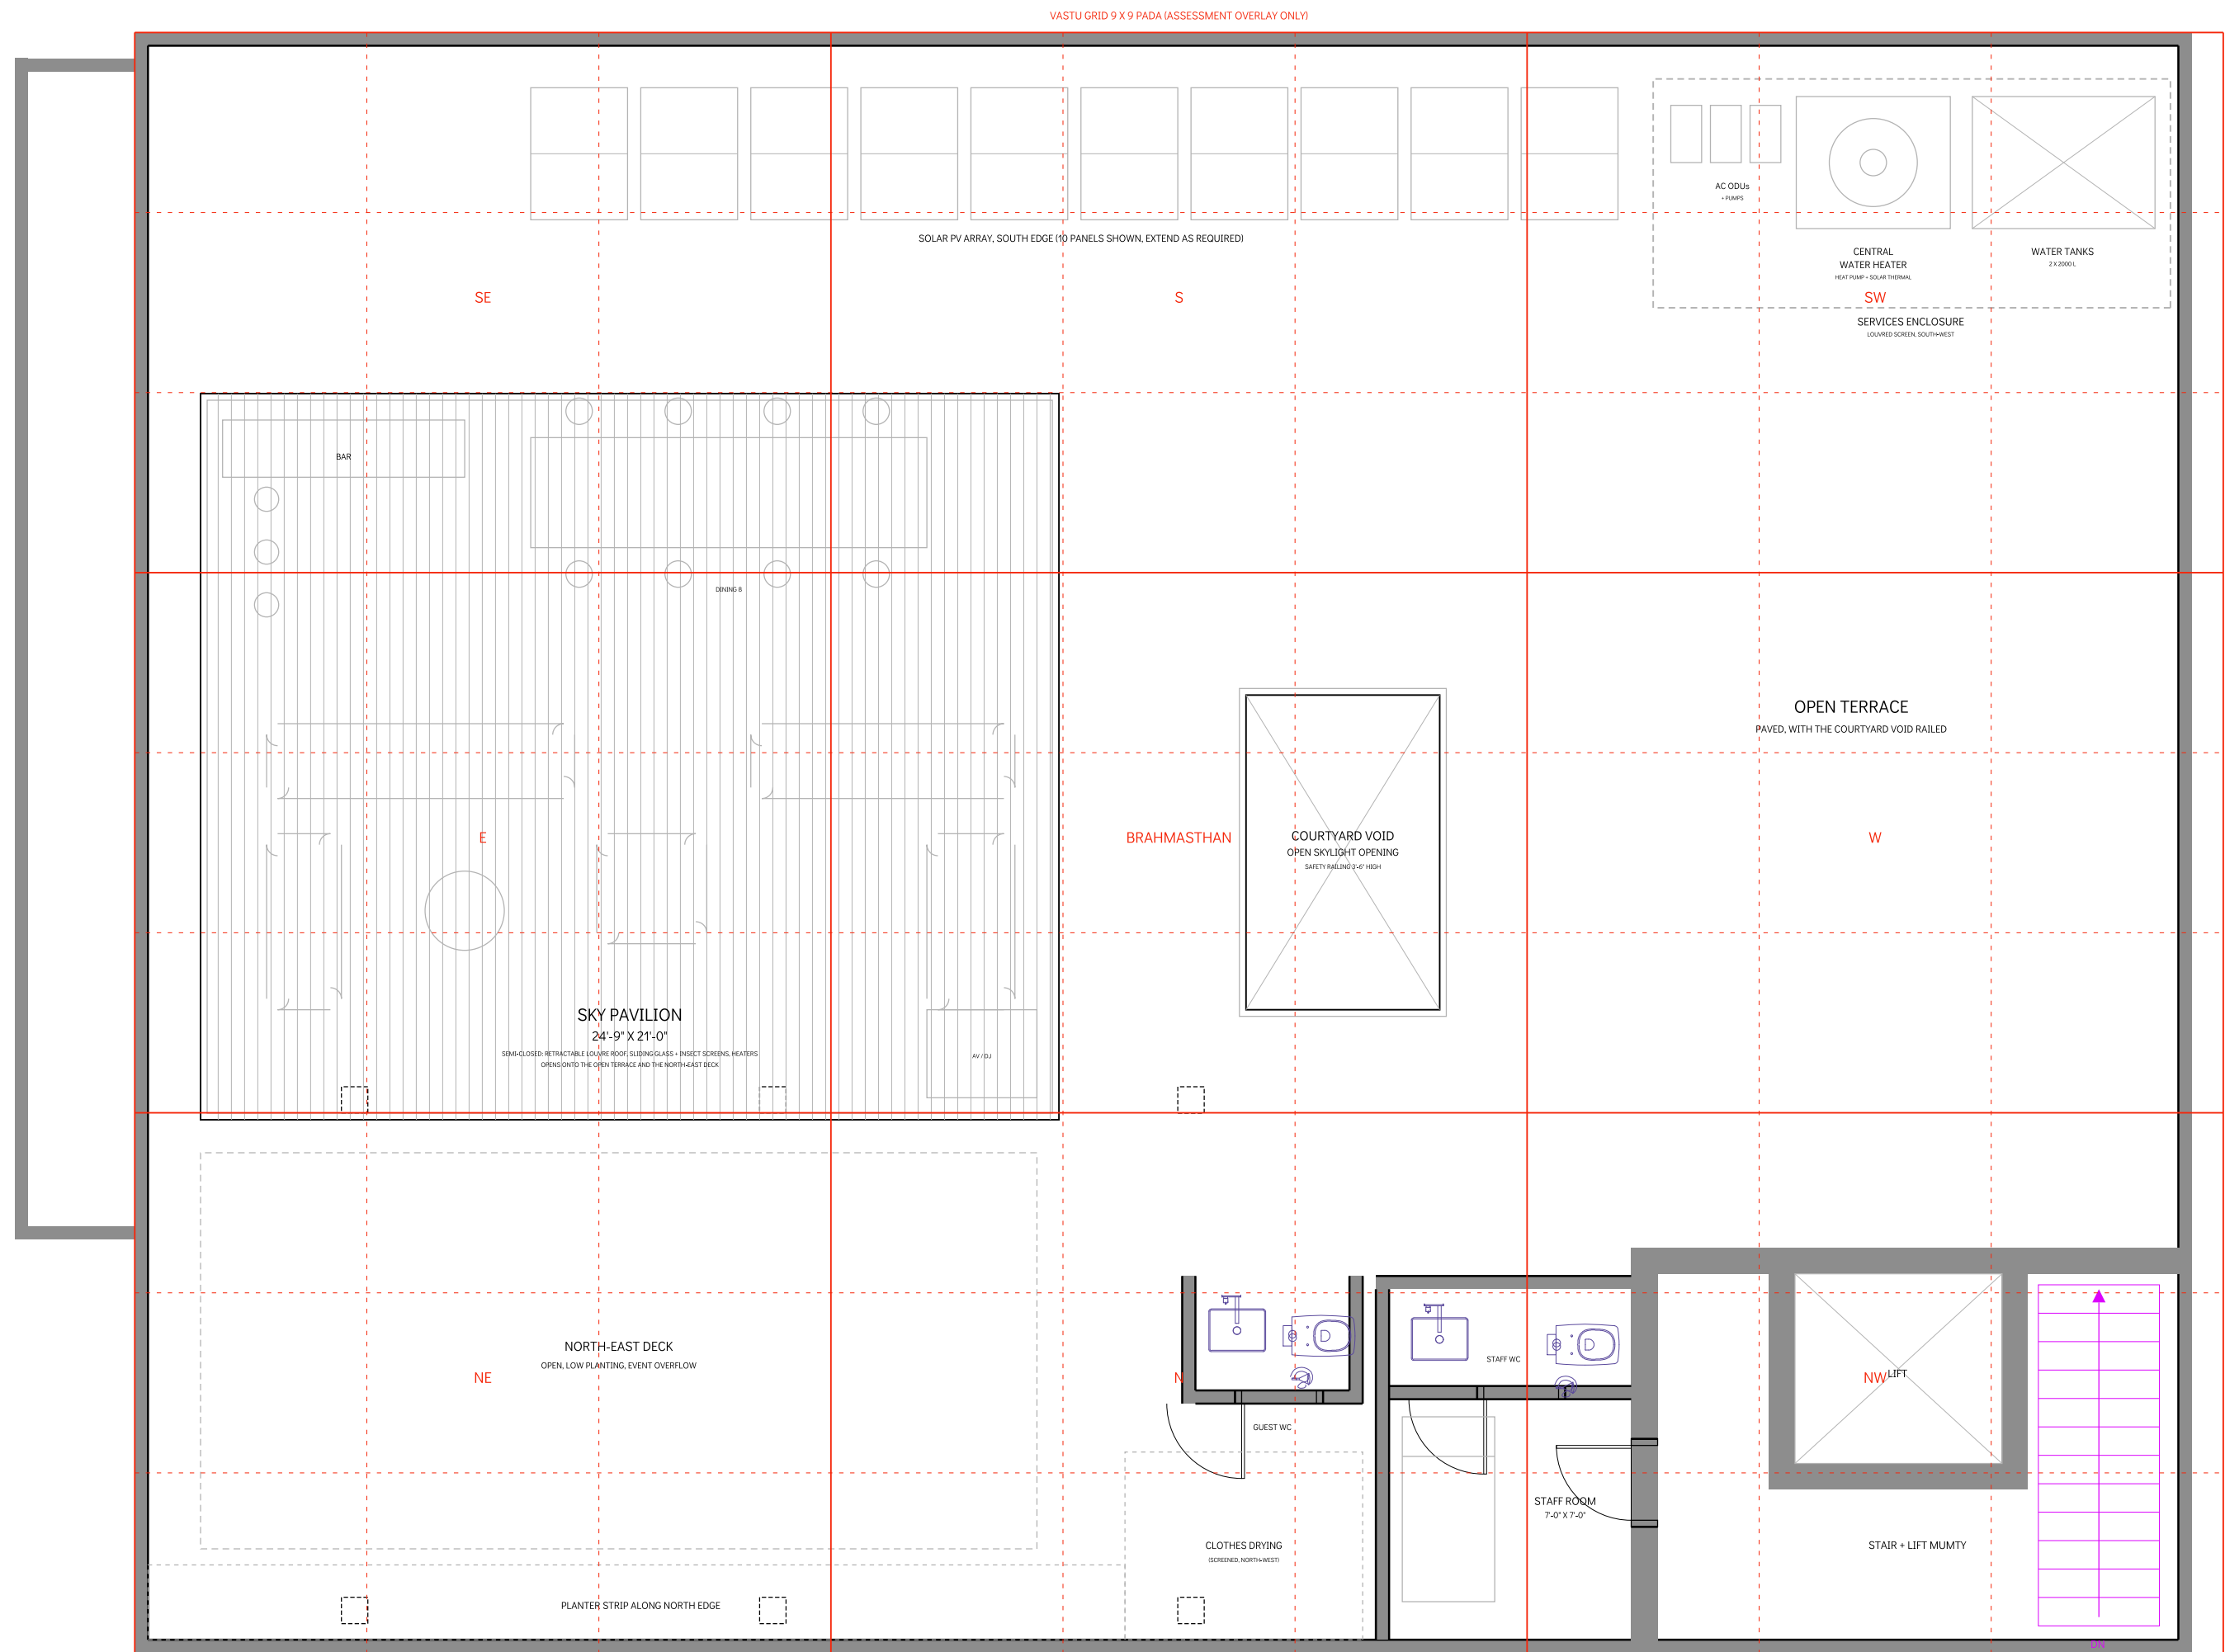

TERRACE FLOOR - LAYOUT

TF-PP-01

NOTES (TERRACE, R5):

1. PARAPET 3'-6" HIGH ALL ROUND; COURTYARD VOID RAILED. 2. WATER TANKS, CENTRAL WATER HEATER, AC OUTDOOR UNITS AND PUMPS IN A LOUVRED SERVICES ENCLOSURE IN THE SOUTH-WEST; SOLAR PV ALONG THE SOUTH PARAPET; NORTH-EAST KEPT OPEN AND LOW (VASTU).
3. SKY PAVILION ON THE EAST: STEEL FRAME, RETRACTABLE LOUVRE ROOF, SLIDING GLASS WITH INSECT SCREENS, BAR, DINING AND LOUNGE; POWER AND WATER TO THE BAR. 4. STAFF ROOM, WC, GUEST WC AND SCREENED DRYING YARD BESIDE THE MUMTY (NORTH-WEST).
5. TERRACE SLAB OVER THE NORTH WING CARRIED ON THE EXTERNAL COLUMNS (DASHED); PAVILION AND SERVICES LOADS TO BE CHECKED BY THE STRUCTURAL ENGINEER. 6. WATERPROOFING AND SLOPES TO NORTH-EAST DRAIN POINTS. 7. VASTU GRID (RED) IS AN ASSESSMENT OVERLAY ONLY.