





BASEMENT -
RENOVATION LAYOUT

BF-PP-01

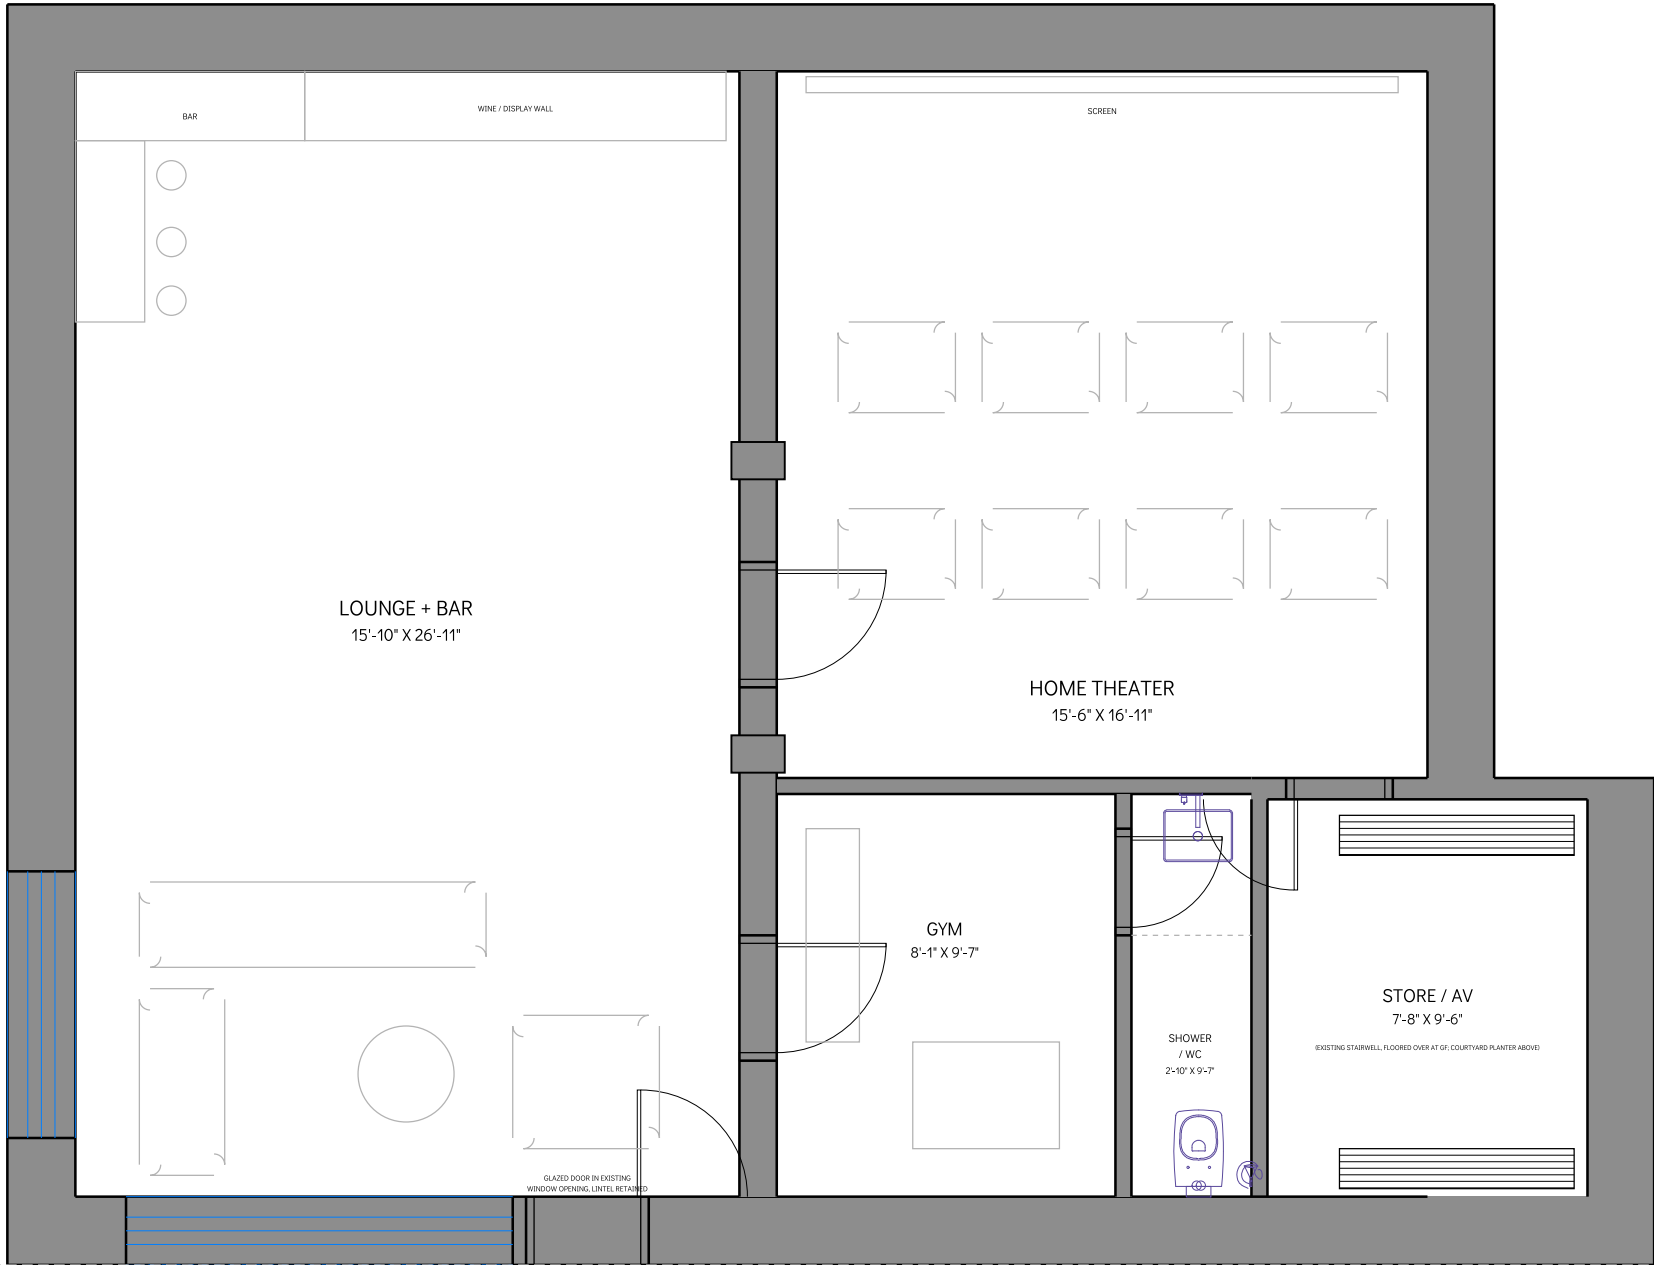

NOTES (BASEMENT):


- Existing stairwell floored over at ground floor level; the well below is the store / AV room; the courtyard planter above it is waterproofed. The Brahmashan above stays open.
- Basement entry by the stair in the west part of the existing north light well (north padas 3-4, outside the Brahmashan and the north-east); north window opening converted to a glazed door, sill masonry removed, lintel retained.
- The servant room is at grade on the east side (see GF-PP-01), not at this level.
- Existing ceiling height 8'-6". Existing RCC columns and hidden beam on the centre line are retained; theater partition is non-load-bearing.
- No new opening in the ground floor slab. Existing basement windows and walls otherwise unchanged.

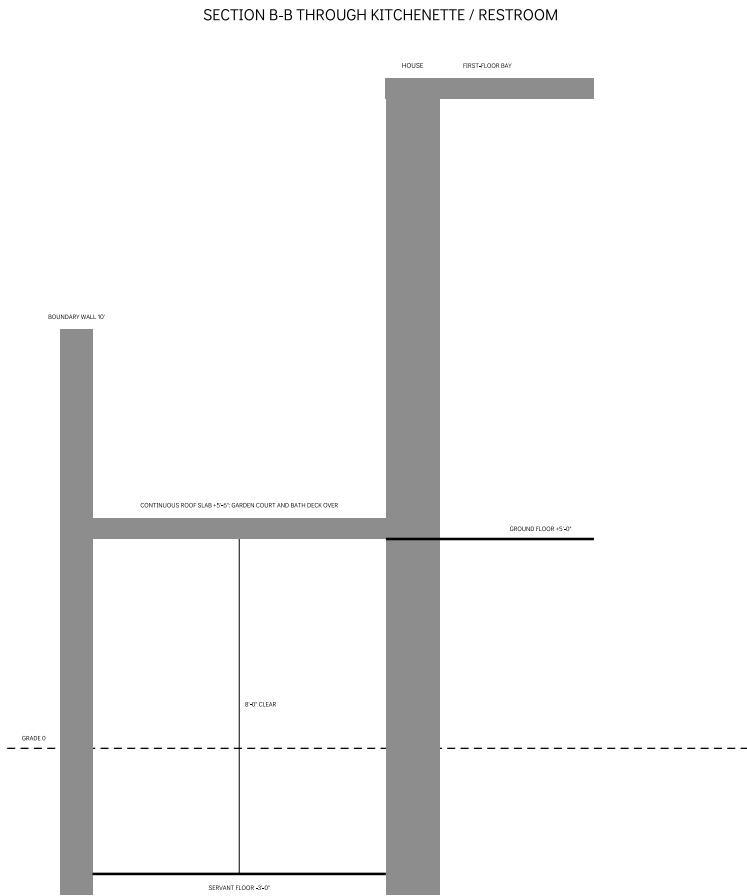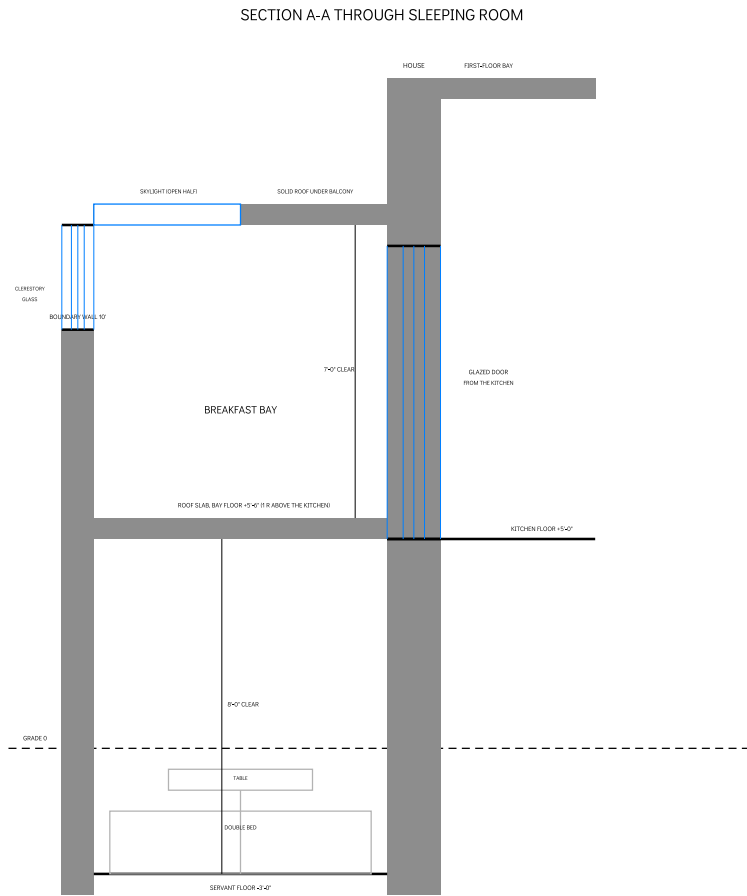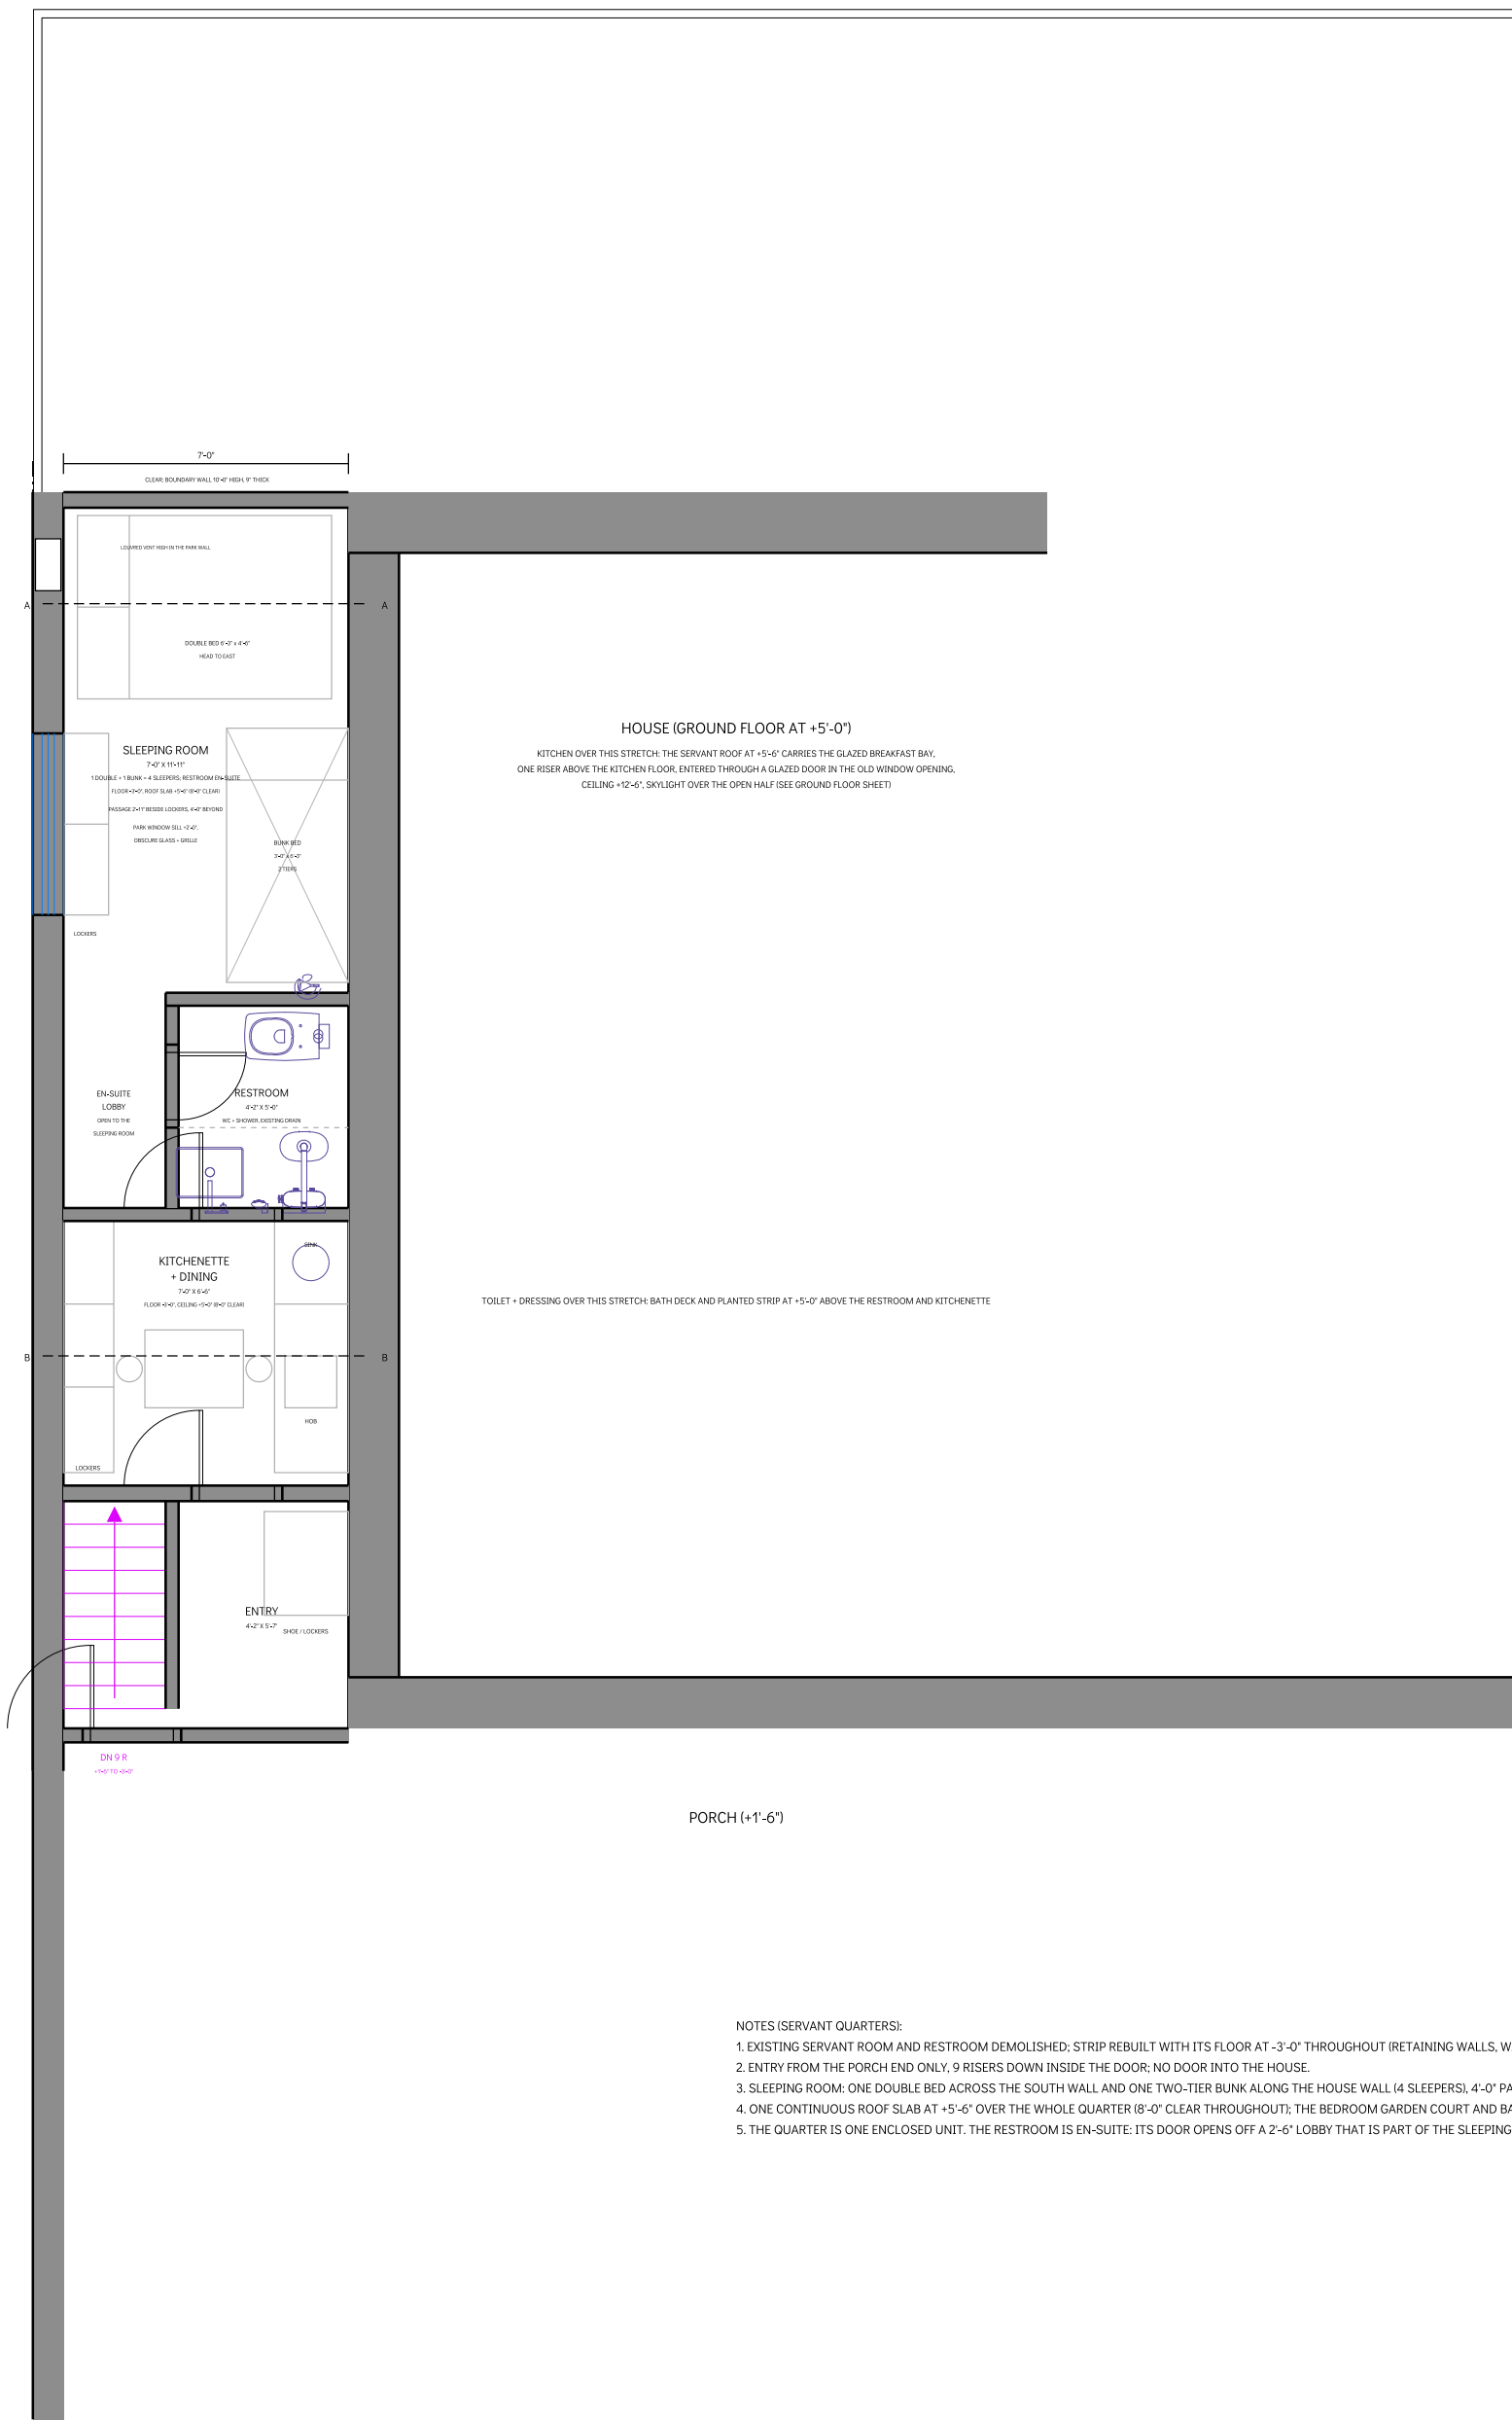

SERVANT QUARTERS -
GRADE LEVEL LAYOUT

- NOTES (SERVANT QUARTERS):
- EXISTING SERVANT ROOM AND RESTROOM DEMOLISHED; STRIP REBUILT WITH ITS FLOOR AT -3'-0" THROUGHOUT (RETAINING WALLS, WATERPROOFED, SUMP + PUMP FOR DRAINAGE).
 - ENTRY FROM THE PORCH END ONLY, 9 RISERS DOWN INSIDE THE DOOR; NO DOOR INTO THE HOUSE.
 - SLEEPING ROOM: ONE DOUBLE BED ACROSS THE SOUTH WALL AND ONE TWO-TIER BUNK ALONG THE HOUSE WALL (4 SLEEPERS); 4'-0" PASSAGE WITH LOCKERS UNDER THE PARK WINDOW; SINGLE HEIGHT FLOOR -3'-0"; ROOF SLAB AT +5'-6" (8'-0" CLEAR); THE ROOF CARRIES THE GLAZED BREAKFAST BAY OFF THE KITCHEN (FLOOR +5'-6"; CEILING +12'-6"), DESIGNED FOR THAT LOAD, WATERPROOFED, LOUVERED VENT HIGH IN THE PARK WALL FOR CROSS-VENTILATION WITH THE DOOR.
 - ONE CONTINUOUS ROOF SLAB AT +5'-6" OVER THE WHOLE QUARTER (8'-0" CLEAR THROUGHOUT); THE BEDROOM GARDEN COURT AND BATH DECK SIT ON IT; RESTROOM ON THE EXISTING DRAIN, HIGH LEVEL VENT TO THE PATH.
 - THE QUARTER IS ONE ENCLOSED UNIT; THE RESTROOM IS EN-SUITE; ITS DOOR OPENS OFF A 2'-6" LOBBY THAT IS PART OF THE SLEEPING ROOM; THE KITCHENETTE CONNECTS THROUGH THE SAME LOBBY; NO OUTDOOR ROUTE BETWEEN ANY ROOMS; WINDOW TO THE PARK IN THE SLEEPING ROOM AS EXISTING, SILL +2'-0" (5'-0" ABOVE THE SERVANT FLOOR), OBSCURE GLASS WITH A GRILLE. ALL DIMENSIONS ARE CLEAR INTERNAL SIZES.

SQ-PP-05

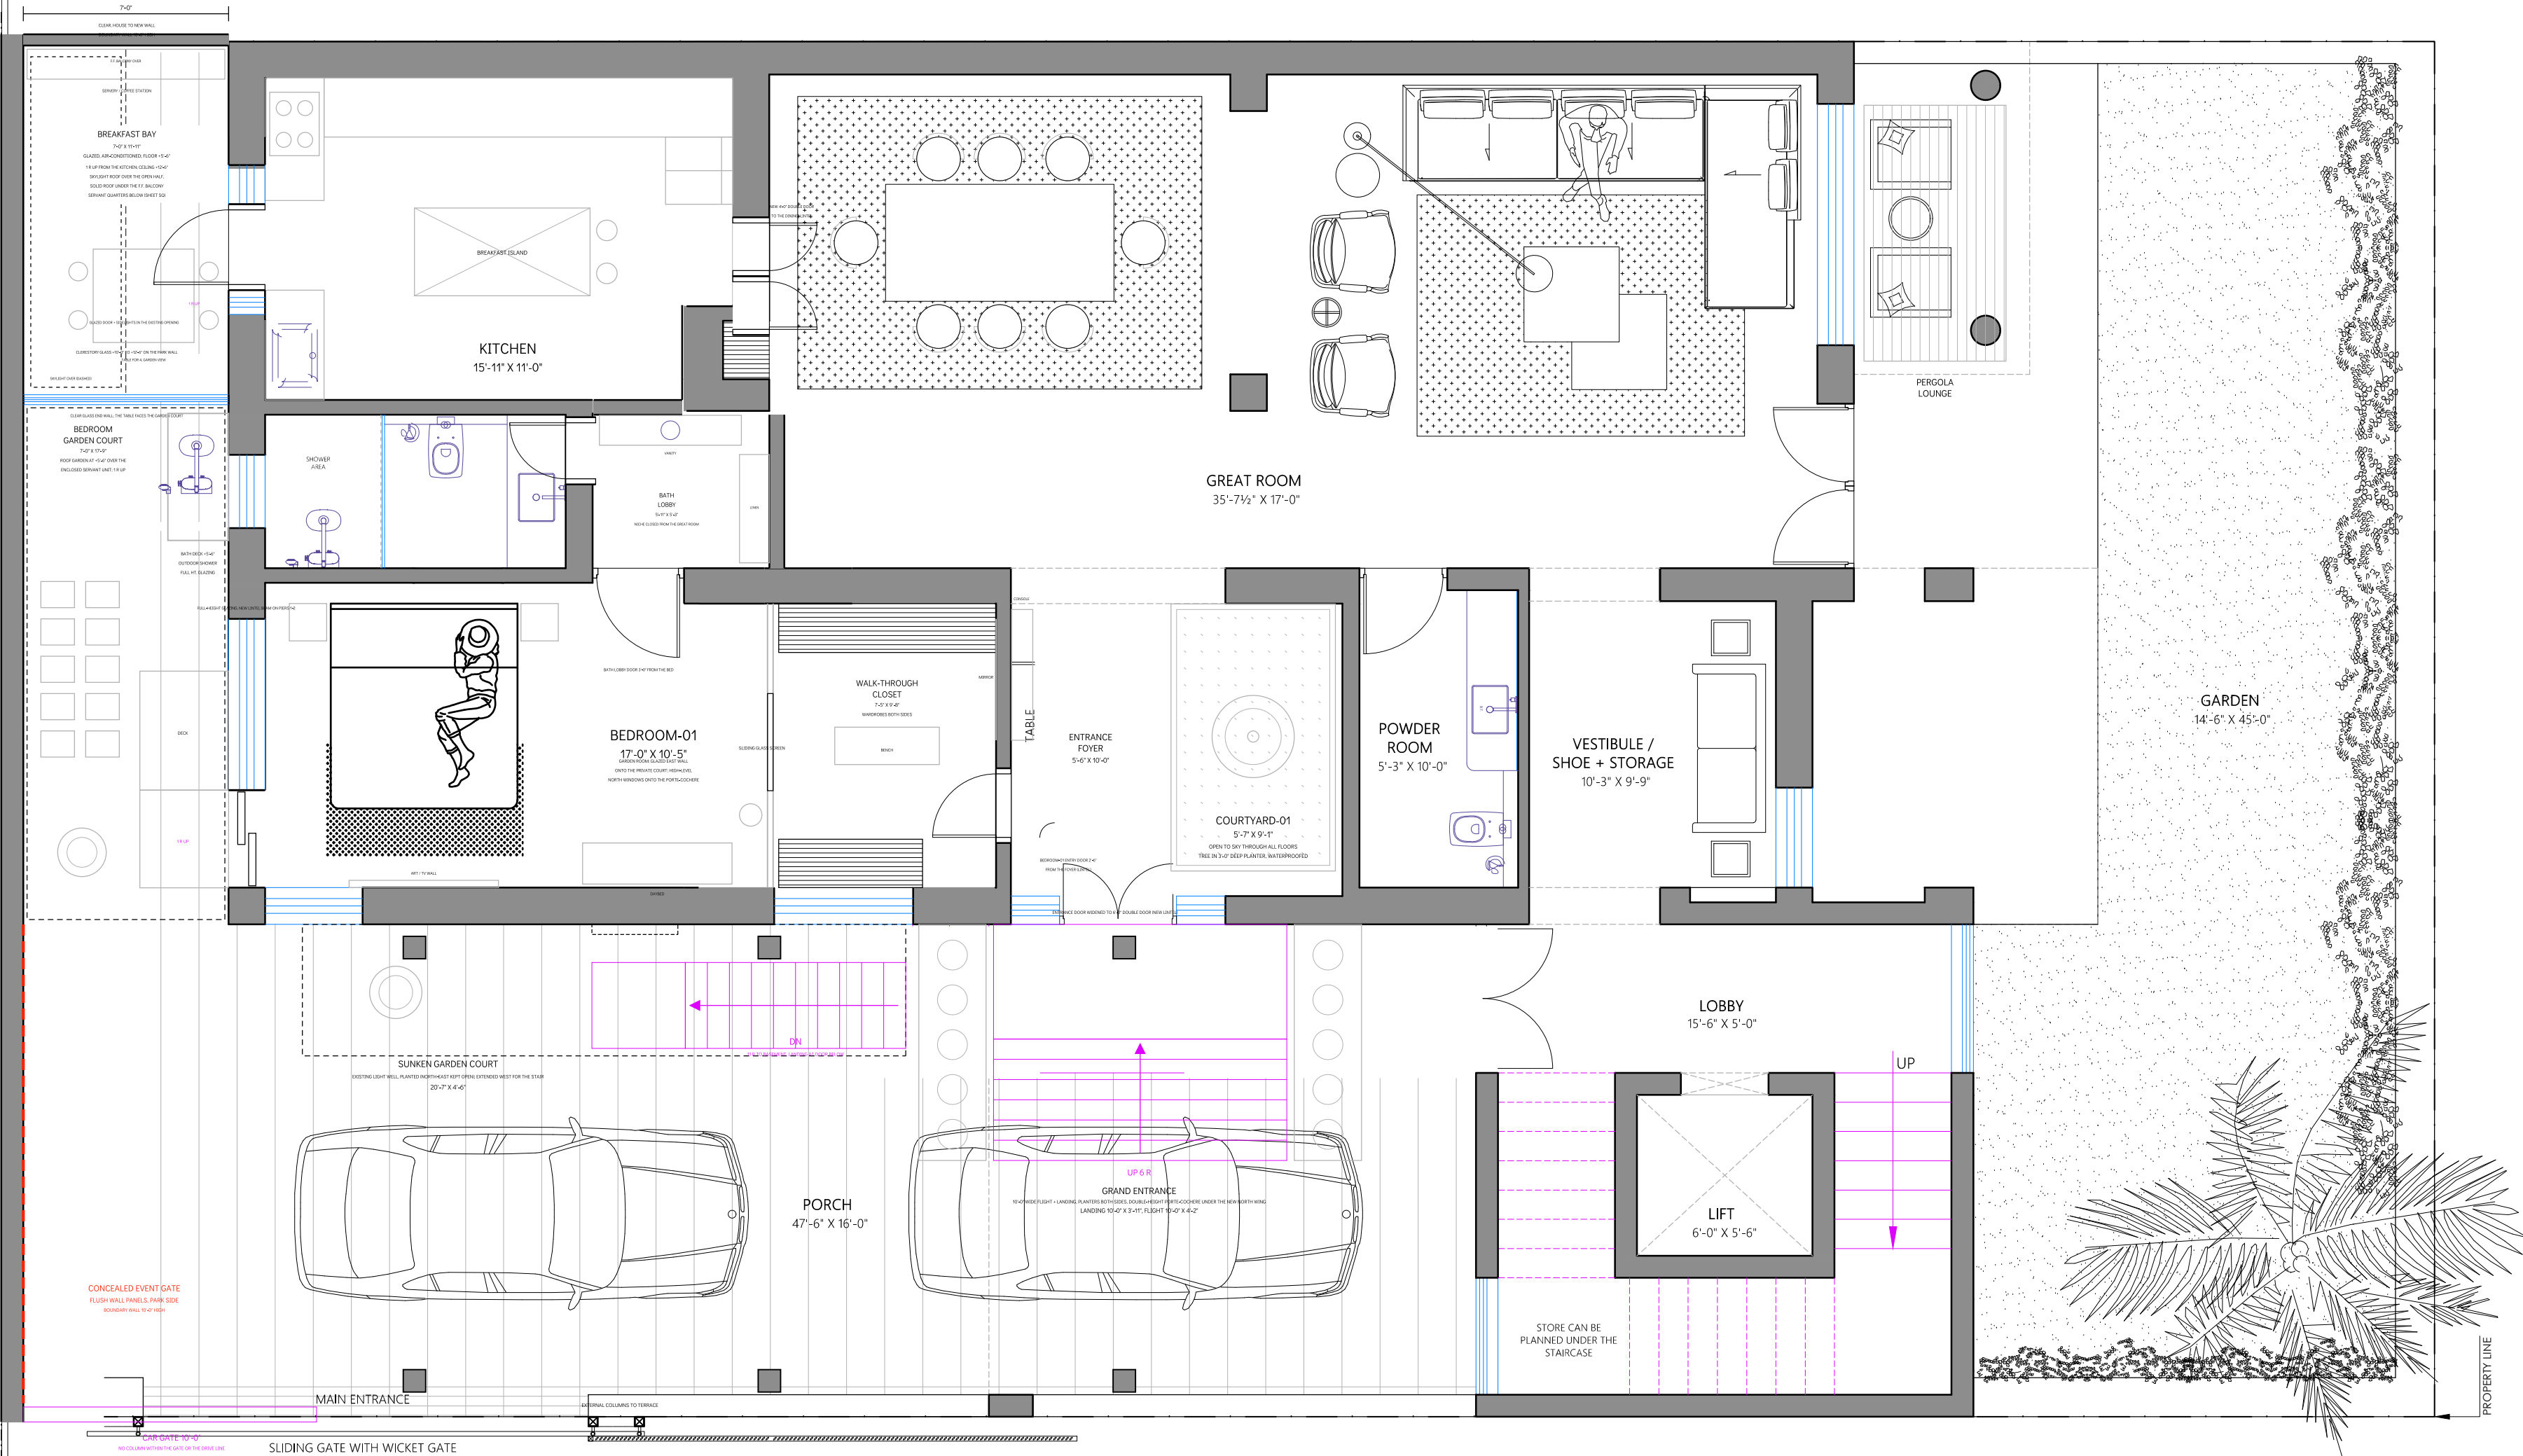

- NOTES:
1. Read this drawing along with relevant architectural, structural or service drawings.
 2. Do not scale; drawing should be read only.
 3. Any discrepancy to be brought to the notice of the architect before commencement of work.
 4. This drawing is a property of Ar. Akash Purohit and shall not be used or reproduced in any manner without the permission of the architects.

PROJECT:
17- CHANDRA PATH

SHEET TITLE:
**GROUND FLOOR -
RENOVATION LAYOUT**

DRAWING NO:
GF-PP-01


DEALT BY: KAPIL	CHECKED BY: AKASH
--------------------	----------------------

SCALE: N.T.S.	DATE: 15-09-2026
------------------	---------------------

FILE PATH:

studio sqft


AR. AKASH PUROHIT
ar.akashpurohit@gmail.com
9784784226

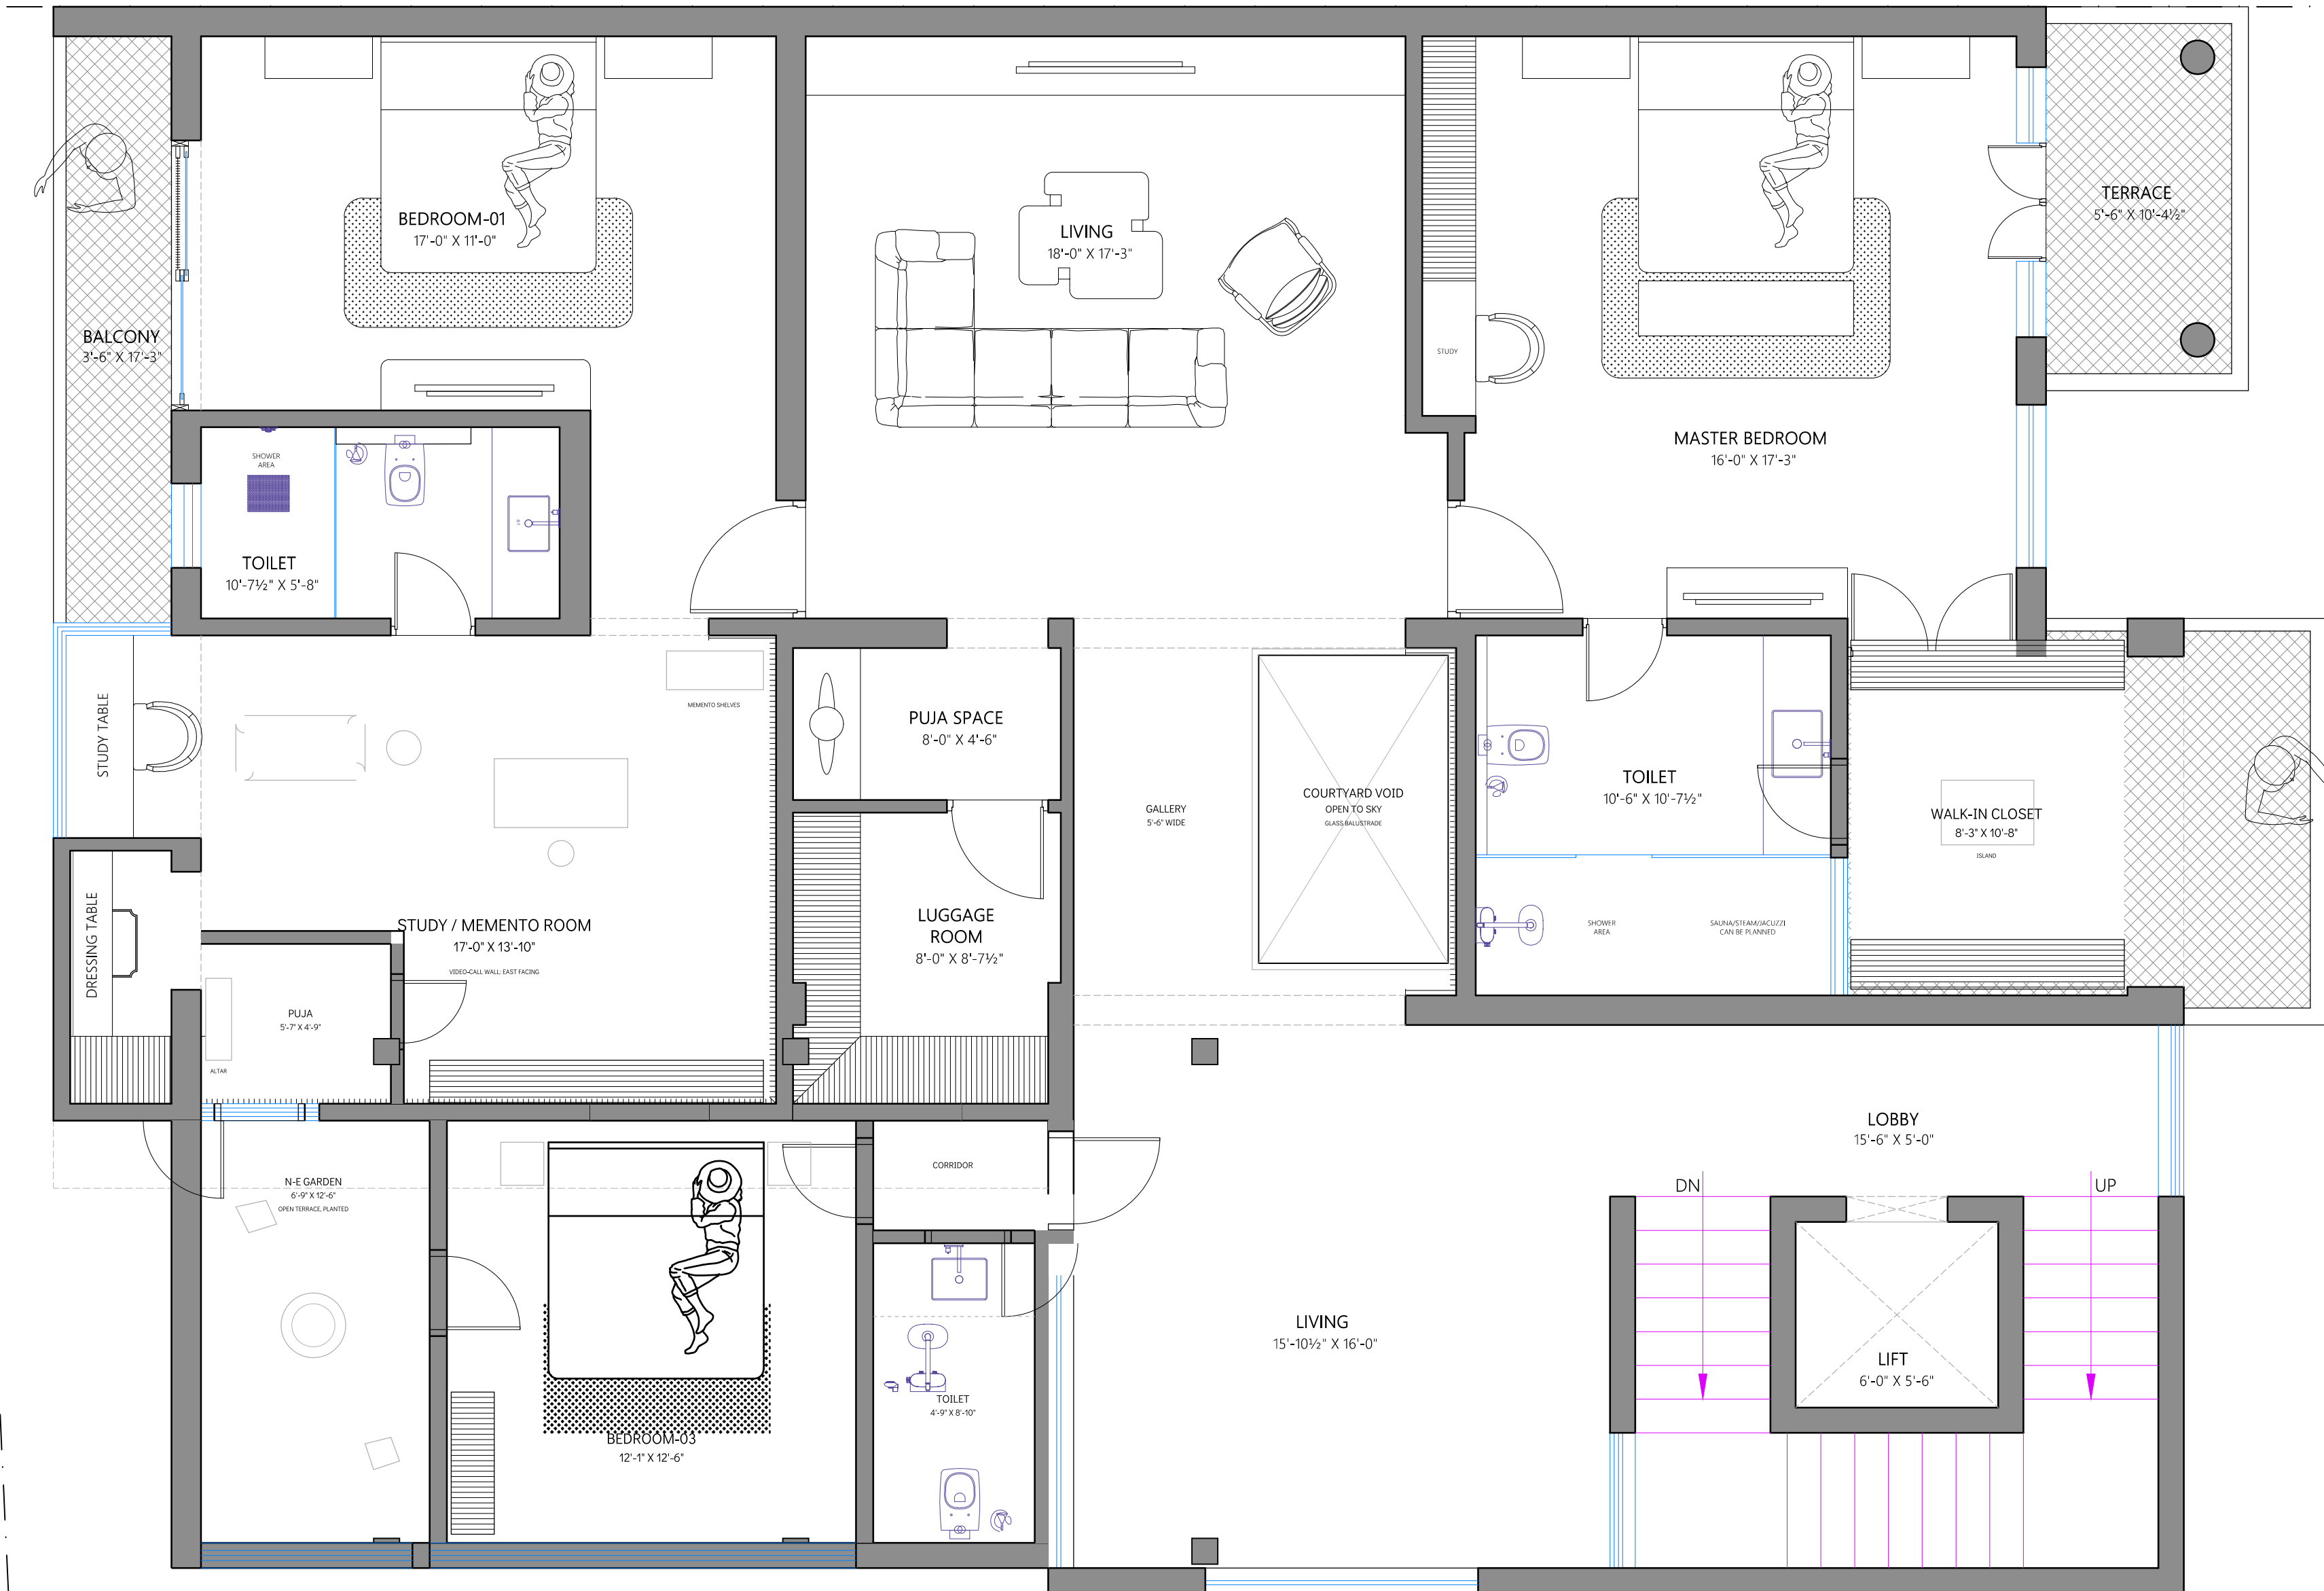

- NOTES:
1. Read this drawing along with relevant architectural, structural or service drawings.
 2. Do not scale; drawing should be read only.
 3. Any discrepancy to be brought to the notice of the architect before commencement of work.
 4. This drawing is a property of Ar. Akash Purohit and shall not be used or reproduced in any manner without the permission of the architects.

PROJECT:
17- CHANDRA PATH

SHEET TITLE:
**FIRST FLOOR -
RENOVATION LAYOUT**

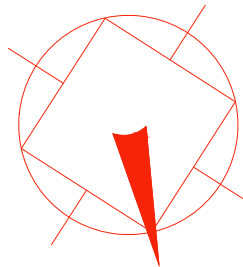

DRAWING NO:
FF-PP-01

DEALT BY:
KAPIL

CHECKED BY:
AKASH

SCALE:
N.T.S.


DATE:
15-09-2026

FILE PATH:

studio sqft

AR. AKASH PUROHIT
ar.akashpurohit@gmail.com
9784784226

NOTES (FIRST FLOOR, R3):
1. THE BLOCK OVER THE PORCH IS REBUILT FROM SCRATCH ON RCC COLUMNS FROM FOUNDATION TO TERRACE (THREE ON THE PORCH LINE, THREE AT THE BACK AGAINST THE NORTH WALL, NONE WITHIN THE 10'-0" CAR GATE OR THE DRIVE LINE), INDEPENDENT OF THE STONE WALLS; TO STRUCTURAL DESIGN.
2. FORMER WEST TERRACE ENCLOSED AS MASTER WALK-IN CLOSET (LIGHT PARTITIONS ON EXISTING SLAB); 3. NORTH-EAST ROOM RE-PURPOSED AS STUDY WITH PUJA IN ITS NORTH-EAST CORNER.
4. COURTYARD VOID WITHIN THE EXISTING STAIRWELL SHAFT; GLASS BALUSTRADE; 5. ROOM DIMENSIONS ARE CLEAR INTERNAL SIZES FROM THE DRAWN WALLS.

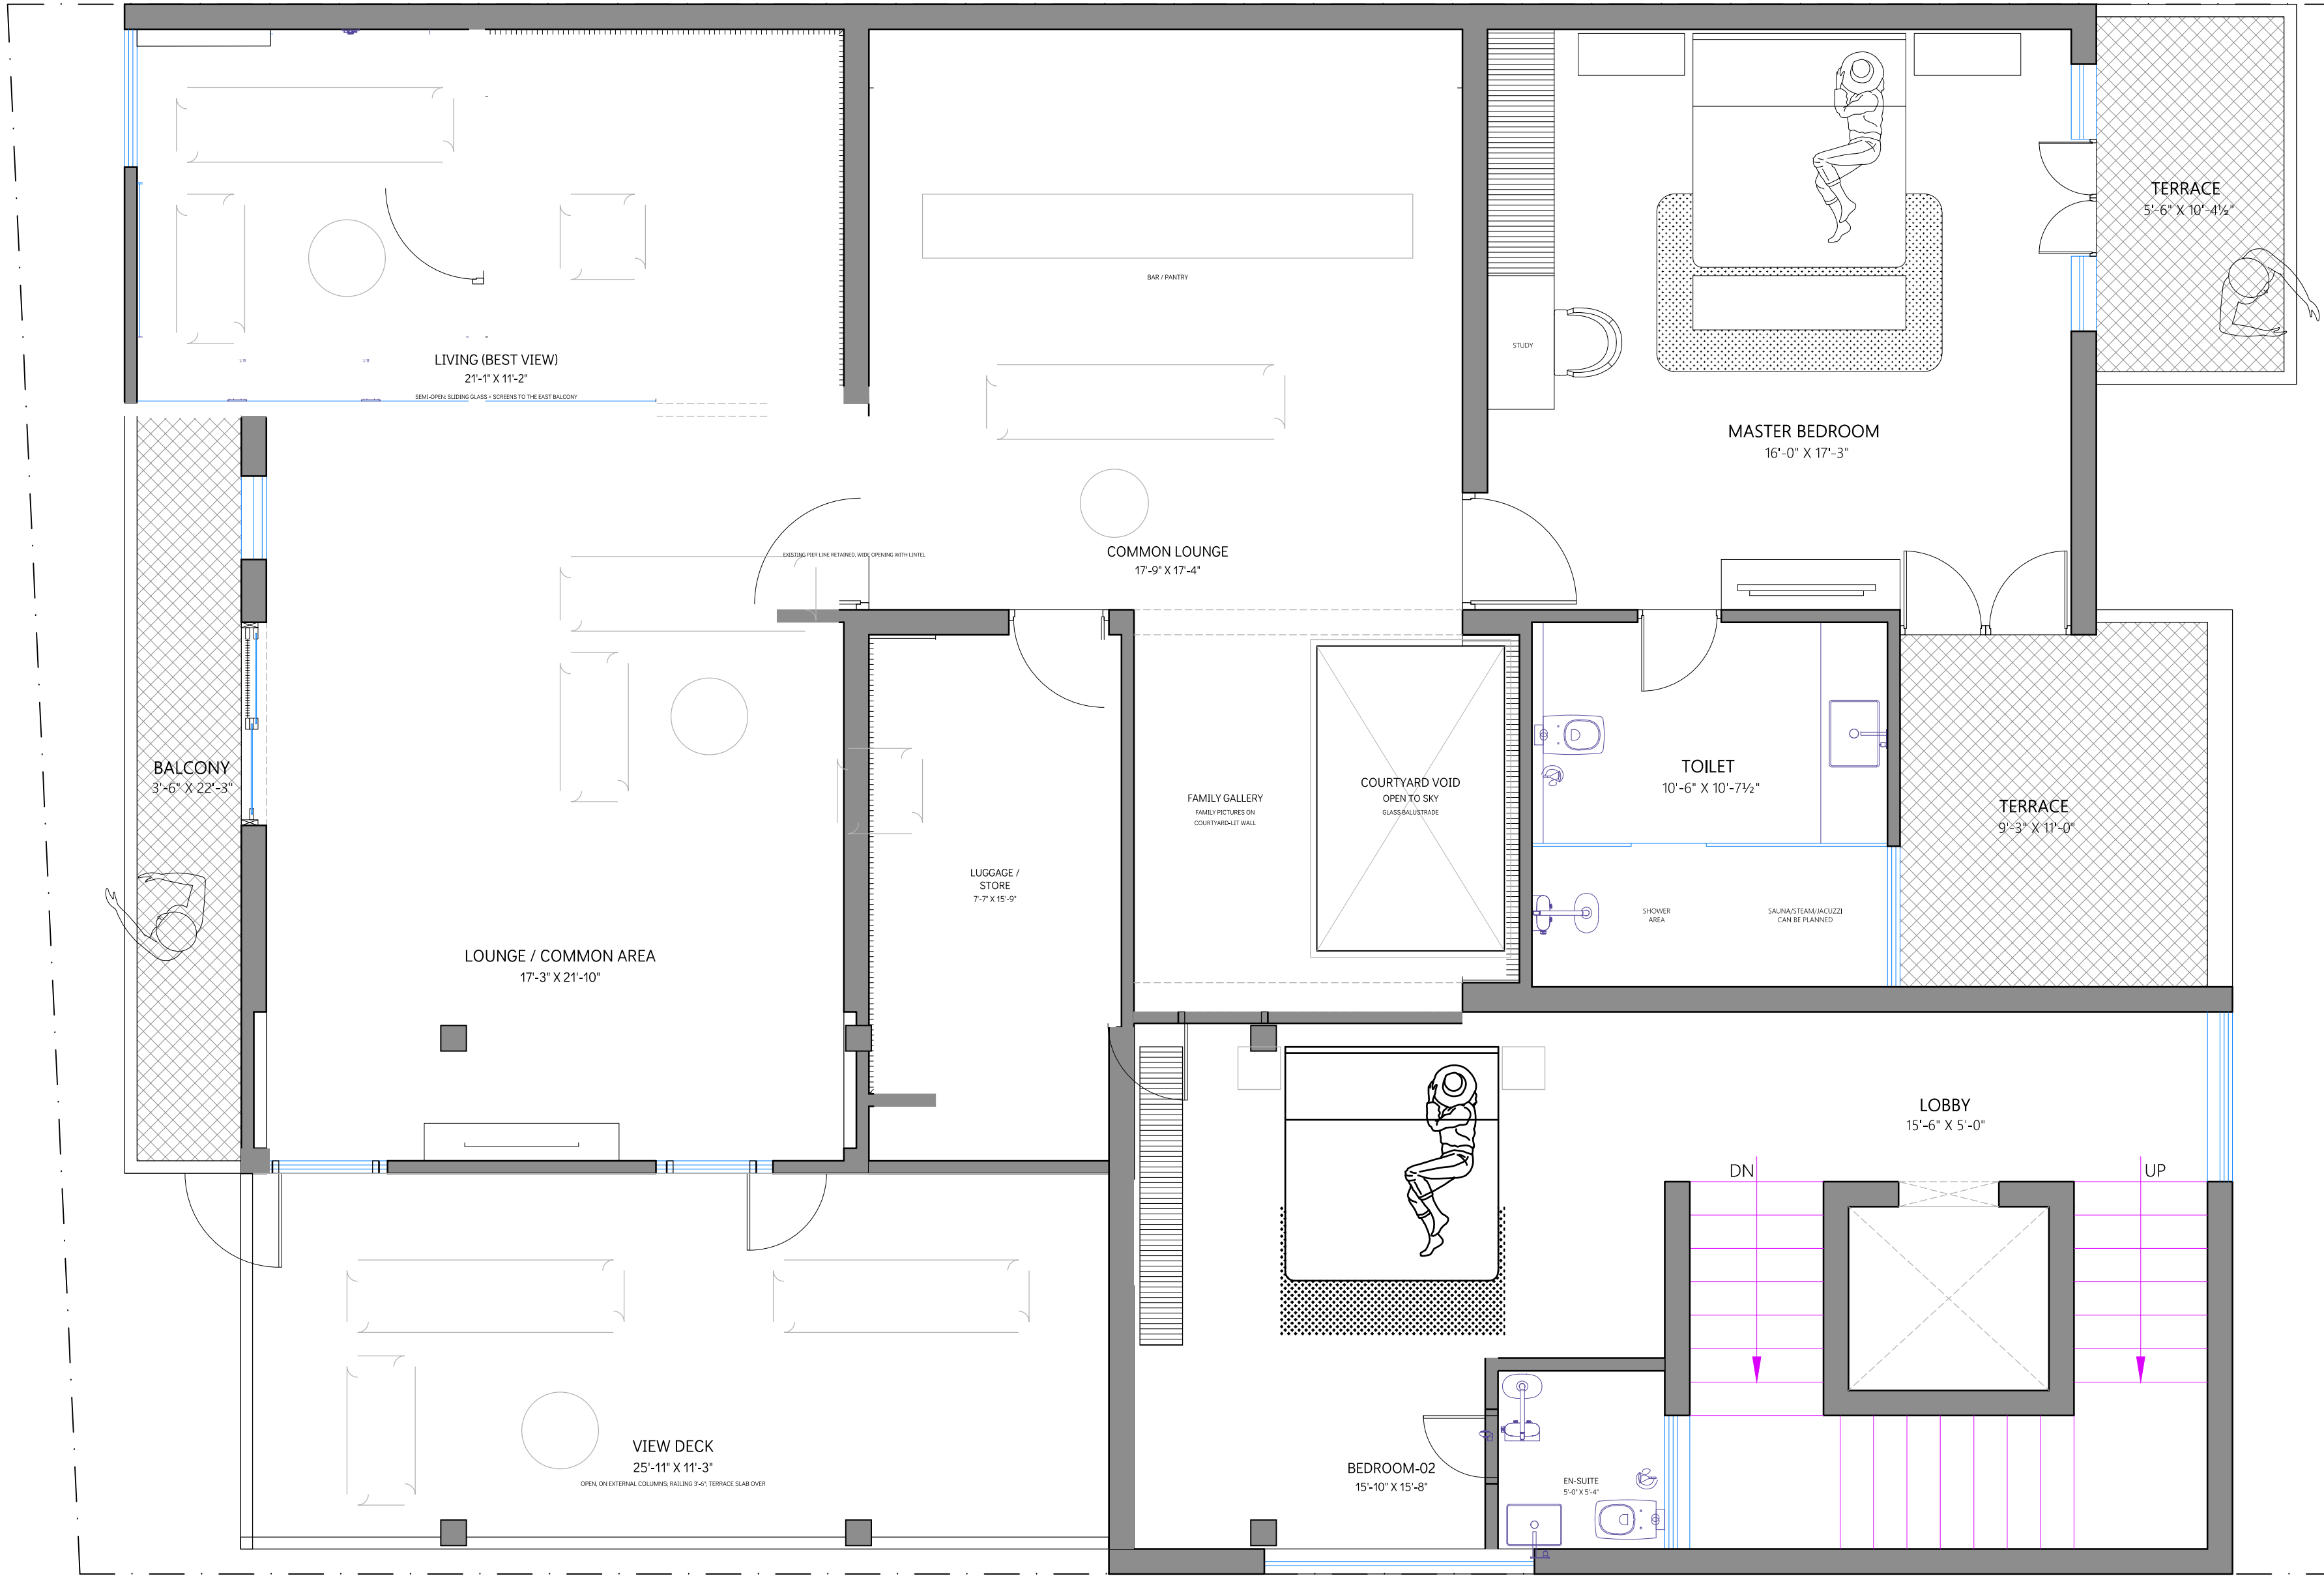


NOTES (SECOND FLOOR, R3):
1. SOUTH-EAST TOILET, WALK-IN CLOSET AND BEDROOM-02 REMOVED; THE SOUTH-EAST CORNER WITH THE BEST VIEW BECOMES THE LIVING ROOM, THE REST A COMMON LOUNGE. FORMER NORTH WINDOWS BECOME DOORS TO THE GARDEN AND BEDROOM-02, OR ARE INFILLED.
2. BEDROOM-02 WITH EN-SUITE IN THE FORMER LIVING OVER THE PORCH (NORTH-WEST); THE NEW EAST WING AT THIS LEVEL IS AN OPEN VIEW DECK ON EXTERNAL COLUMNS, NO WALLS. 3. STRUCTURAL WALL LINES RETAINED AS PIERS; OPENINGS WITH LINTELS.
4. FAMILY GALLERY ALONG THE COURTYARD VOID. 5. ROOM DIMENSIONS ARE CLEAR INTERNAL SIZES FROM THE DRAWN WALLS.

- NOTES:
1. Read this drawing along with relevant architectural, structural or service drawings.
 2. Do not scale; drawing should be read only.
 3. Any discrepancy to be brought to the notice of the architect before commencement of work.
 4. This drawing is a property of Ar. Akash Purohit and shall not be used or reproduced in any manner without the permission of the architects.

PROJECT:
17- CHANDRA PATH

SHEET TITLE:
SECOND FLOOR- LAYOUT

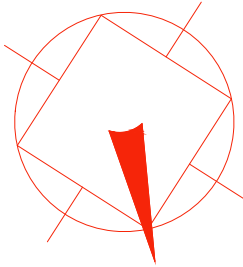

DRAWING NO:
SF-PP-01

DEALT BY:
KAPIL

CHECKED BY:
AKASH


SCALE:
N.T.S.

DATE:
15-09-2026

FILE PATH:

studio sqft

AR. AKASH PUROHIT
ar.akashpurohit@gmail.com
9784784226

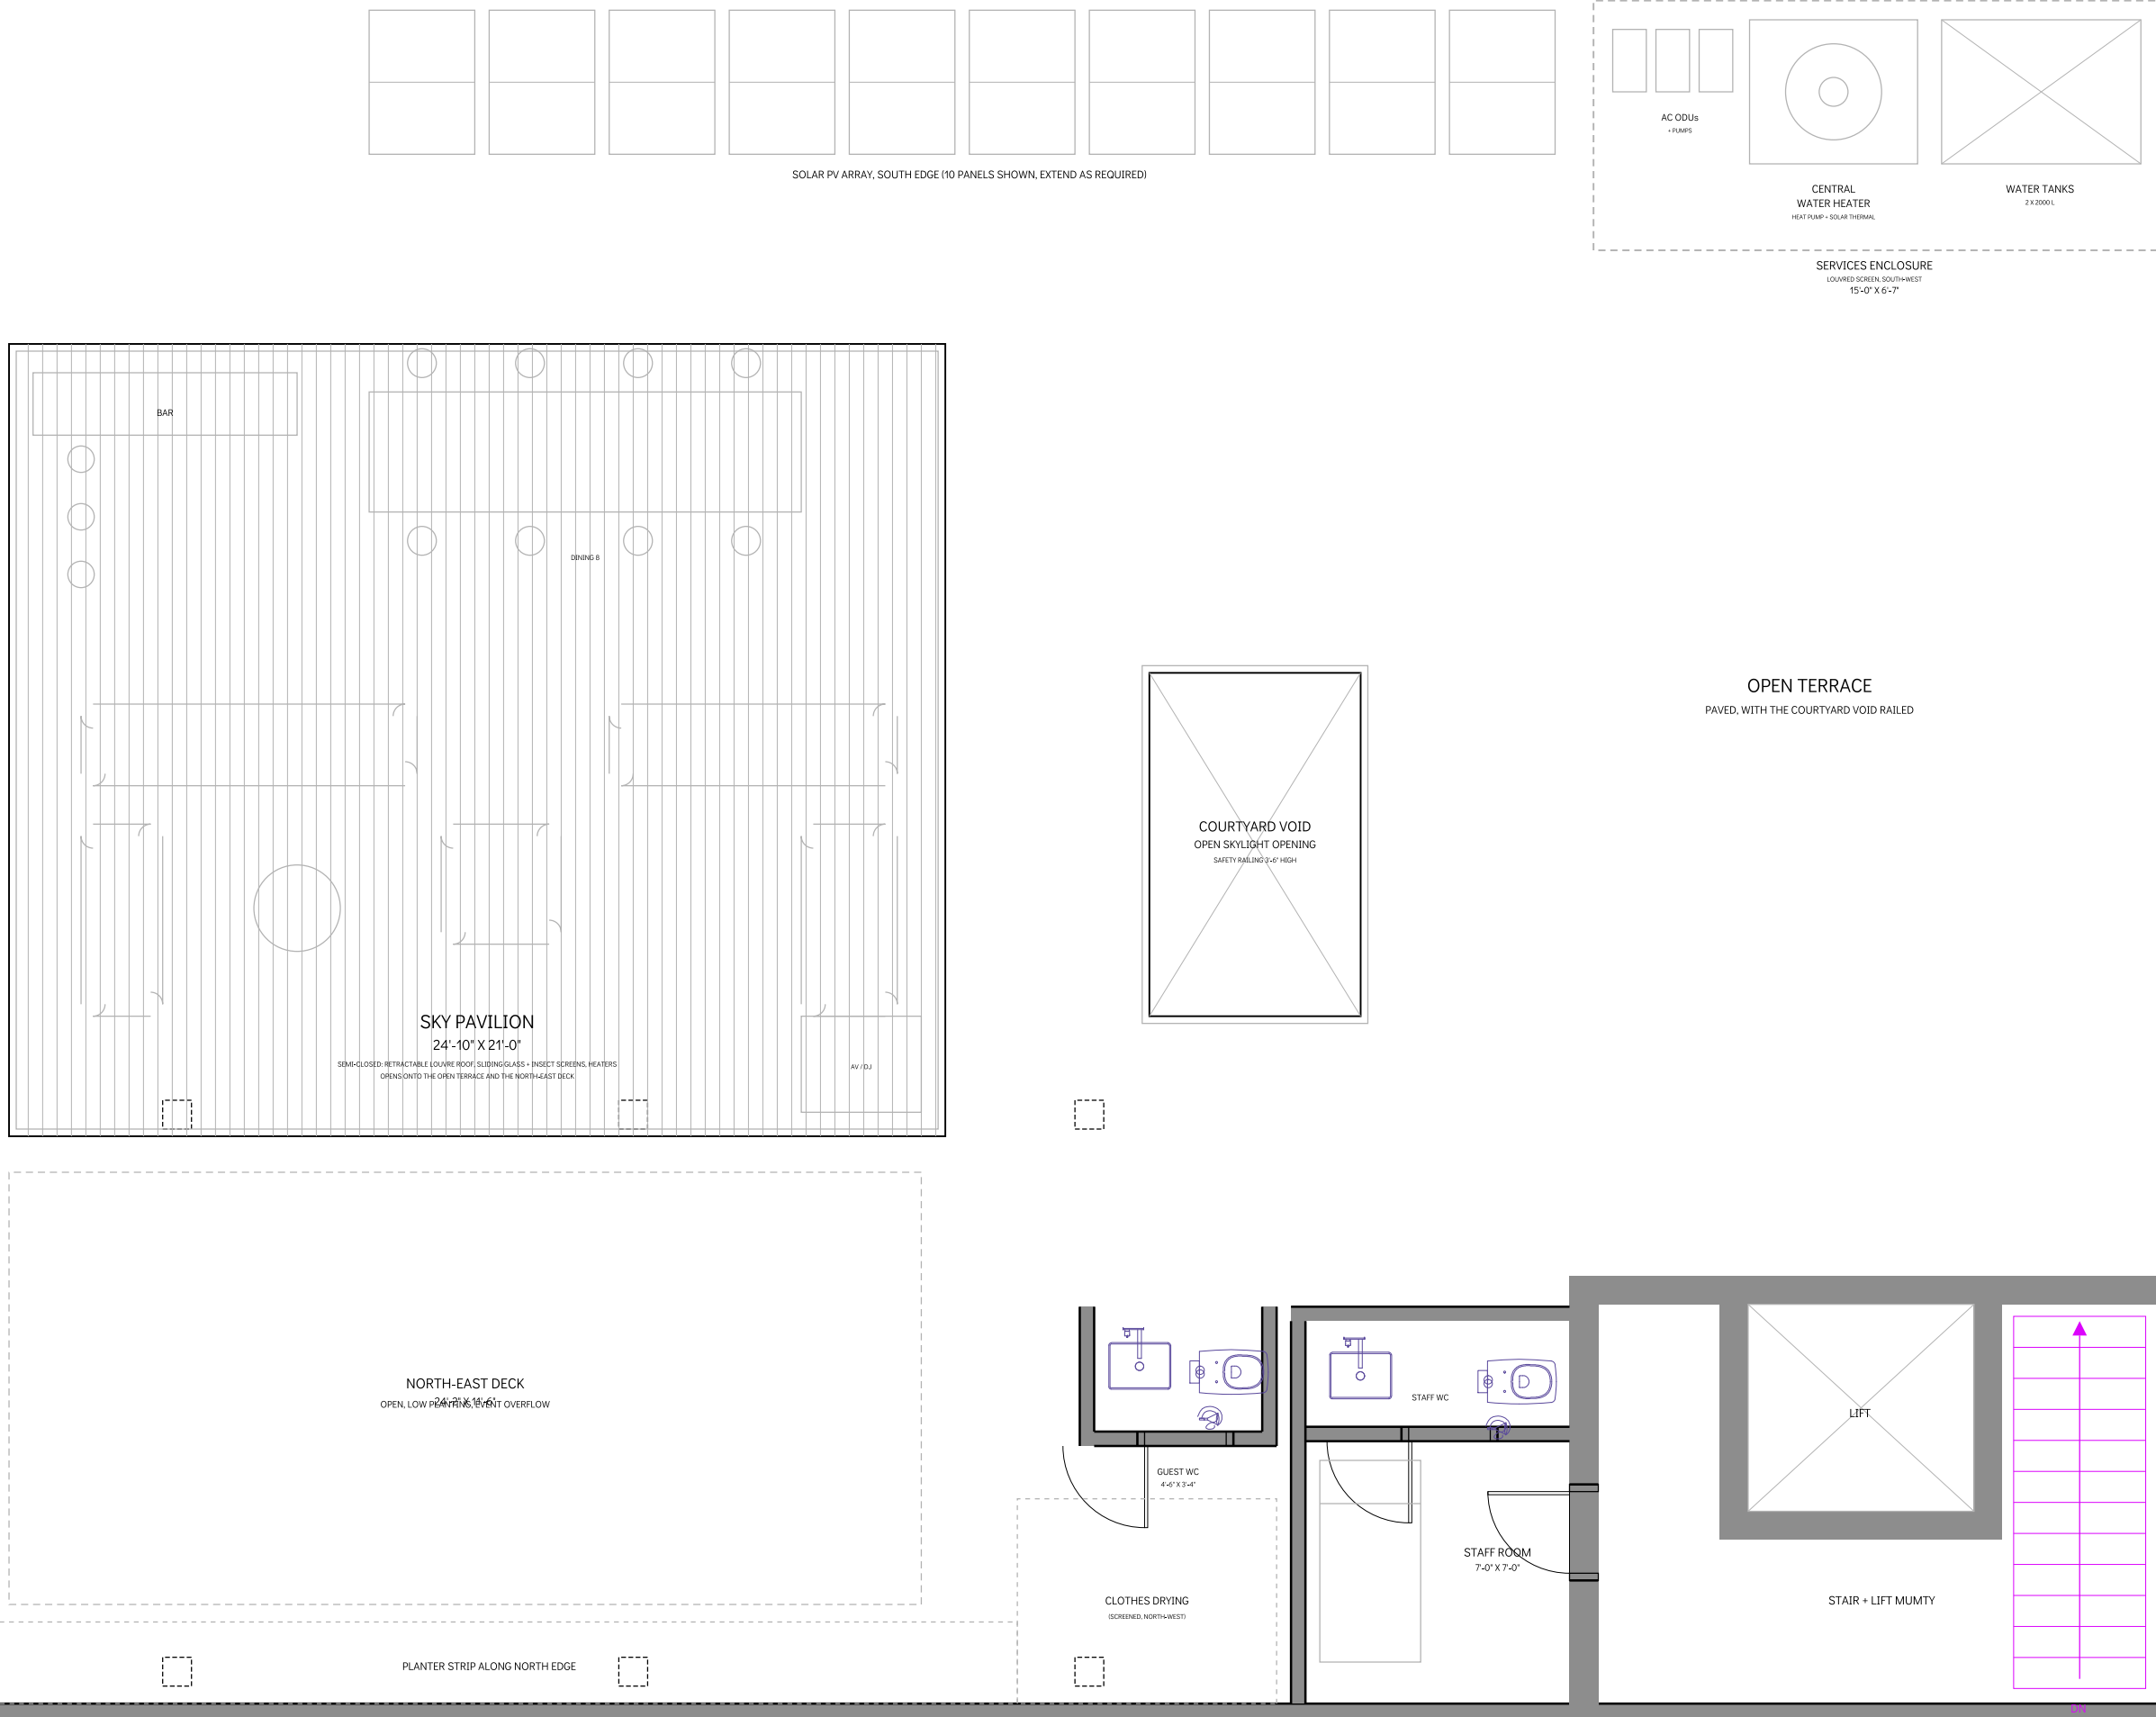

TERRACE FLOOR -
LAYOUT

TF-PP-01

NOTES (TERRACE, R5):
1. PARAPET 3'-6" HIGH ALL ROUND; COURTYARD VOID RAILED. 2. WATER TANKS, CENTRAL WATER HEATER, AC OUTDOOR UNITS AND PUMPS IN A LOUVRED SERVICES ENCLOSURE IN THE SOUTH-WEST; SOLAR PV ALONG THE SOUTH PARAPET; NORTH-EAST KEPT OPEN AND LOW (VASTUI).
3. SKY PAVILION ON THE EAST: STEEL FRAME, RETRACTABLE LOUVRE ROOF, SLIDING GLASS WITH INSECT SCREENS, BAR, DINING AND LOUNGE; POWER AND WATER TO THE BAR. 4. STAFF ROOM, WC, GUEST WC AND SCREENED DRYING YARD BESIDE THE MUMTY (NORTH-WEST).
5. TERRACE SLAB OVER THE NORTH WING CARRIED ON THE EXTERNAL COLUMNS (DASHED); PAVILION AND SERVICES LOADS TO BE CHECKED BY THE STRUCTURAL ENGINEER. 6. WATERPROOFING AND SLOPES TO NORTH-EAST DRAIN POINTS.