



BASEMENT -
RENOVATION LAYOUT

BF-PP-01

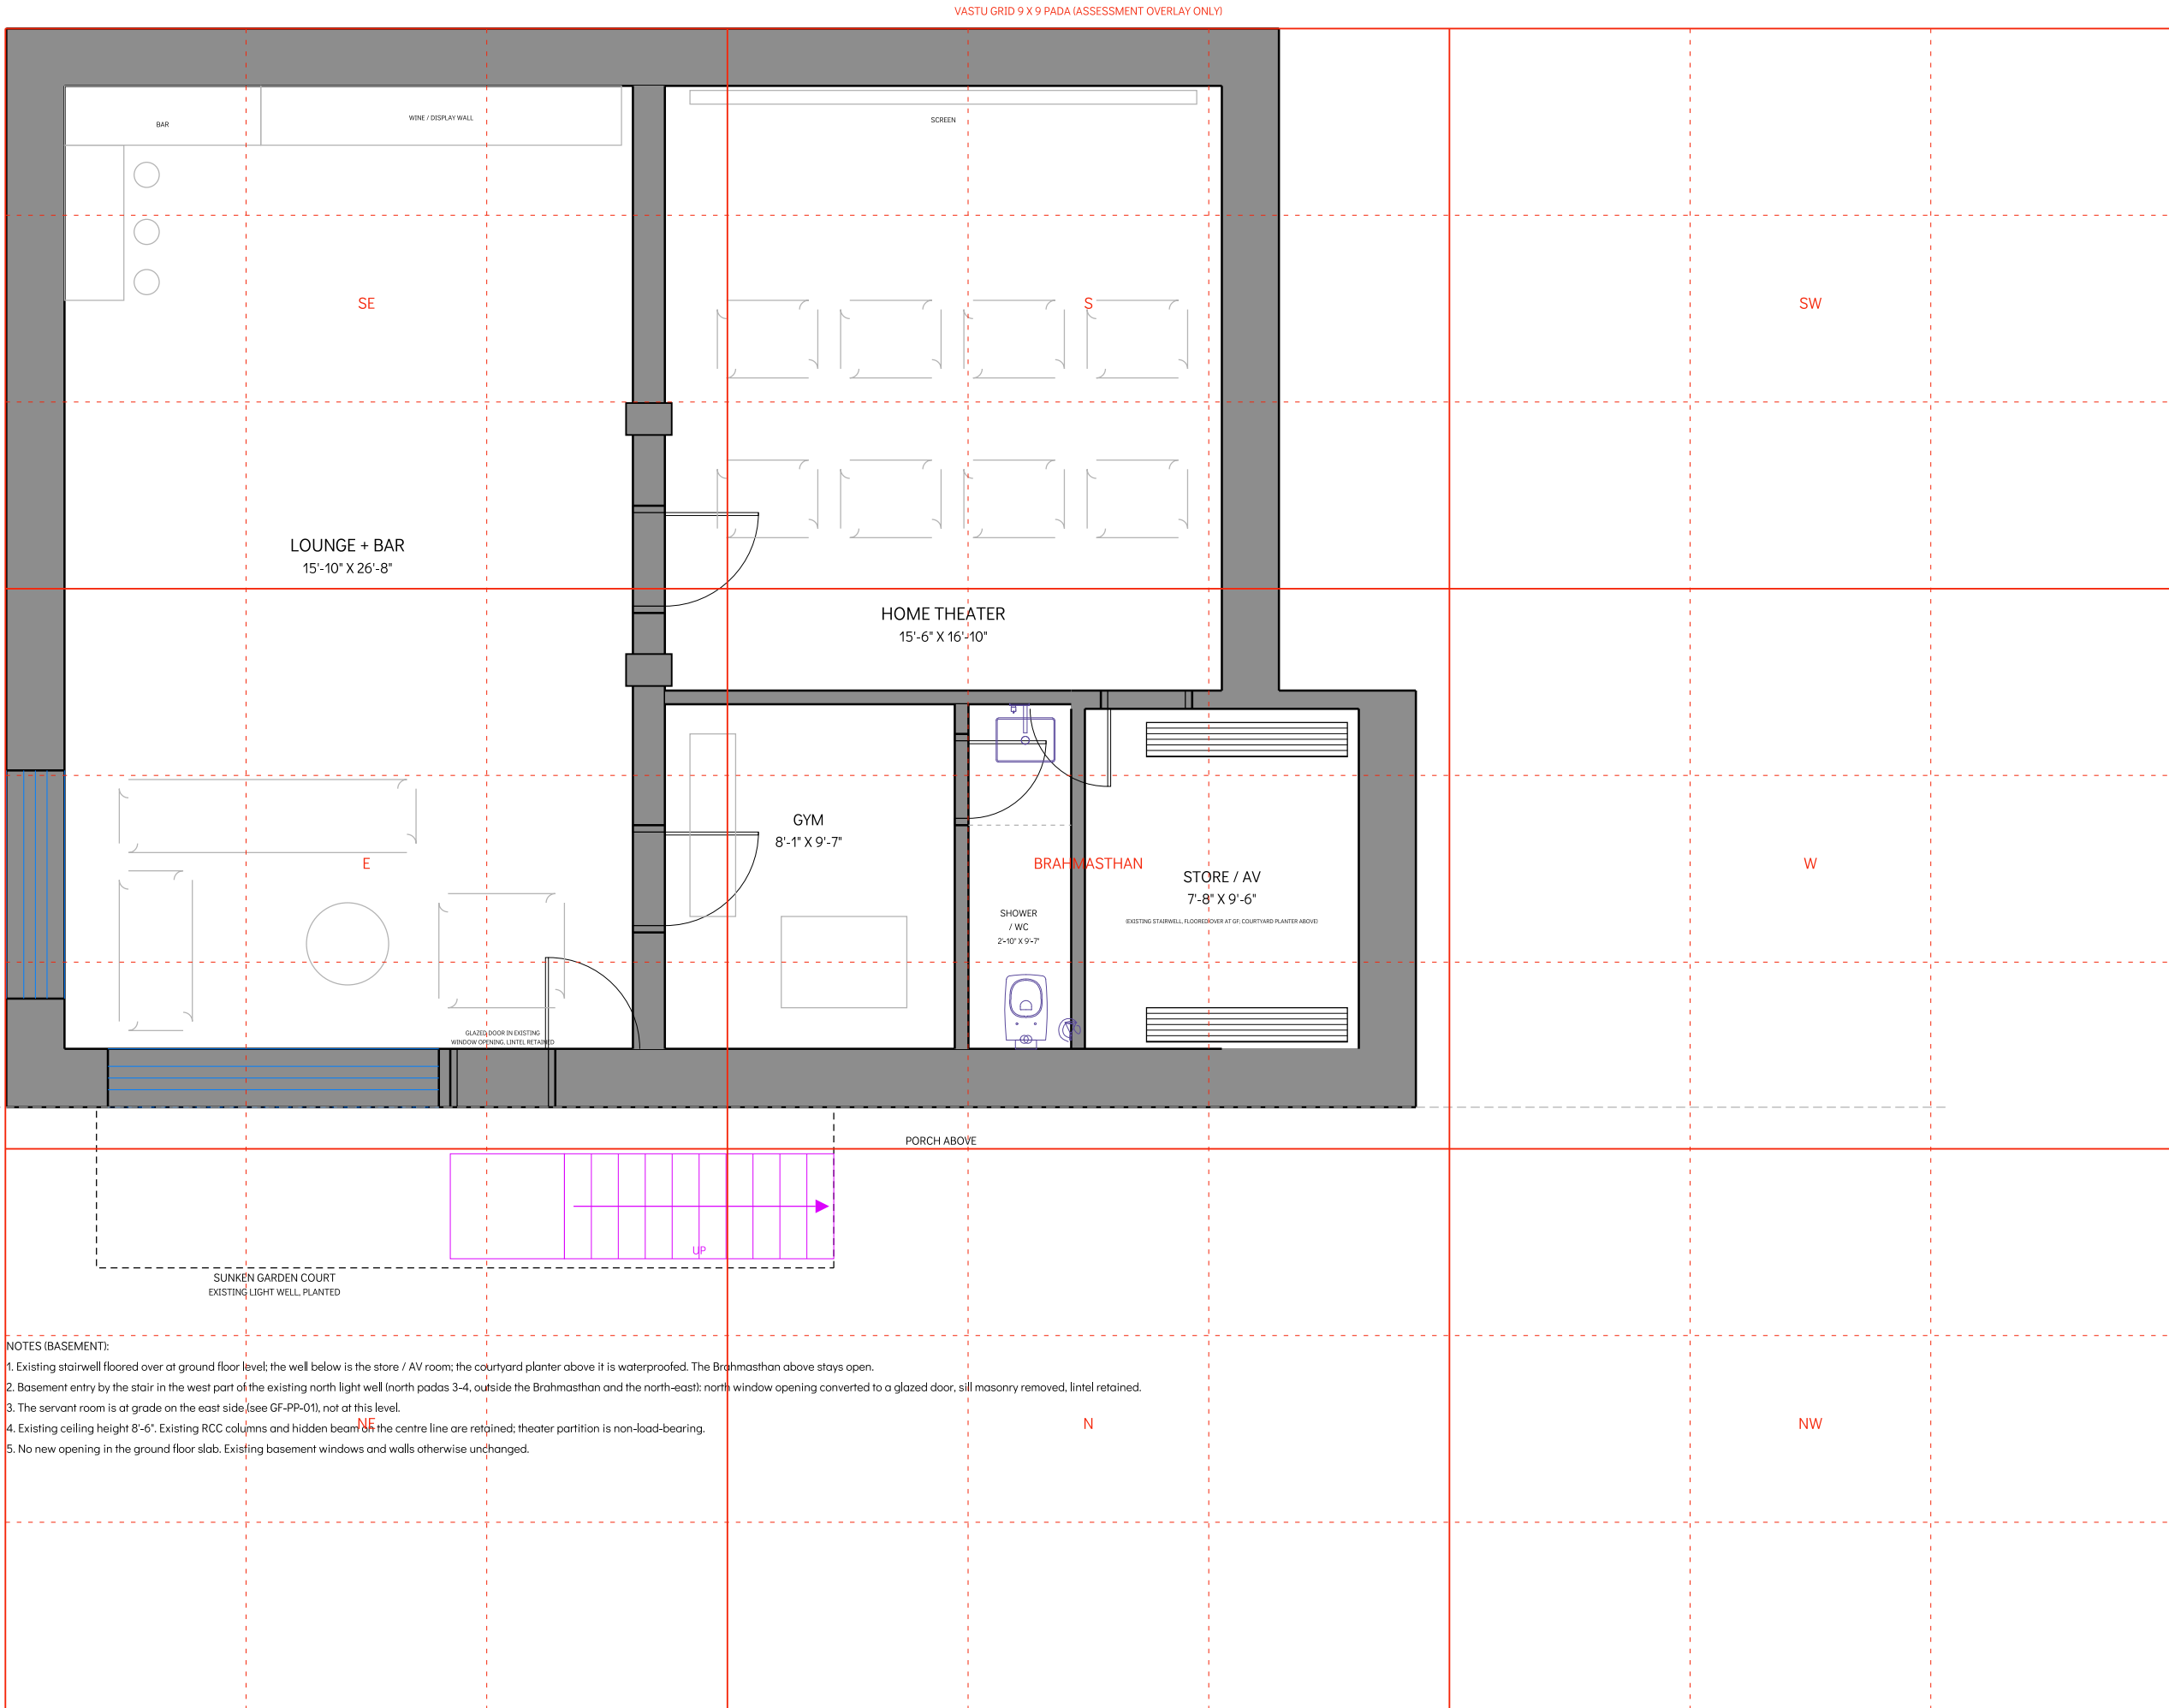


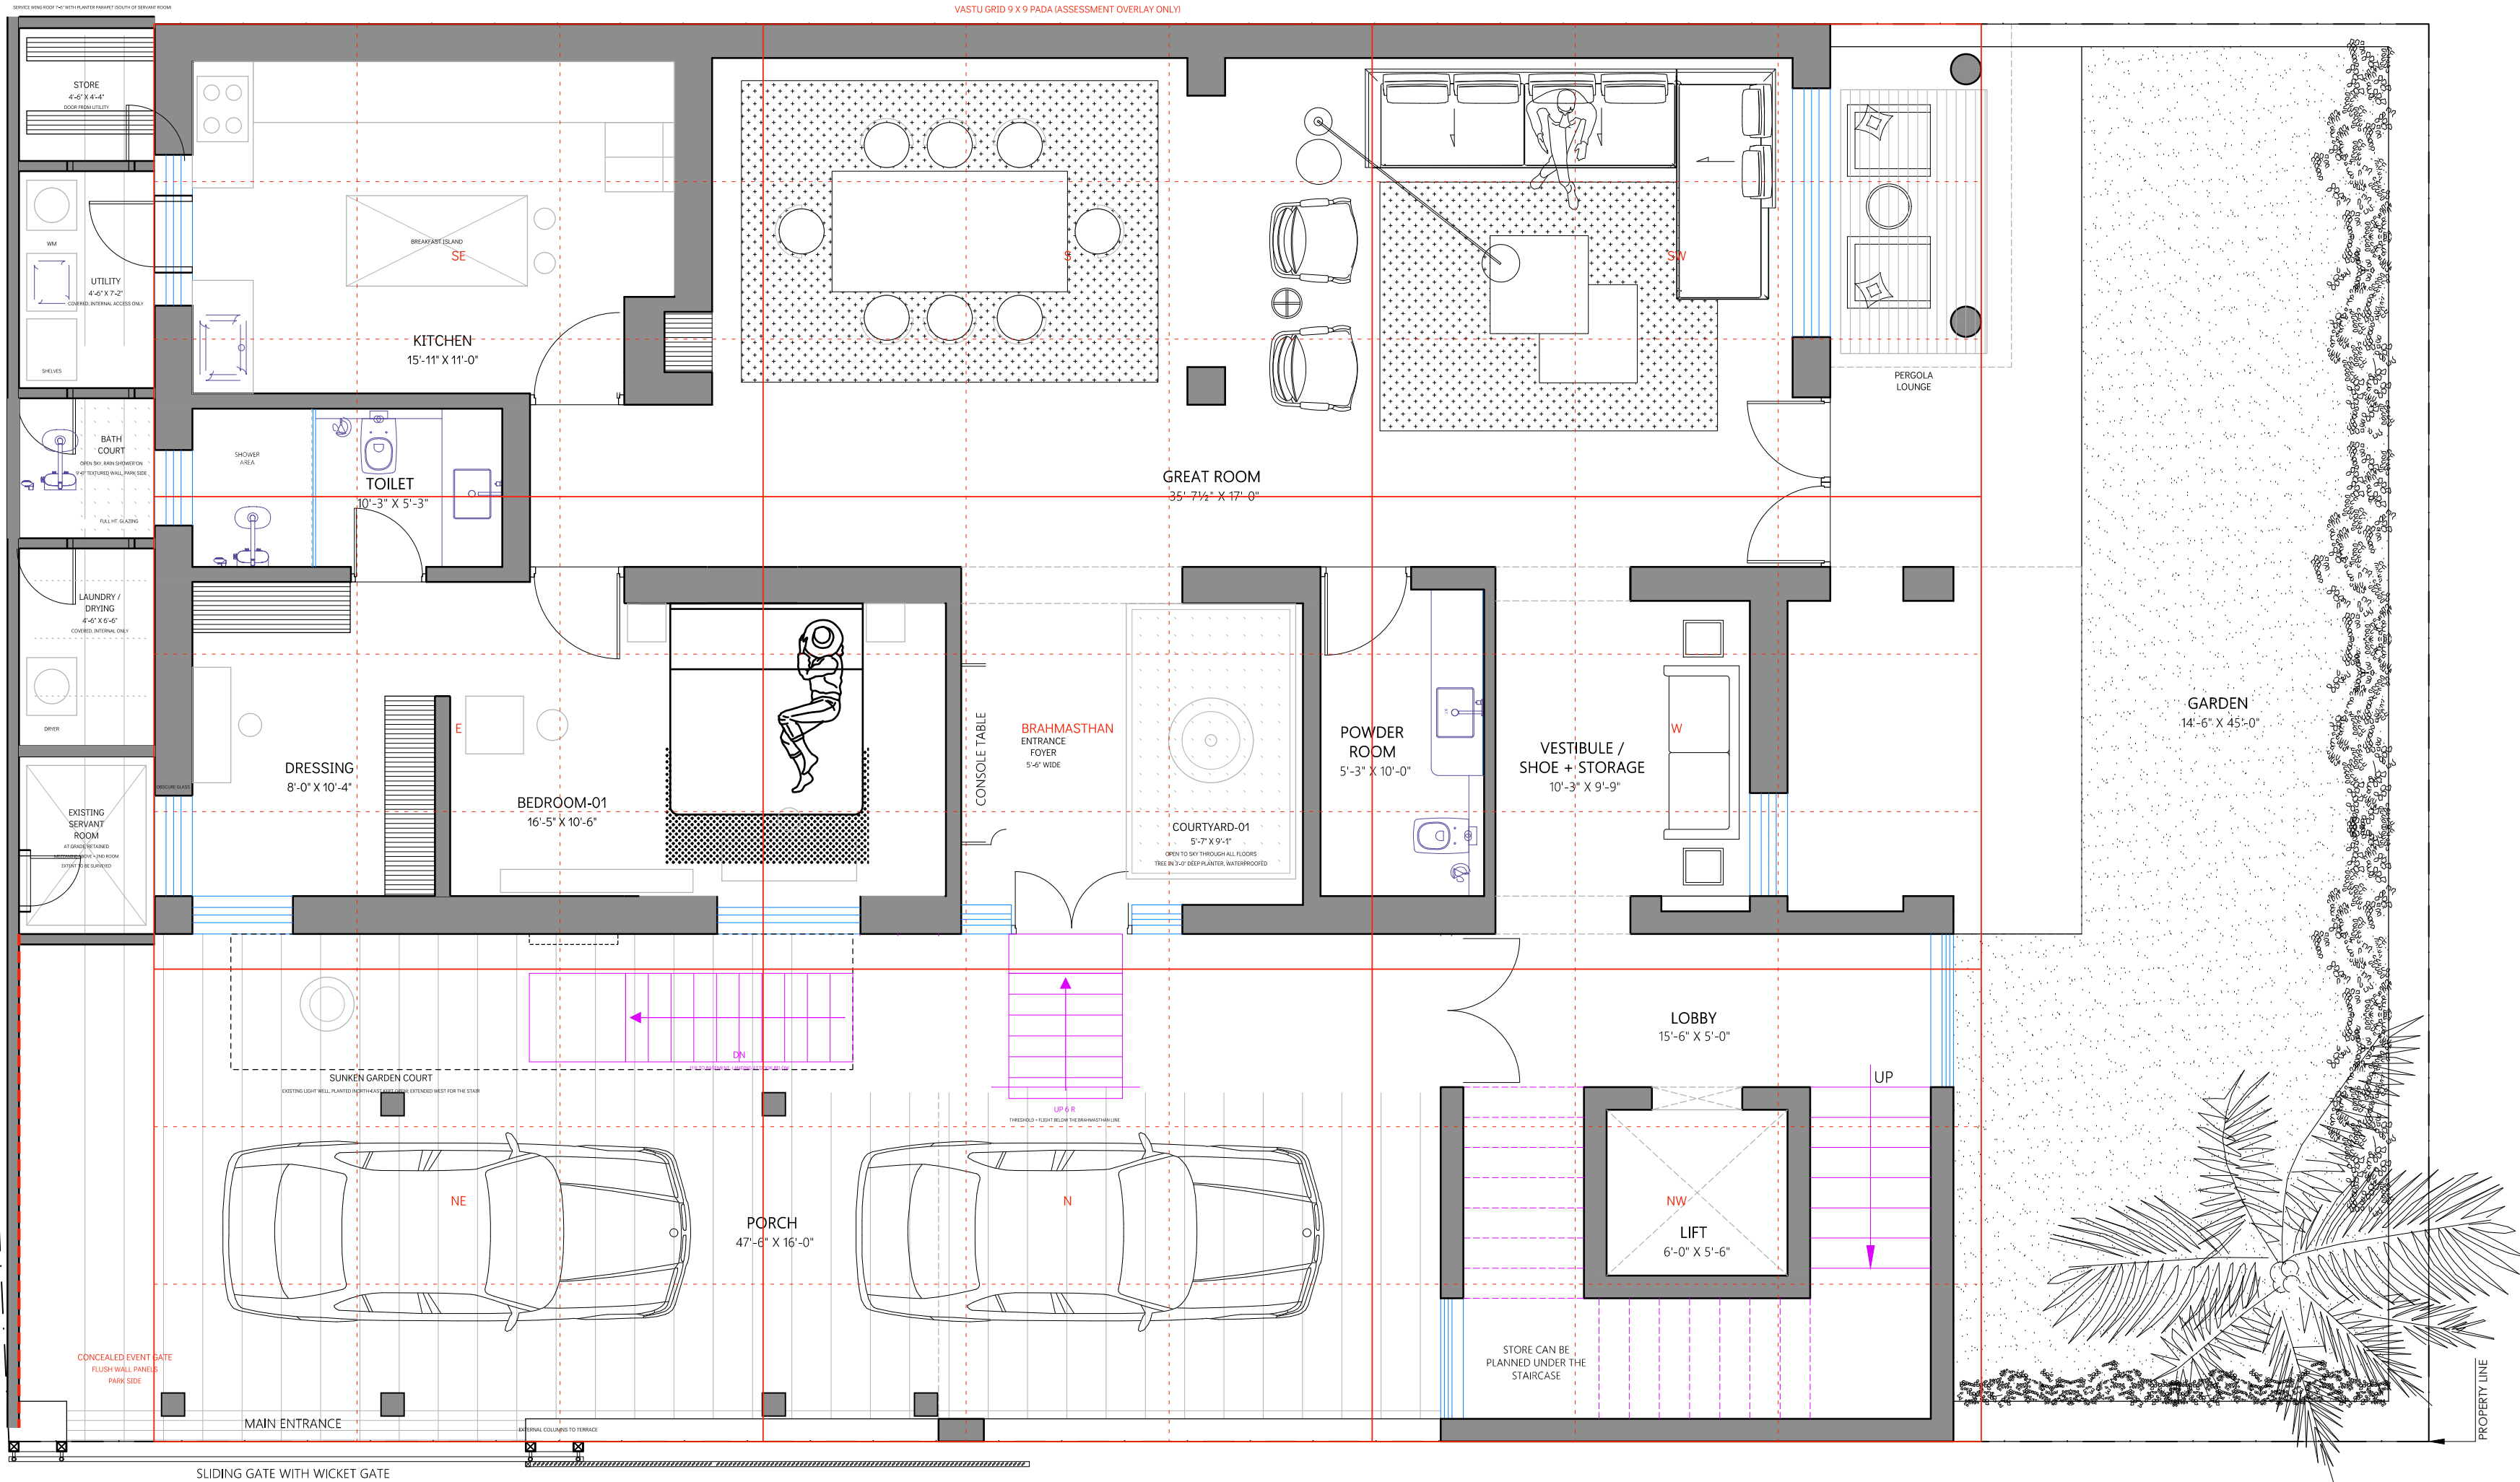

- NOTES:
1. Read this drawing along with relevant architectural, structural or service drawings.
 2. Do not scale; drawing should be read only.
 3. Any discrepancy to be brought to the notice of the architect before commencement of work.
 4. This drawing is a property of Ar. Akash Purohit and shall not be used or reproduced in any manner without the permission of the architects.

PROJECT:
17- CHANDRA PATH

SHEET TITLE:
**GROUND FLOOR -
RENOVATION LAYOUT**

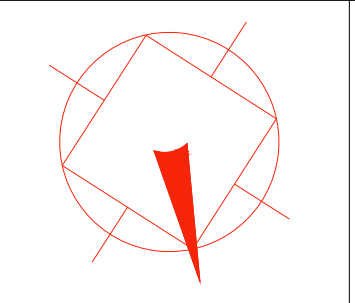

DRAWING NO:
GF-PP-01

DEALT BY: KAPIL	CHECKED BY: AKASH
--------------------	----------------------

SCALE: N.T.S.	DATE: 15-09-2026
------------------	---------------------

FILE PATH:

studio sqft


AR. AKASH PUROHIT
ar.akashpurohit@gmail.com
9784784226

NOTES (REVISION R3):
A. EAST BOUNDARY WALL REBUILT STRAIGHT AND PARALLEL TO THE HOUSE (DRAWN AT THE WIDEST EXISTING OFFSET, TO BE CONFIRMED BY SURVEY). NO OPENINGS TO THE PARK SIDE EXCEPT THE EVENT GATE.
B. CONCEALED EVENT GATE IN THE EAST BOUNDARY WALL FROM THE HOUSE CORNER TO THE FRONT BOUNDARY. FLUSH WALL-FINISHED PANELS ON CONCEALED PIVOTS, OPENED ONLY FOR EVENTS.
C. COURTYARD-01 IN THE EXISTING STAIRWELL SHAFT, OPEN TO SKY THROUGH ALL FLOORS. THE BRAHMASTHAN (CENTRE OF THE WHOLE-HOUSE GRID) IS KEPT OPEN AND FREE OF STAIRS. ENTRANCE STEPS ARE A COMPACT 6-RISER FLIGHT OUTSIDE THE EXISTING DOOR. BASEMENT STAIR IN THE WEST PART OF THE EXISTING LIGHT WELL. LIFT GIVES THE STEP-FREE ROUTE.
D. ENCLOSED SERVICE WING ALONG THE EAST SIDE AT GROUND FLOOR LEVEL ENTERED ONLY FROM THE KITCHEN. STORE DOOR FROM UTILITY. UTILITY, OPEN-SKY BATH COURT WITH THE OUTDOOR SHOWER AGAINST A 9'-0" TEXTURED WALL ON THE PARK SIDE. COVERED LAUNDRY. THE EXISTING SERVANT ROOM AT GRADE AT THE NORTH END IS RETAINED WITH ITS OWN ENTRY. THE SPACE ABOVE IT UP TO THE FIRST-FLOOR BAY BECOMES A MEZZANINE SECOND ROOM (LADDER STAIR INSIDE, HEADROOM TO BE VERIFIED).
E. SERVICE WING ROOFED AT 7'-6" WITH A PLANTER PARAPET. BATHROOM EAST WINDOW IN OBSCURE GLASS. VERANDAH REMOVED. PORCH PAVING PATTERN REMOVED. DRESSING EAST WINDOW IN OBSCURE GLASS (SERVANT ROOM OUTSIDE). LONG-TERM STAFF ROOM ON THE TERRACE (TF-PP-01). SINCE A SERVANT ROOM IN THE NORTH-EAST IS A VASTU COMPROMISE.
F. VASTU GRID (RED) COVERS THE WHOLE BUILT HOUSE INCLUDING THE PORCH LEVEL UNDER THE UPPER FLOORS; ASSESSMENT OVERLAY ONLY. SHEET ORIENTATION: TOP = SOUTH, BOTTOM = NORTH, LEFT = EAST, RIGHT = WEST.

- NOTES:
1. Read this drawing along with relevant architectural, structural or service drawings.
 2. Do not scale; drawing should be read only.
 3. Any discrepancy to be brought to the notice of the architect before commencement of work.
 4. This drawing is a property of Ar. Akash Purohit and shall not be used or reproduced in any manner without the permission of the architects.

PROJECT:
17- CHANDRA PATH


SHEET TITLE:
**FIRST FLOOR -
RENOVATION LAYOUT**

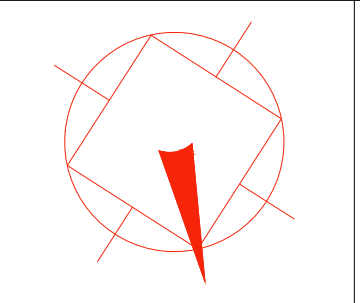


DRAWING NO: FF-PP-01	
DEALT BY: KAPIL	CHECKED BY: AKASH
SCALE: N.T.S.	DATE: 15-09-2026
FILE PATH:	

studio sqft

AR. AKASH PUROHIT
ar.akashpurohit@gmail.com
9784784226

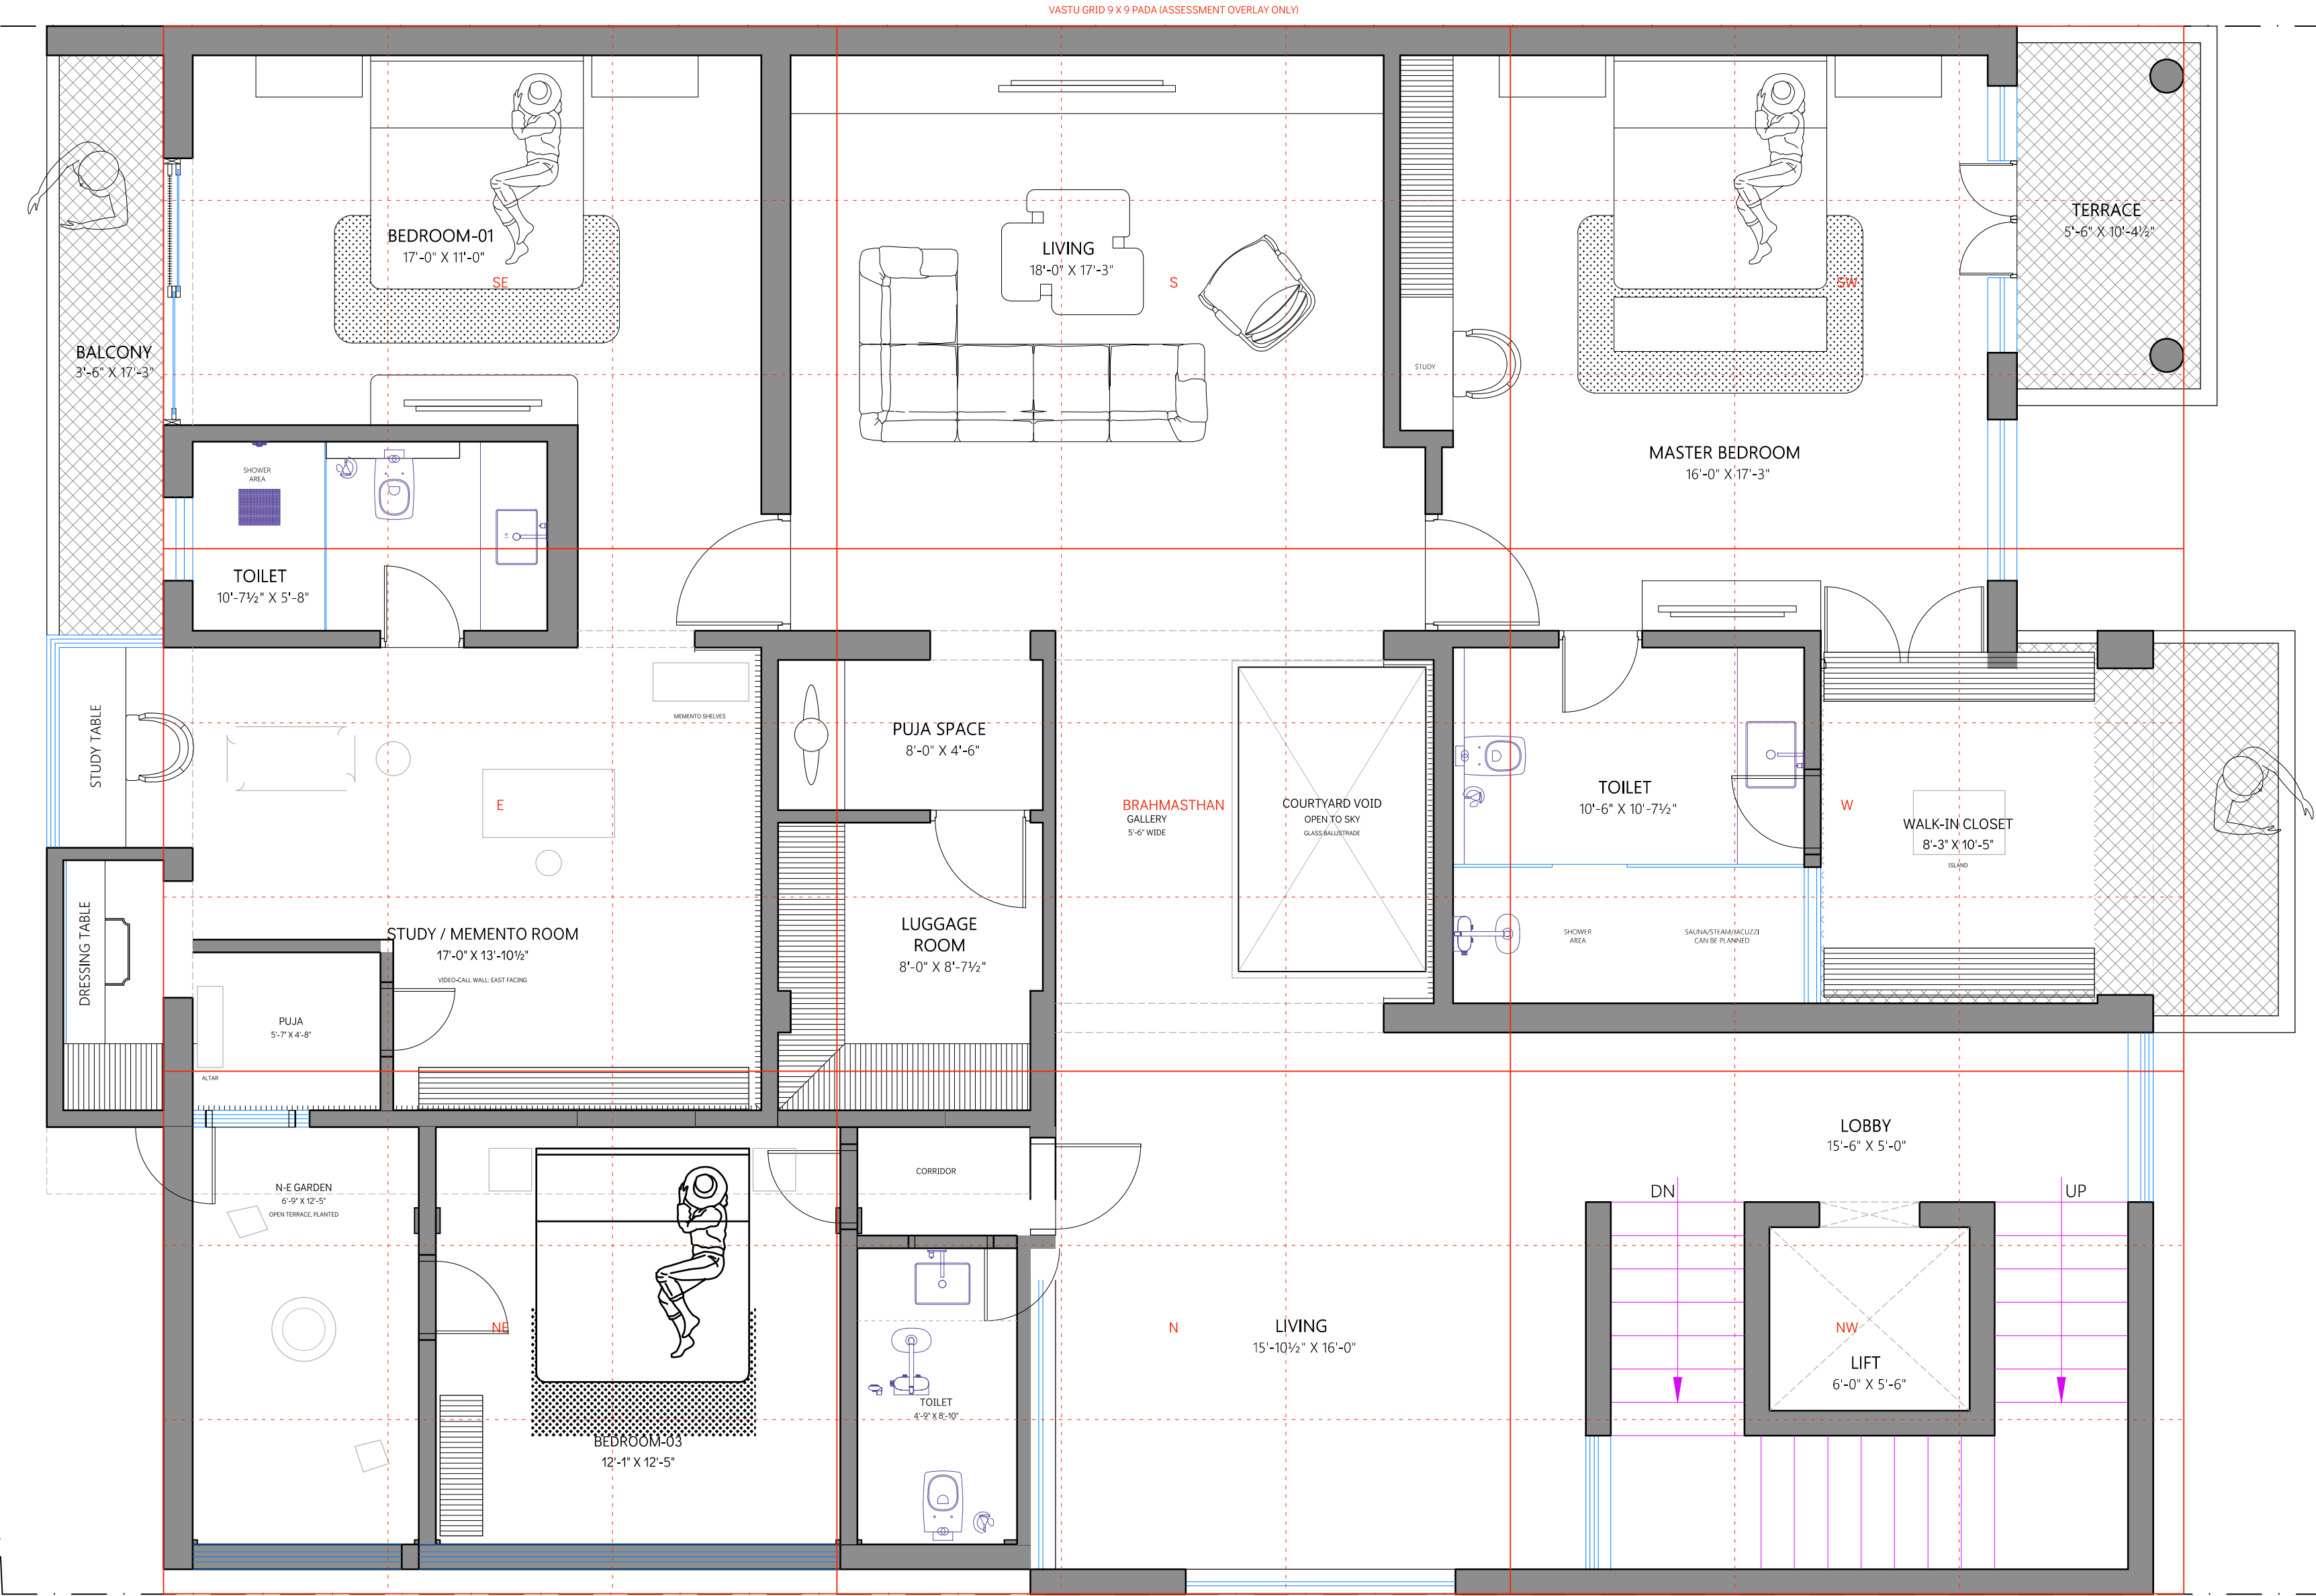


NOTES (FIRST FLOOR, R3):
1. NEW SLABS OVER THE PORCH CARRIED ON EXTERNAL RCC COLUMNS FROM FOUNDATION TO TERRACE (FOUR ON THE PORCH LINE, TWO AT THE BACK AGAINST THE NORTH WALL), INDEPENDENT OF THE STONE WALLS; TO STRUCTURAL DESIGN.
2. FORMER WEST TERRACE ENCLOSED AS MASTER WALK-IN CLOSET (LIGHT PARTITIONS ON EXISTING SLAB). 3. NORTH-EAST ROOM RE-PURPOSED AS STUDY WITH PUJA IN ITS NORTH-EAST CORNER.
4. COURTYARD VOID WITHIN THE EXISTING STAIRWELL SHAFT; GLASS BALUSTRADE. 5. VASTU GRID (RED) IS AN ASSESSMENT OVERLAY ONLY.

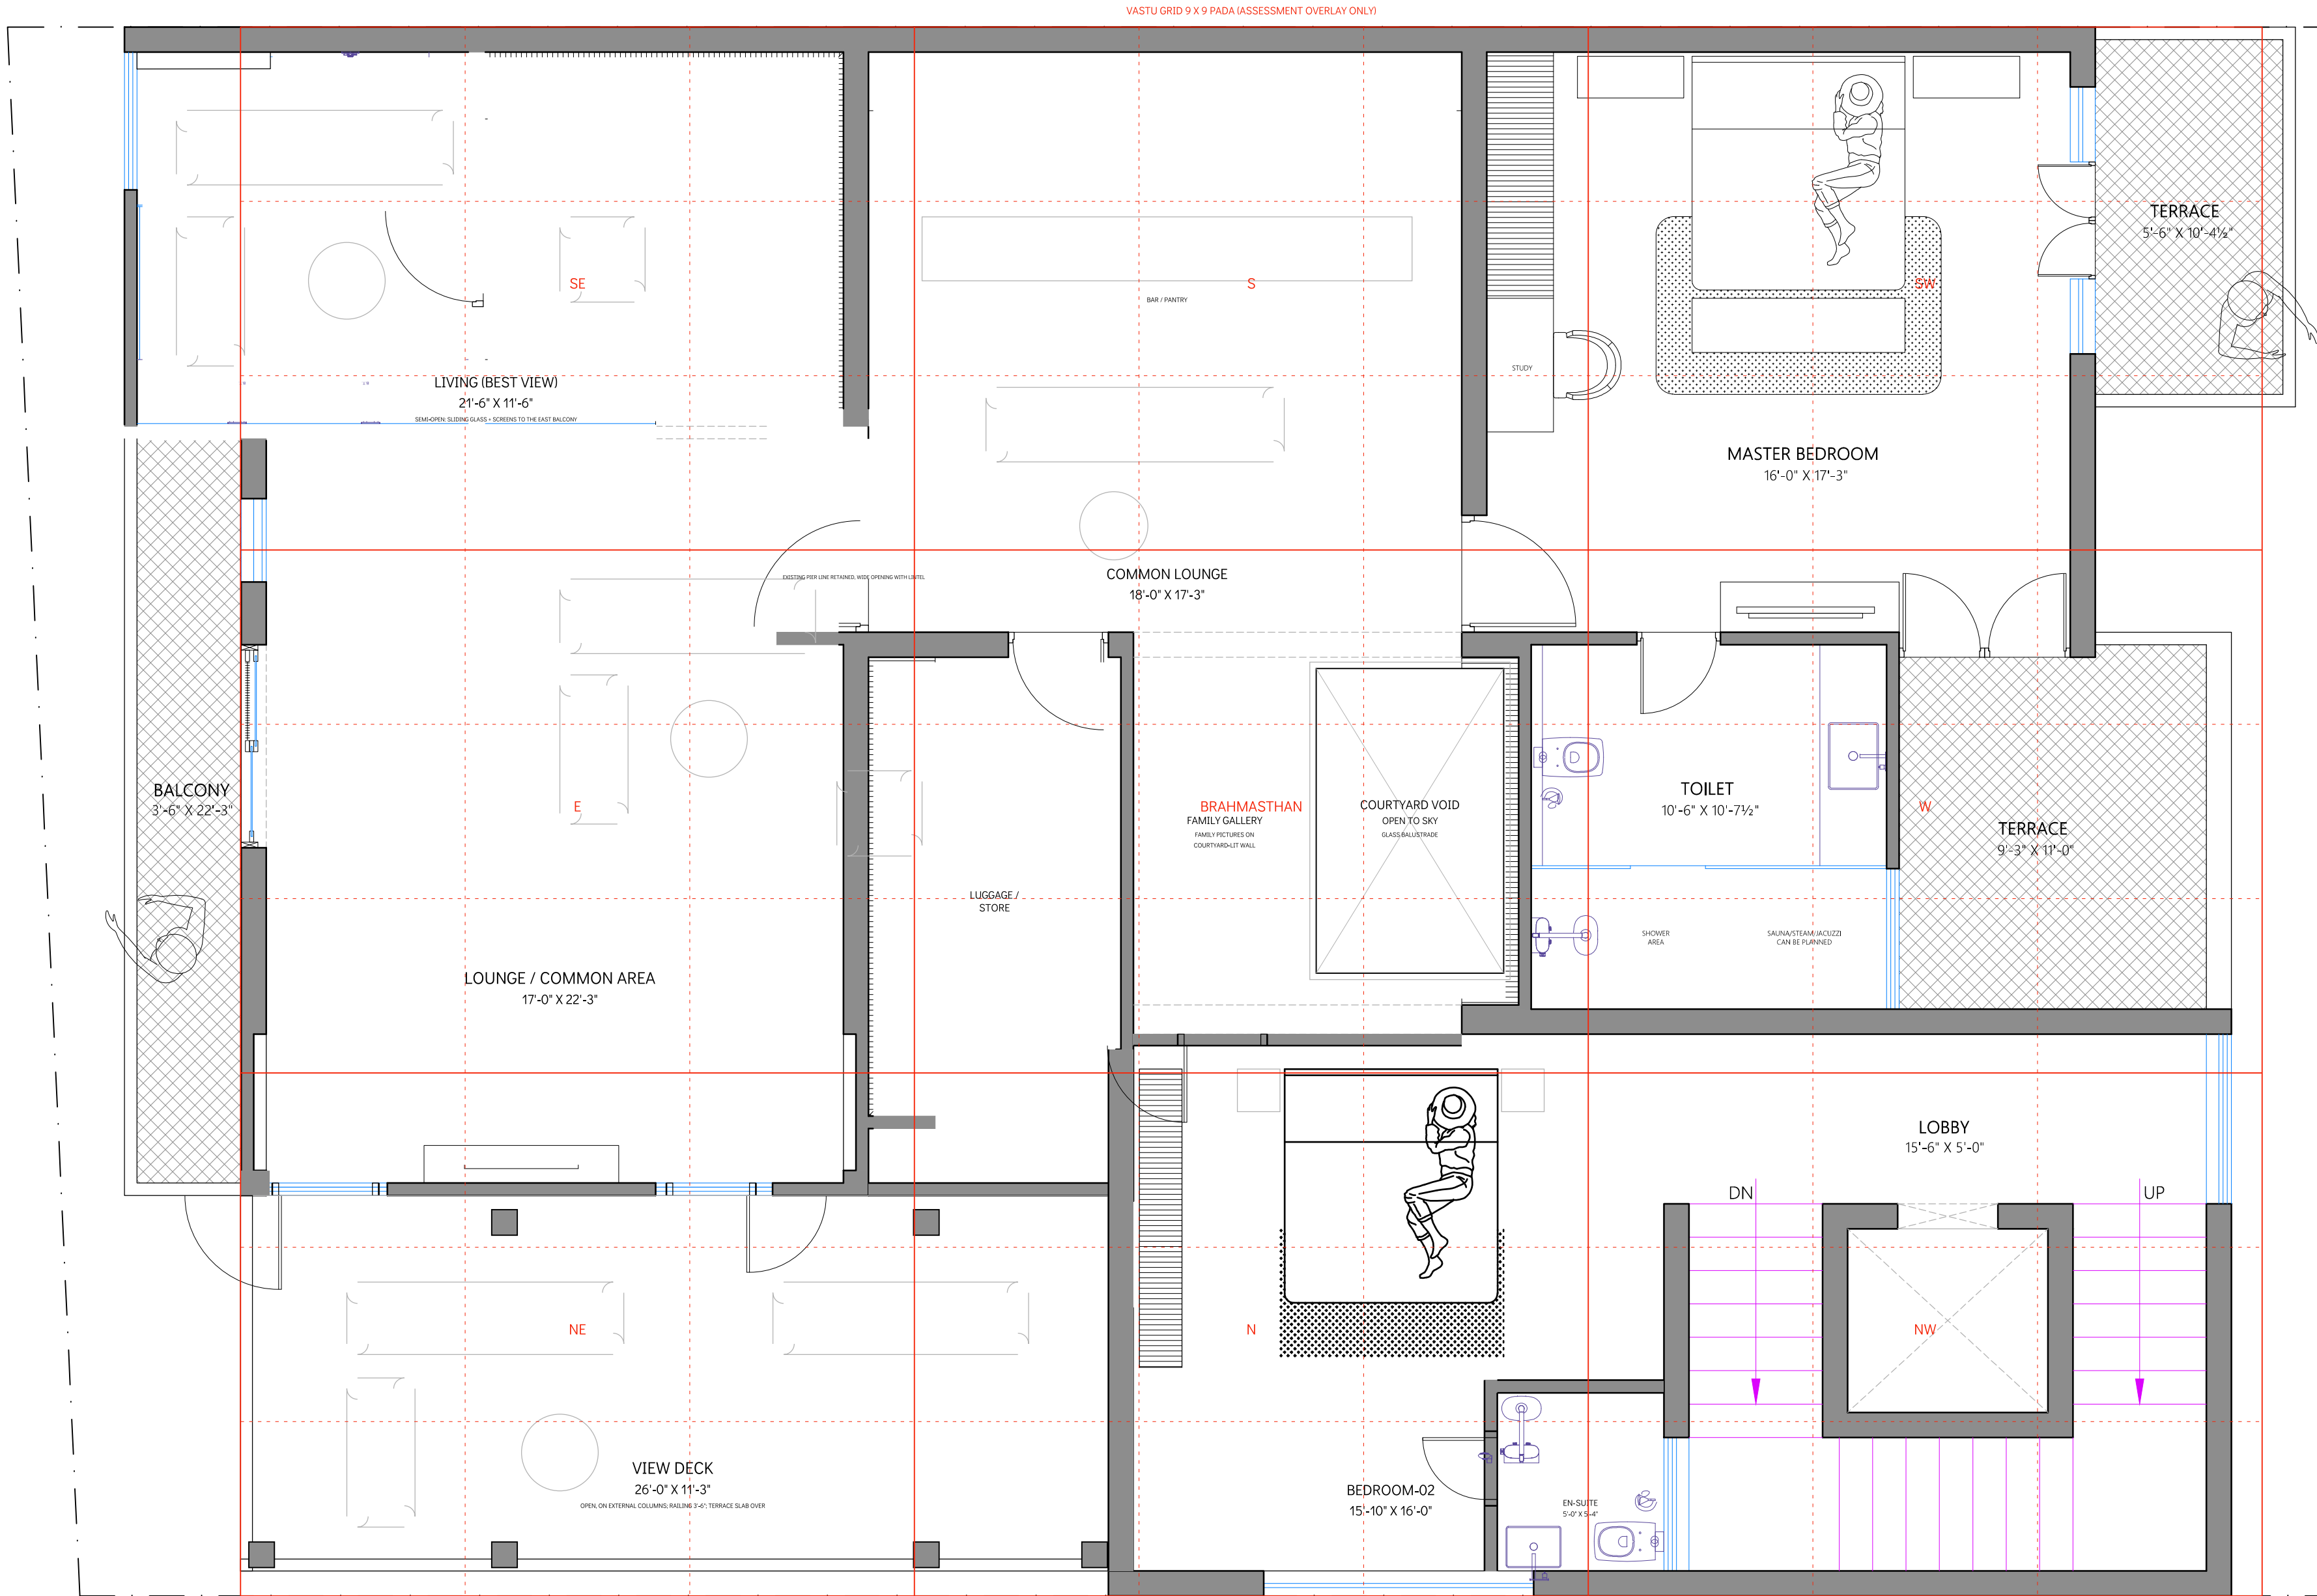

- NOTES:
1. Read this drawing along with relevant architectural, structural or service drawings.
 2. Do not scale; drawing should be read only.
 3. Any discrepancy to be brought to the notice of the architect before commencement of work.
 4. This drawing is a property of Ar. Akash Purohit and shall not be used or reproduced in any manner without the permission of the architects.

PROJECT:
17- CHANDRA PATH

SHEET TITLE:
SECOND FLOOR- LAYOUT

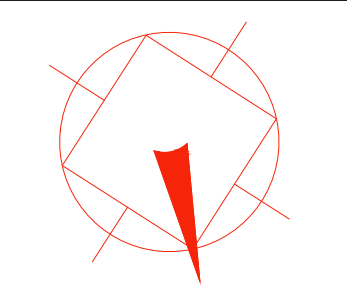

DRAWING NO:
SF-PP-01

DEALT BY:
KAPIL

CHECKED BY:
AKASH

SCALE:
N.T.S.


DATE:
15-09-2026

FILE PATH:

studio sqft

AR. AKASH PUROHIT
ar.akashpurohit@gmail.com
9784784226

- NOTES (SECOND FLOOR, R3):
1. SOUTH-EAST TOILET, WALK-IN CLOSET AND BEDROOM-02 REMOVED; THE SOUTH-EAST CORNER WITH THE BEST VIEW BECOMES THE LIVING ROOM, THE REST A COMMON LOUNGE. FORMER NORTH WINDOWS BECOME DOORS TO THE GARDEN AND BEDROOM-02, OR ARE INFILLED.
 2. BEDROOM-02 WITH EN-SUITE IN THE FORMER LIVING OVER THE PORCH (NORTH-WEST); THE NEW EAST WING AT THIS LEVEL IS AN OPEN VIEW DECK ON EXTERNAL COLUMNS, NO WALLS. 3. STRUCTURAL WALL LINES RETAINED AS PIERS; OPENINGS WITH LINTELS.
 4. FAMILY GALLERY ALONG THE COURTYARD VOID. 5. VASTU GRID (RED) IS AN ASSESSMENT OVERLAY ONLY.

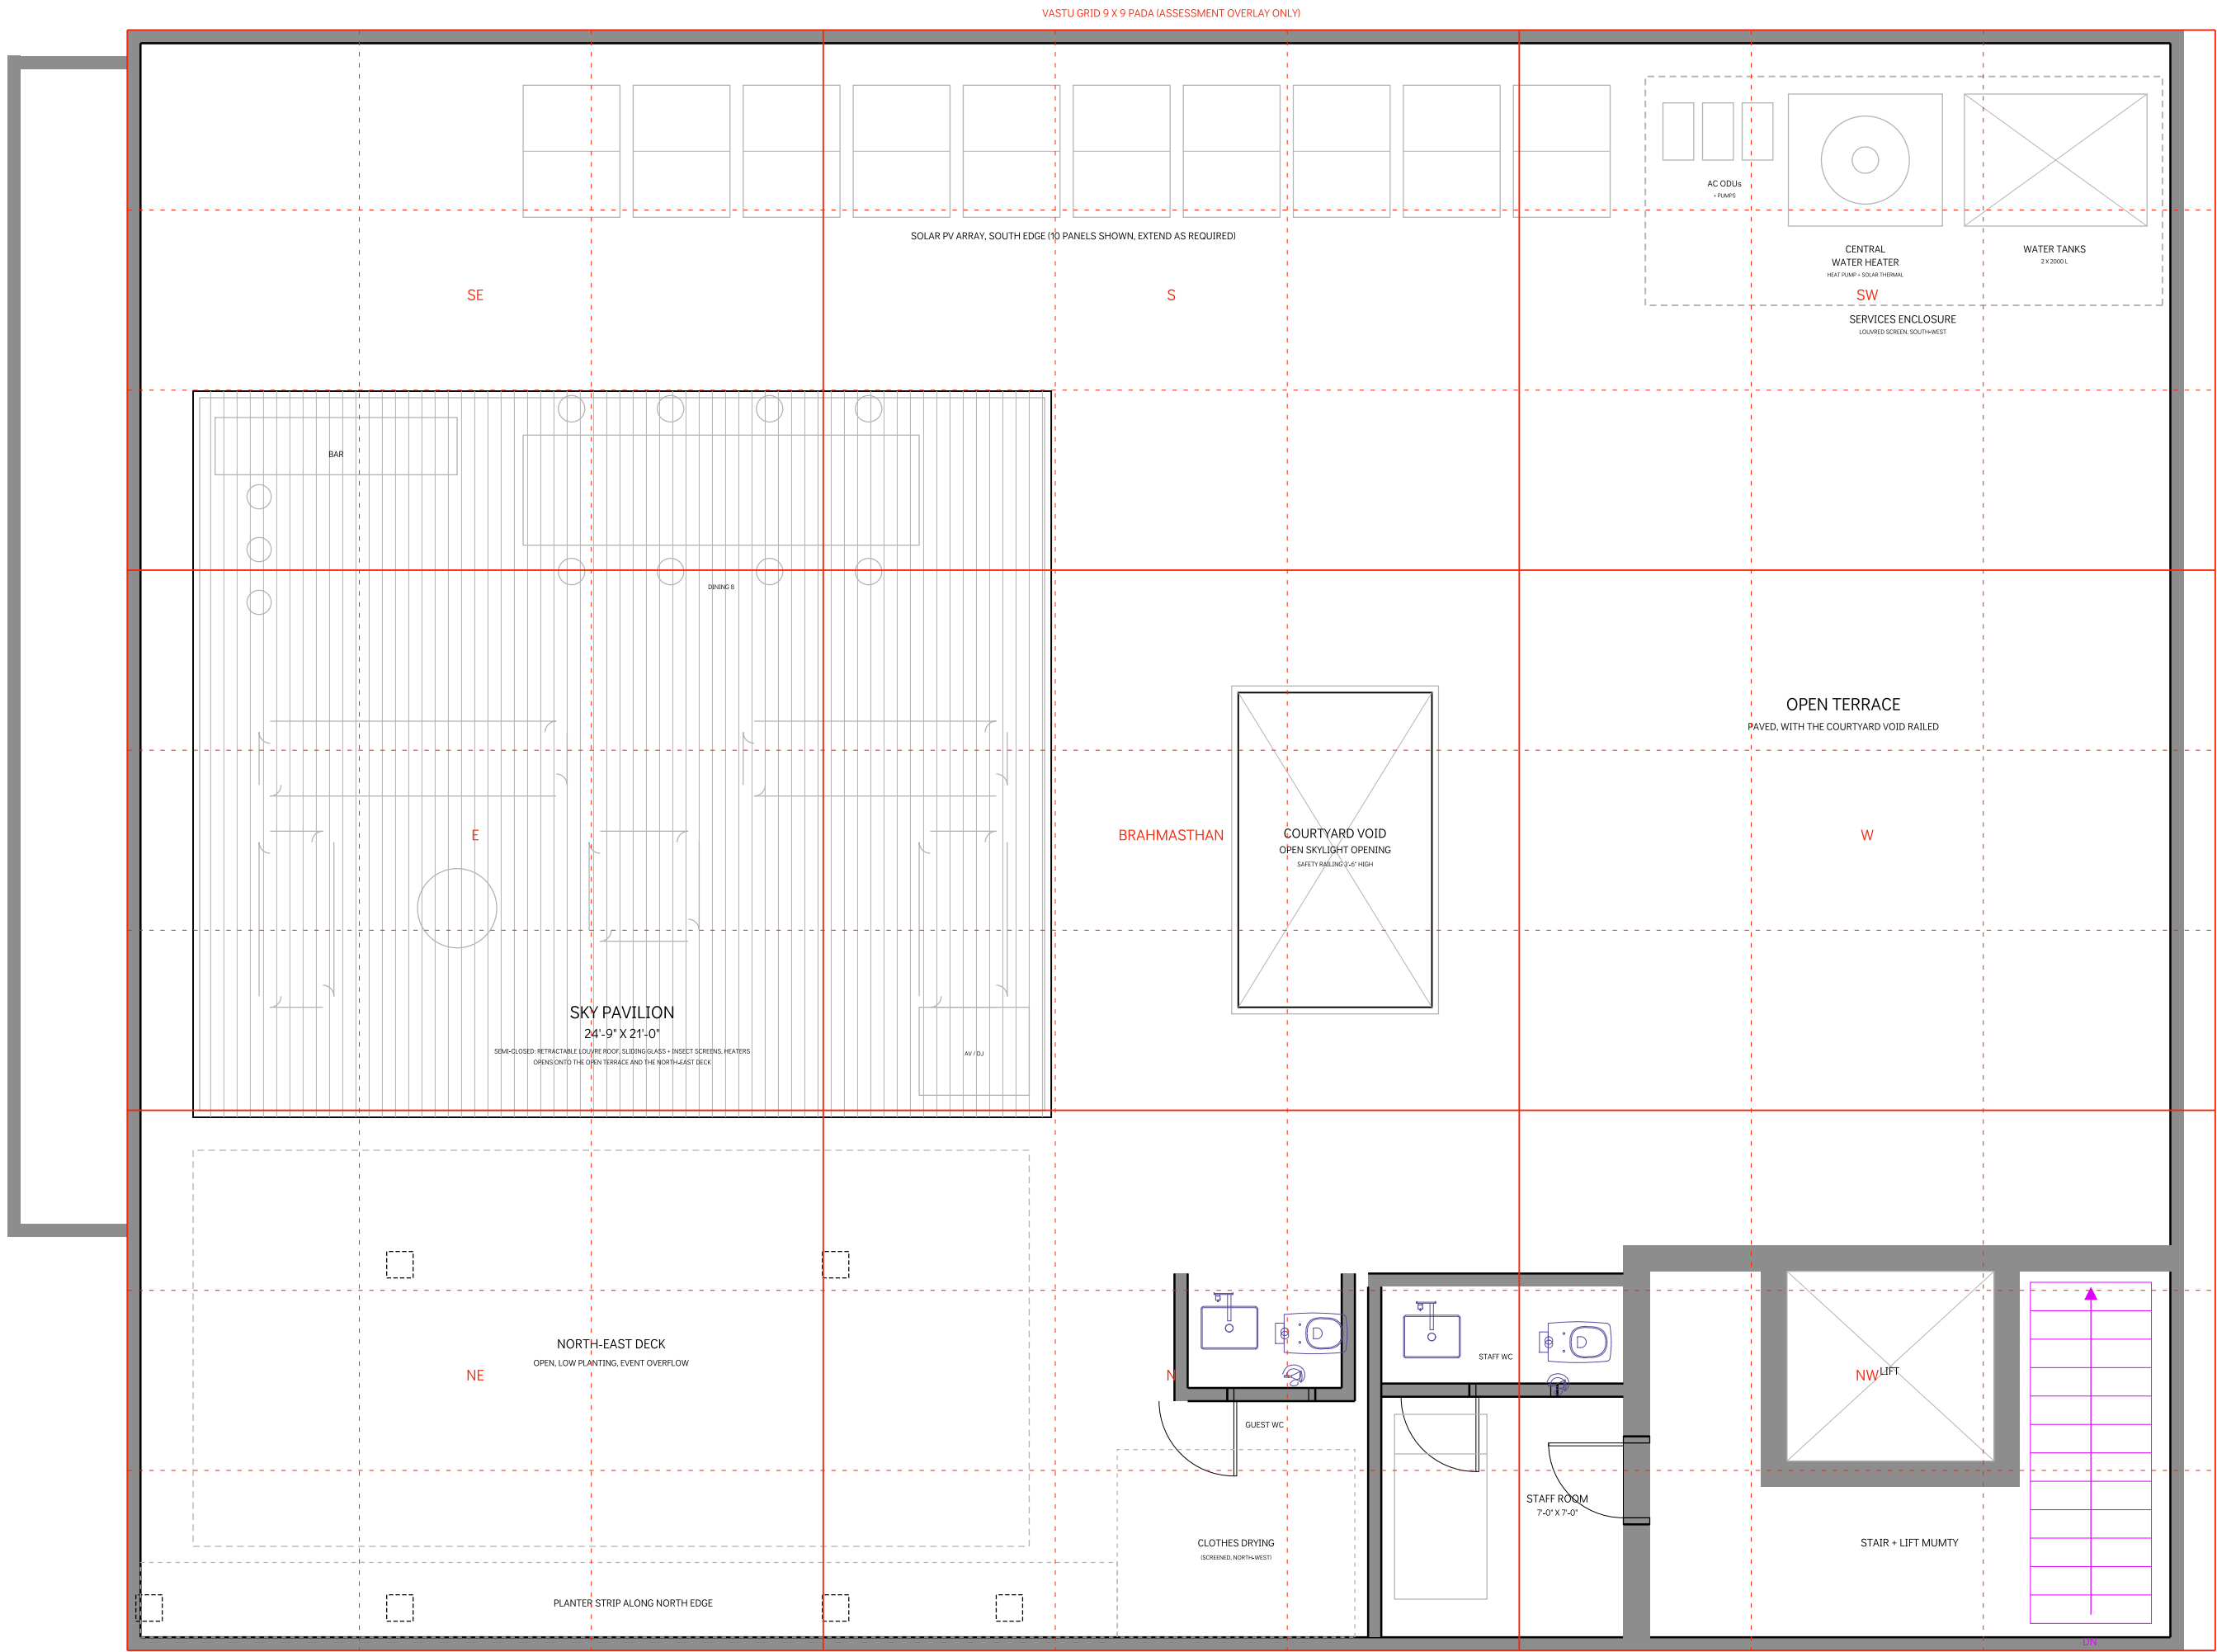

TERRACE FLOOR - LAYOUT

TF-PP-01

NOTES (TERRACE, R5):
1. PARAPET 3'-6" HIGH ALL ROUND; COURTYARD VOID RAILED. 2. WATER TANKS, CENTRAL WATER HEATER, AC OUTDOOR UNITS AND PUMPS IN A LOUVRED SERVICES ENCLOSURE IN THE SOUTH-WEST; SOLAR PV ALONG THE SOUTH PARAPET; NORTH-EAST KEPT OPEN AND LOW (VASTU).
3. SKY PAVILION ON THE EAST: STEEL FRAME, RETRACTABLE LOUVRE ROOF, SLIDING GLASS WITH INSECT SCREENS, BAR, DINING AND LOUNGE; POWER AND WATER TO THE BAR. 4. STAFF ROOM, WC, GUEST WC AND SCREENED DRYING YARD BESIDE THE MUMTY (NORTH-WEST).
5. TERRACE SLAB OVER THE NORTH WING CARRIED ON THE EXTERNAL COLUMNS (DASHED); PAVILION AND SERVICES LOADS TO BE CHECKED BY THE STRUCTURAL ENGINEER. 6. WATERPROOFING AND SLOPES TO NORTH-EAST DRAIN POINTS. 7. VASTU GRID (RED) IS AN ASSESSMENT OVERLAY ONLY.