


BASEMENT -
RENOVATION LAYOUT

BF-PP-01

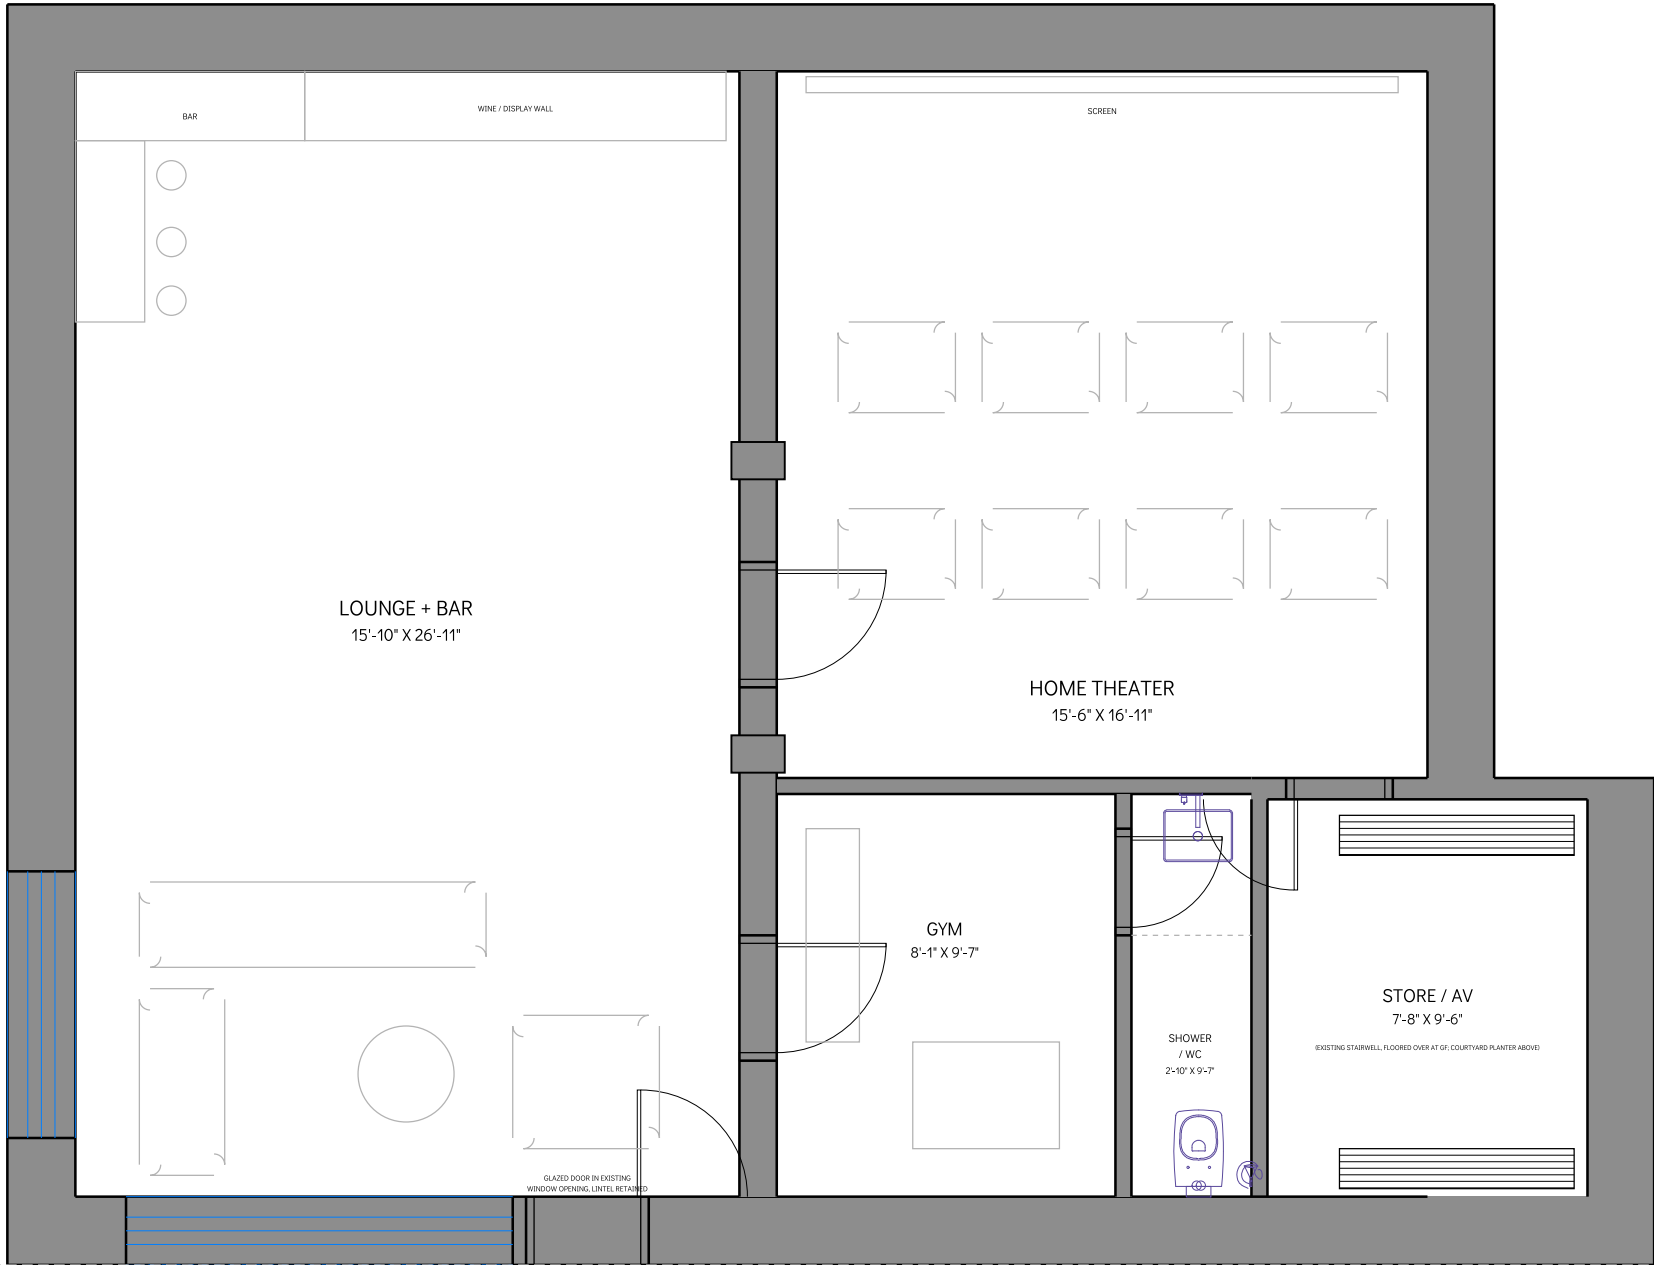


NOTES (BASEMENT):

1. Existing stairwell floored over at ground floor level; the well below is the store / AV room; the courtyard planter above it is waterproofed. The Brahmashan above stays open.
2. Basement entry by the stair in the west part of the existing north light well (north padas 3-4, outside the Brahmashan and the north-east); north window opening converted to a glazed door, sill masonry removed, lintel retained.
3. The servant room is at grade on the east side (see GF-PP-01), not at this level.
4. Existing ceiling height 8'-6". Existing RCC columns and hidden beam on the centre line are retained; theater partition is non-load-bearing.
5. No new opening in the ground floor slab. Existing basement windows and walls otherwise unchanged.

1. Read this drawing along with relevant architectural, structural or service drawings.
2. Do not scale; drawing should be read only.
3. Any discrepancy to be brought to the notice of the architect before commencement of work.
4. This drawing is a property of Ar. Akash Purohit and shall not be used or reproduced in any manner without the permission of the architects.

SHEET TITLE:

**GROUND FLOOR -
RENOVATION LAYOUT**

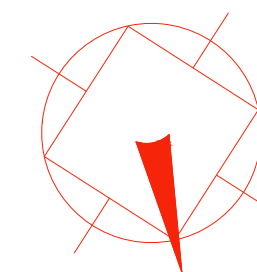


DEALT BY: KAPIL	CHECKED BY: AKASH
--------------------	----------------------

FILE PATH:

studio sqft

AR. AKASH PUROHIT
ar.akashpurohit@gmail.com
9784784226

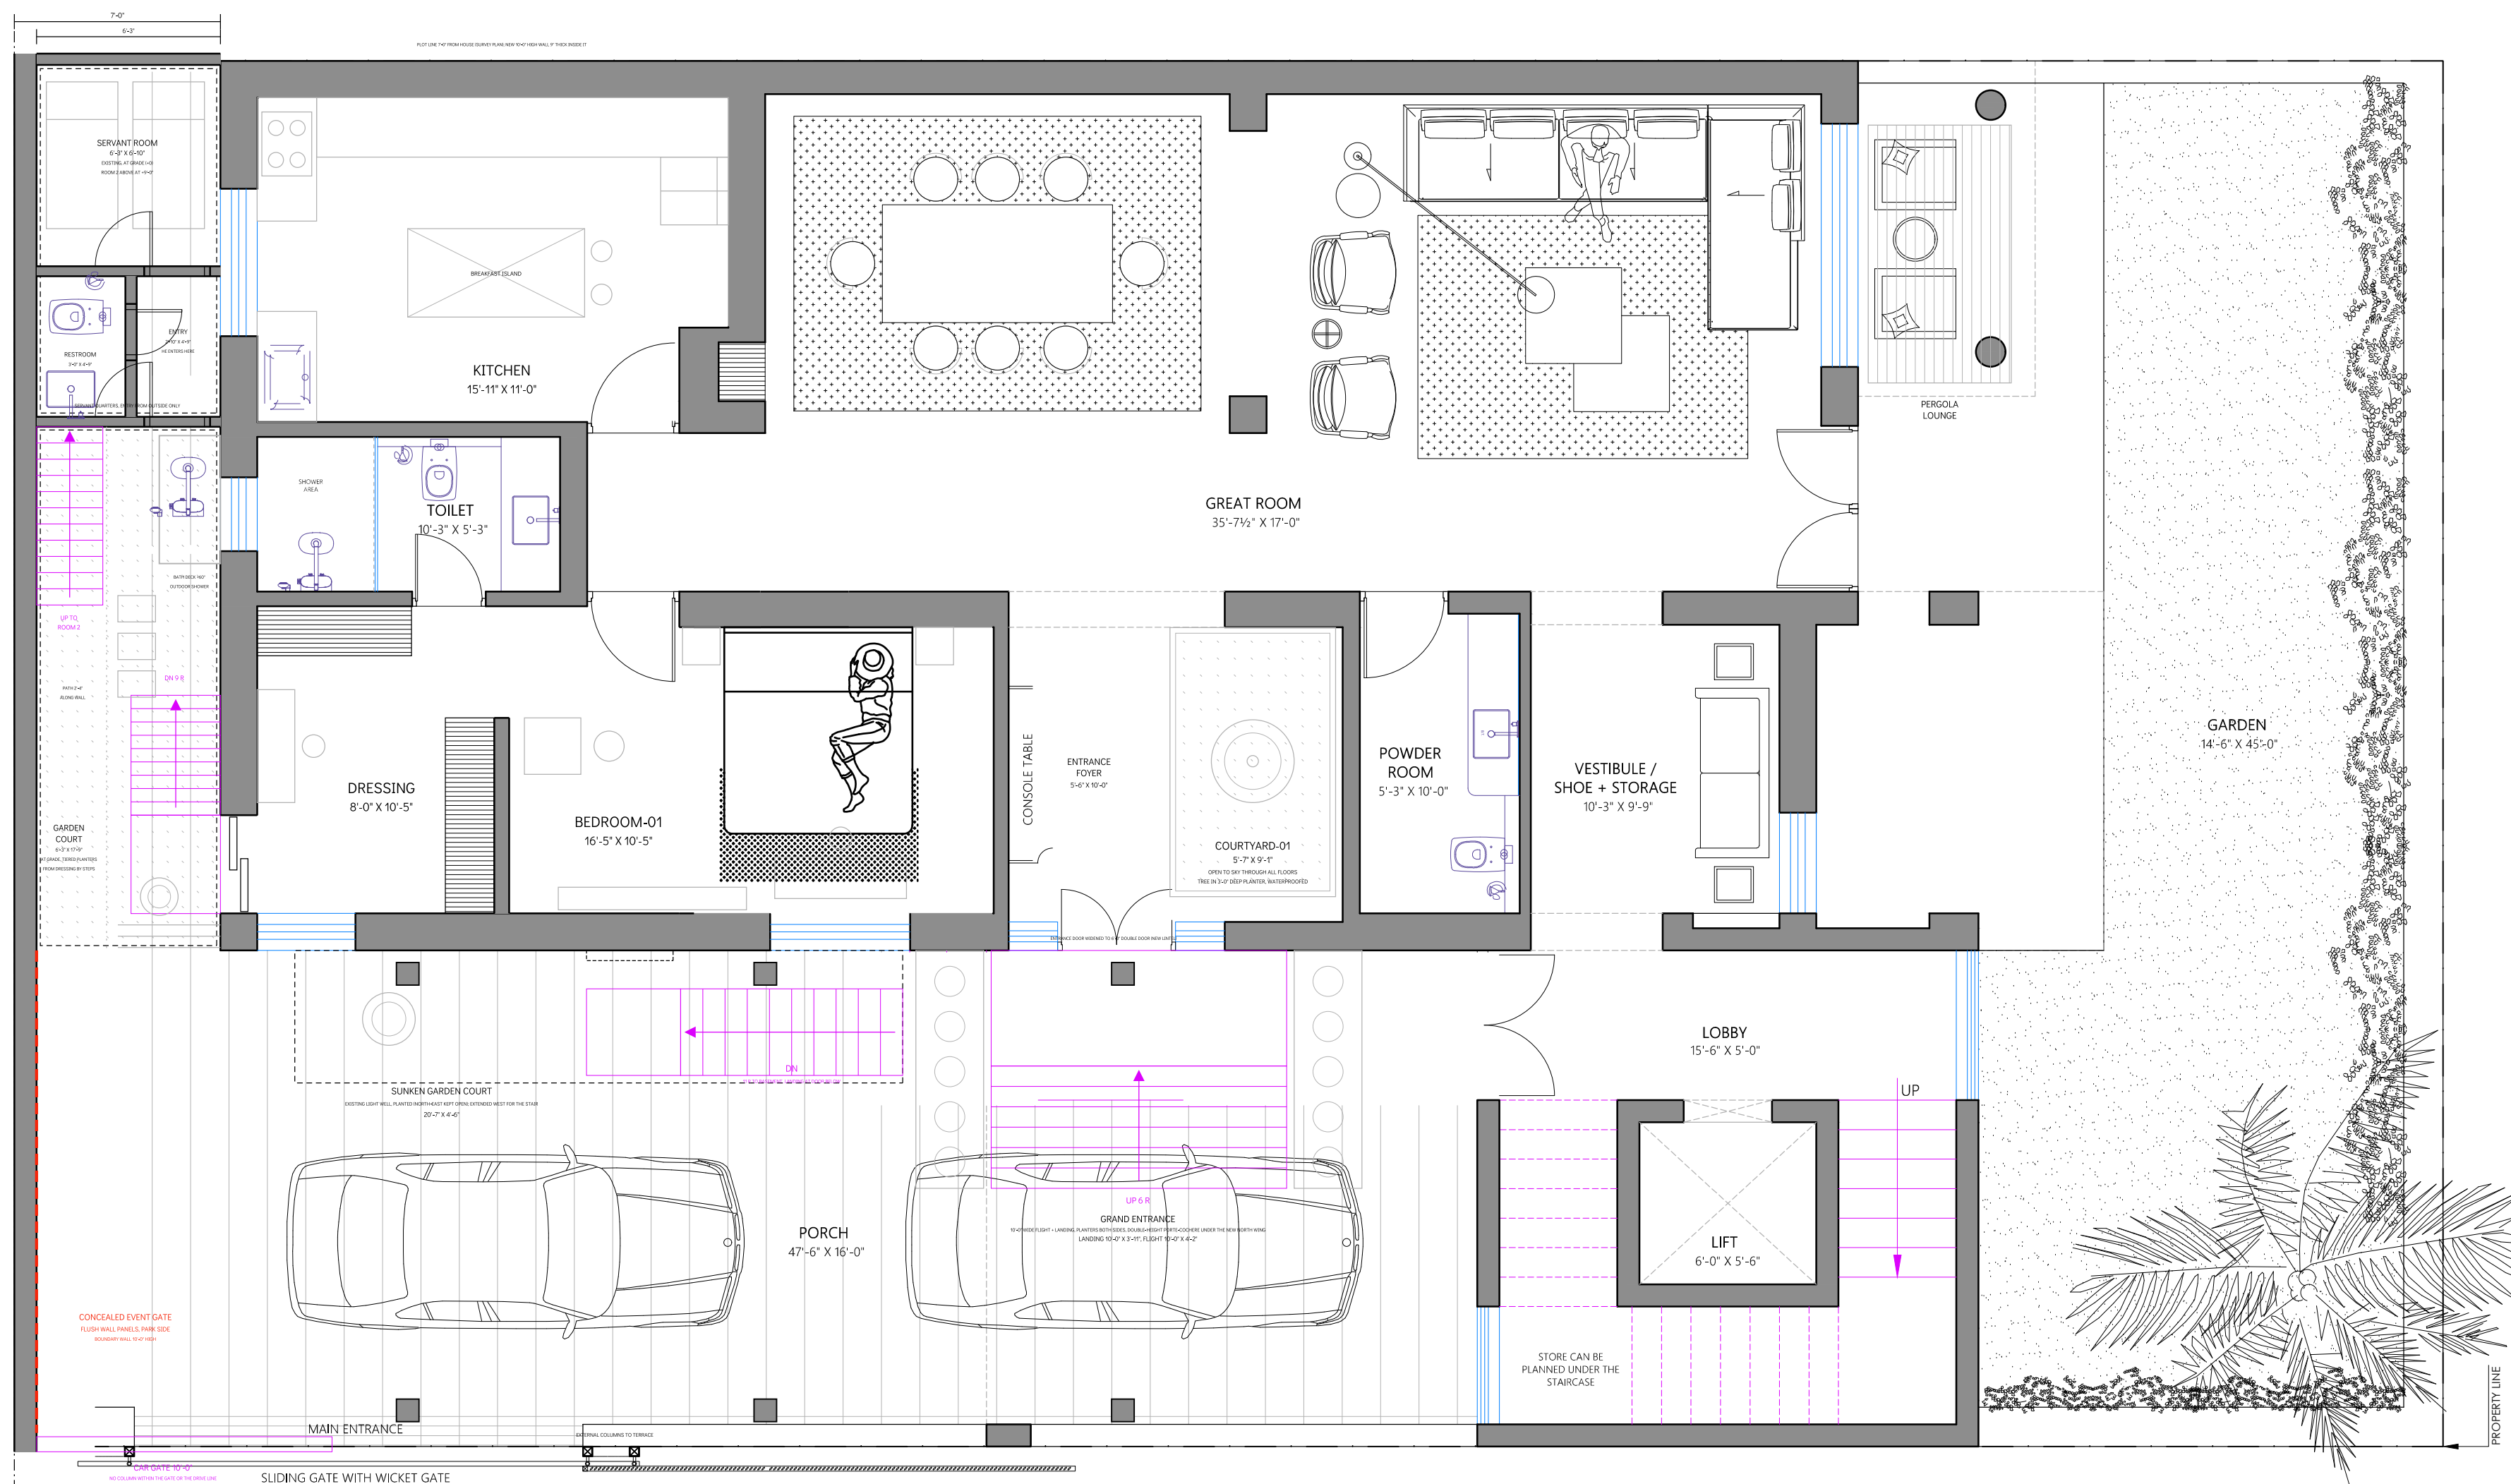

NOTES (REVISION R3):

A. EAST PLOT LINE 7'-0" FROM THE HOUSE (SURVEY PLAN, TOP-LEFT CORNER), TAKEN STRAIGHT FOR THE FULL LENGTH. NEW 10'-0" HIGH BOUNDARY WALL 9" THICK INSIDE IT. CLEAR STRIP 6'-3". NO OPENINGS TO THE PARK EXCEPT THE EVENT GATE; CAR GATE 10'-0" AT THE EAST END OF THE NORTH BOUNDARY.


B. CONCEALED EVENT GATE IN THE EAST BOUNDARY WALL FROM THE HOUSE CORNER TO THE FRONT BOUNDARY: FLUSH WALL-FINISHED PANELS ON CONCEALED PIVOTS, OPENED ONLY FOR EVENTS.

C. COURTYARD-Y-1 IN THE EXISTING STAIRWELL SHAFT, OPEN TO SKY THROUGH ALL FLOORS: THE BRAHMASTHAN (CENTRE OF THE WHOLE-HOUSE GRID) IS KEPT OPEN AND FREE OF STAIRS. ENTRANCE STEPS ARE A COMPACT 6-RISER LIGHT OUTSIDE. THE EXISTING DOOR; BASEMENT FLOOR; BASEMENT STAIR IN THE WEST PART OF THE EXISTING LIGHT WELL. LIFT GIVES THE STEP-FREE ROUTE.

D. EAST STAIR: SERVANT QUARTERS AT GRADE IN THE SOUTH-EAST EXISTING ROOM; RESTROOM ON THE EAST, ENTRY ON THE WEST. SECOND ROOM ABOVE AT -4'-0" BY AN EXTERNAL STAIR ALONG THE WALL ENTERED FROM OUTSIDE ONLY, NO DOOR INTO THE HOUSE. NORTH OF IT ONE OPEN GARDEN COURT AT GRADE WITH TIERED PLANTERS, THE SERVANT'S PATH ALONG THE WALL, A BATH DECK AT -6'0" WITH THE OUTDOOR SHOWER, AND STEPS DOWN FROM THE DRESSING.

E. SERVICE WING ROOFED AT 7'-6" WITH A PLANTER PARAPET; BATHROOM EAST WINDOW IN OBSCURE GLASS. GRAND ENTRANCE: 10'-0" FLIGHT CENTRED ON THE WIDENED FRONT DOOR (NORTH PADA 5), BELOW THE BRAHMASTHAN LINE. BASEMENT STAIR IN THE NORTH LIGHT WELL. THE WHOLE BLOCK OVER THE PORCH LOBBY, LIFT, MAIN STAIR, UPPER LIVING ROOMS) IS DEMOLISHED AND REBUILT ON THE NEW COLUMN GRID. LIFT AND MAIN STAIR STAY IN THE NORTH-WEST.


F. ALL ROOM DIMENSIONS ARE CLEAR INTERNAL. SIZES TAKEN FROM THE DRAIN WALLS. SHEET ORIENTATION: TOP - SOUTH, BOTTOM - NORTH, LEFT - EAST, RIGHT - WEST.

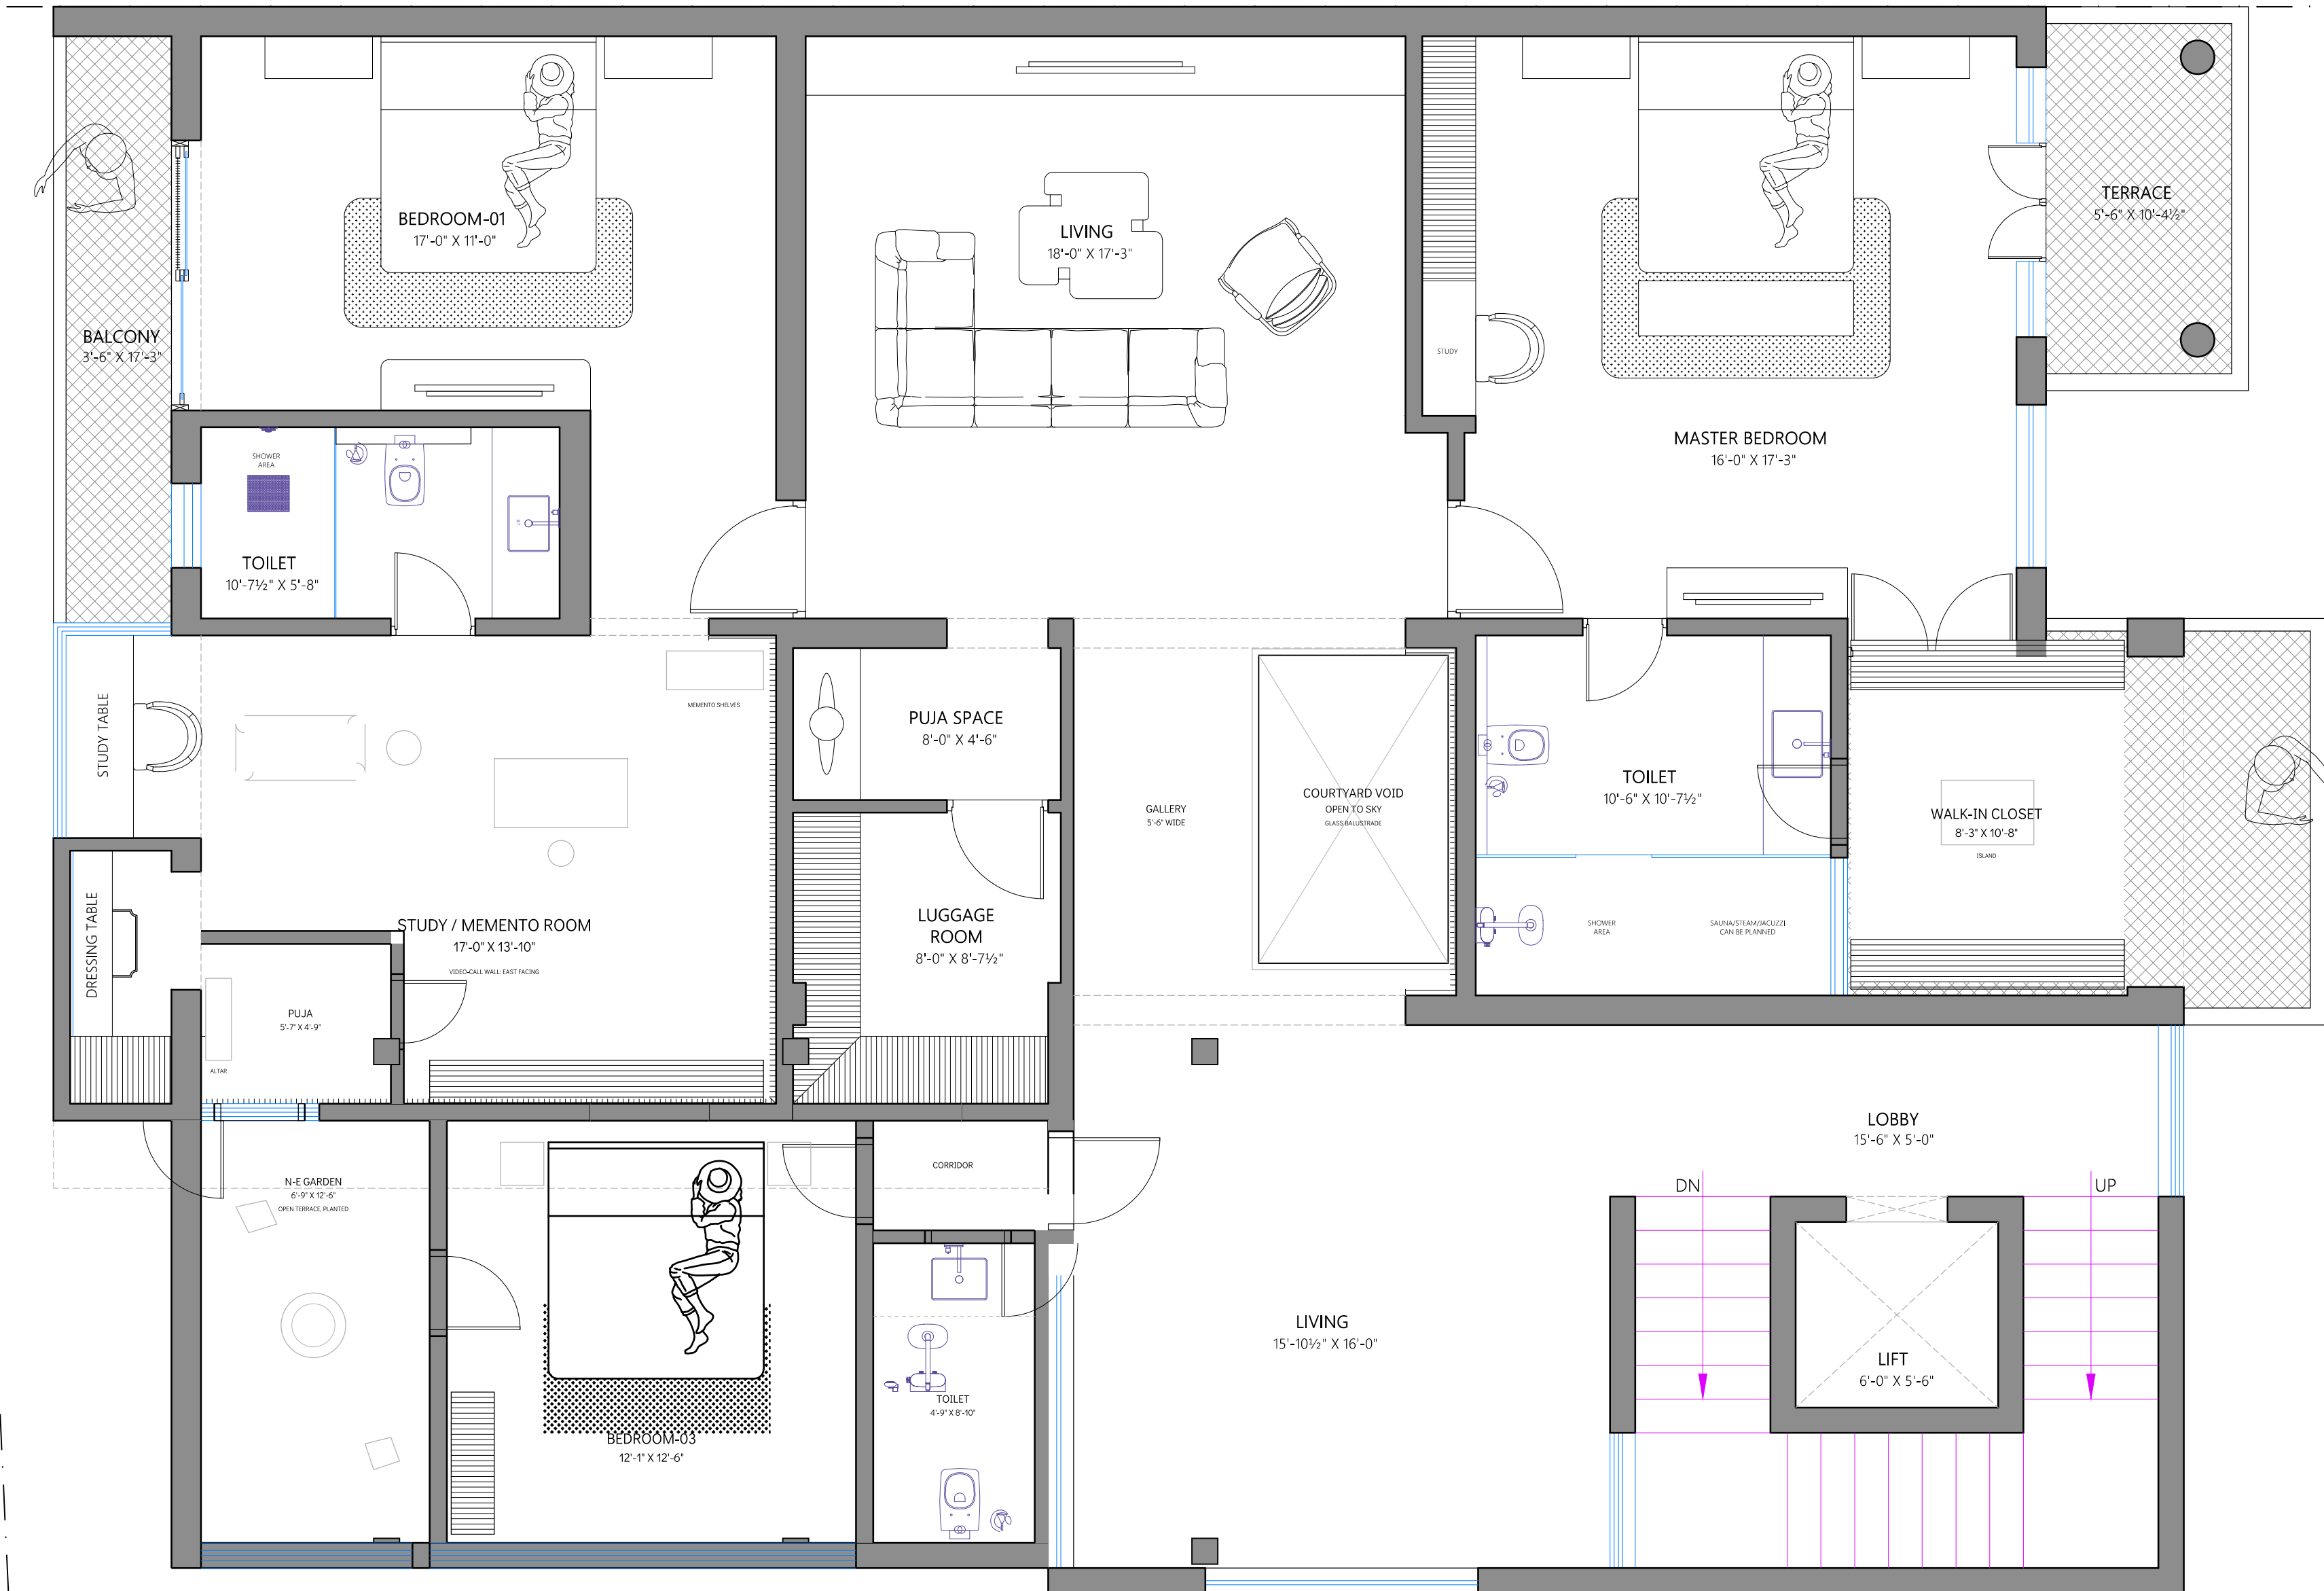

- NOTES:
1. Read this drawing along with relevant architectural, structural or service drawings.
 2. Do not scale; drawing should be read only.
 3. Any discrepancy to be brought to the notice of the architect before commencement of work.
 4. This drawing is a property of Ar. Akash Purohit and shall not be used or reproduced in any manner without the permission of the architects.

PROJECT:
17- CHANDRA PATH

SHEET TITLE:
**FIRST FLOOR -
RENOVATION LAYOUT**

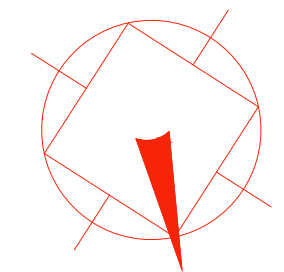

DRAWING NO:
FF-PP-01

DEALT BY:
KAPIL

CHECKED BY:
AKASH

SCALE:
N.T.S.

DATE:
15-09-2026


FILE PATH:

studio sqft

AR. AKASH PUROHIT

ar.akashpurohit@gmail.com
9784784226

- NOTES (FIRST FLOOR, R3):
1. THE BLOCK OVER THE PORCH IS REBUILT FROM SCRATCH ON RCC COLUMNS FROM FOUNDATION TO TERRACE (THREE ON THE PORCH LINE, THREE AT THE BACK AGAINST THE NORTH WALL, NONE WITHIN THE 10'-0" CAR GATE OR THE DRIVE LINE), INDEPENDENT OF THE STONE WALLS; TO STRUCTURAL DESIGN.
 2. FORMER WEST TERRACE ENCLOSED AS MASTER WALK-IN CLOSET (LIGHT PARTITIONS ON EXISTING SLAB); 3. NORTH-EAST ROOM RE-PURPOSED AS STUDY WITH PUJA IN ITS NORTH-EAST CORNER.
 4. COURTYARD VOID WITHIN THE EXISTING STAIRWELL SHAFT; GLASS BALUSTRADE; 5. ROOM DIMENSIONS ARE CLEAR INTERNAL SIZES FROM THE DRAWN WALLS.

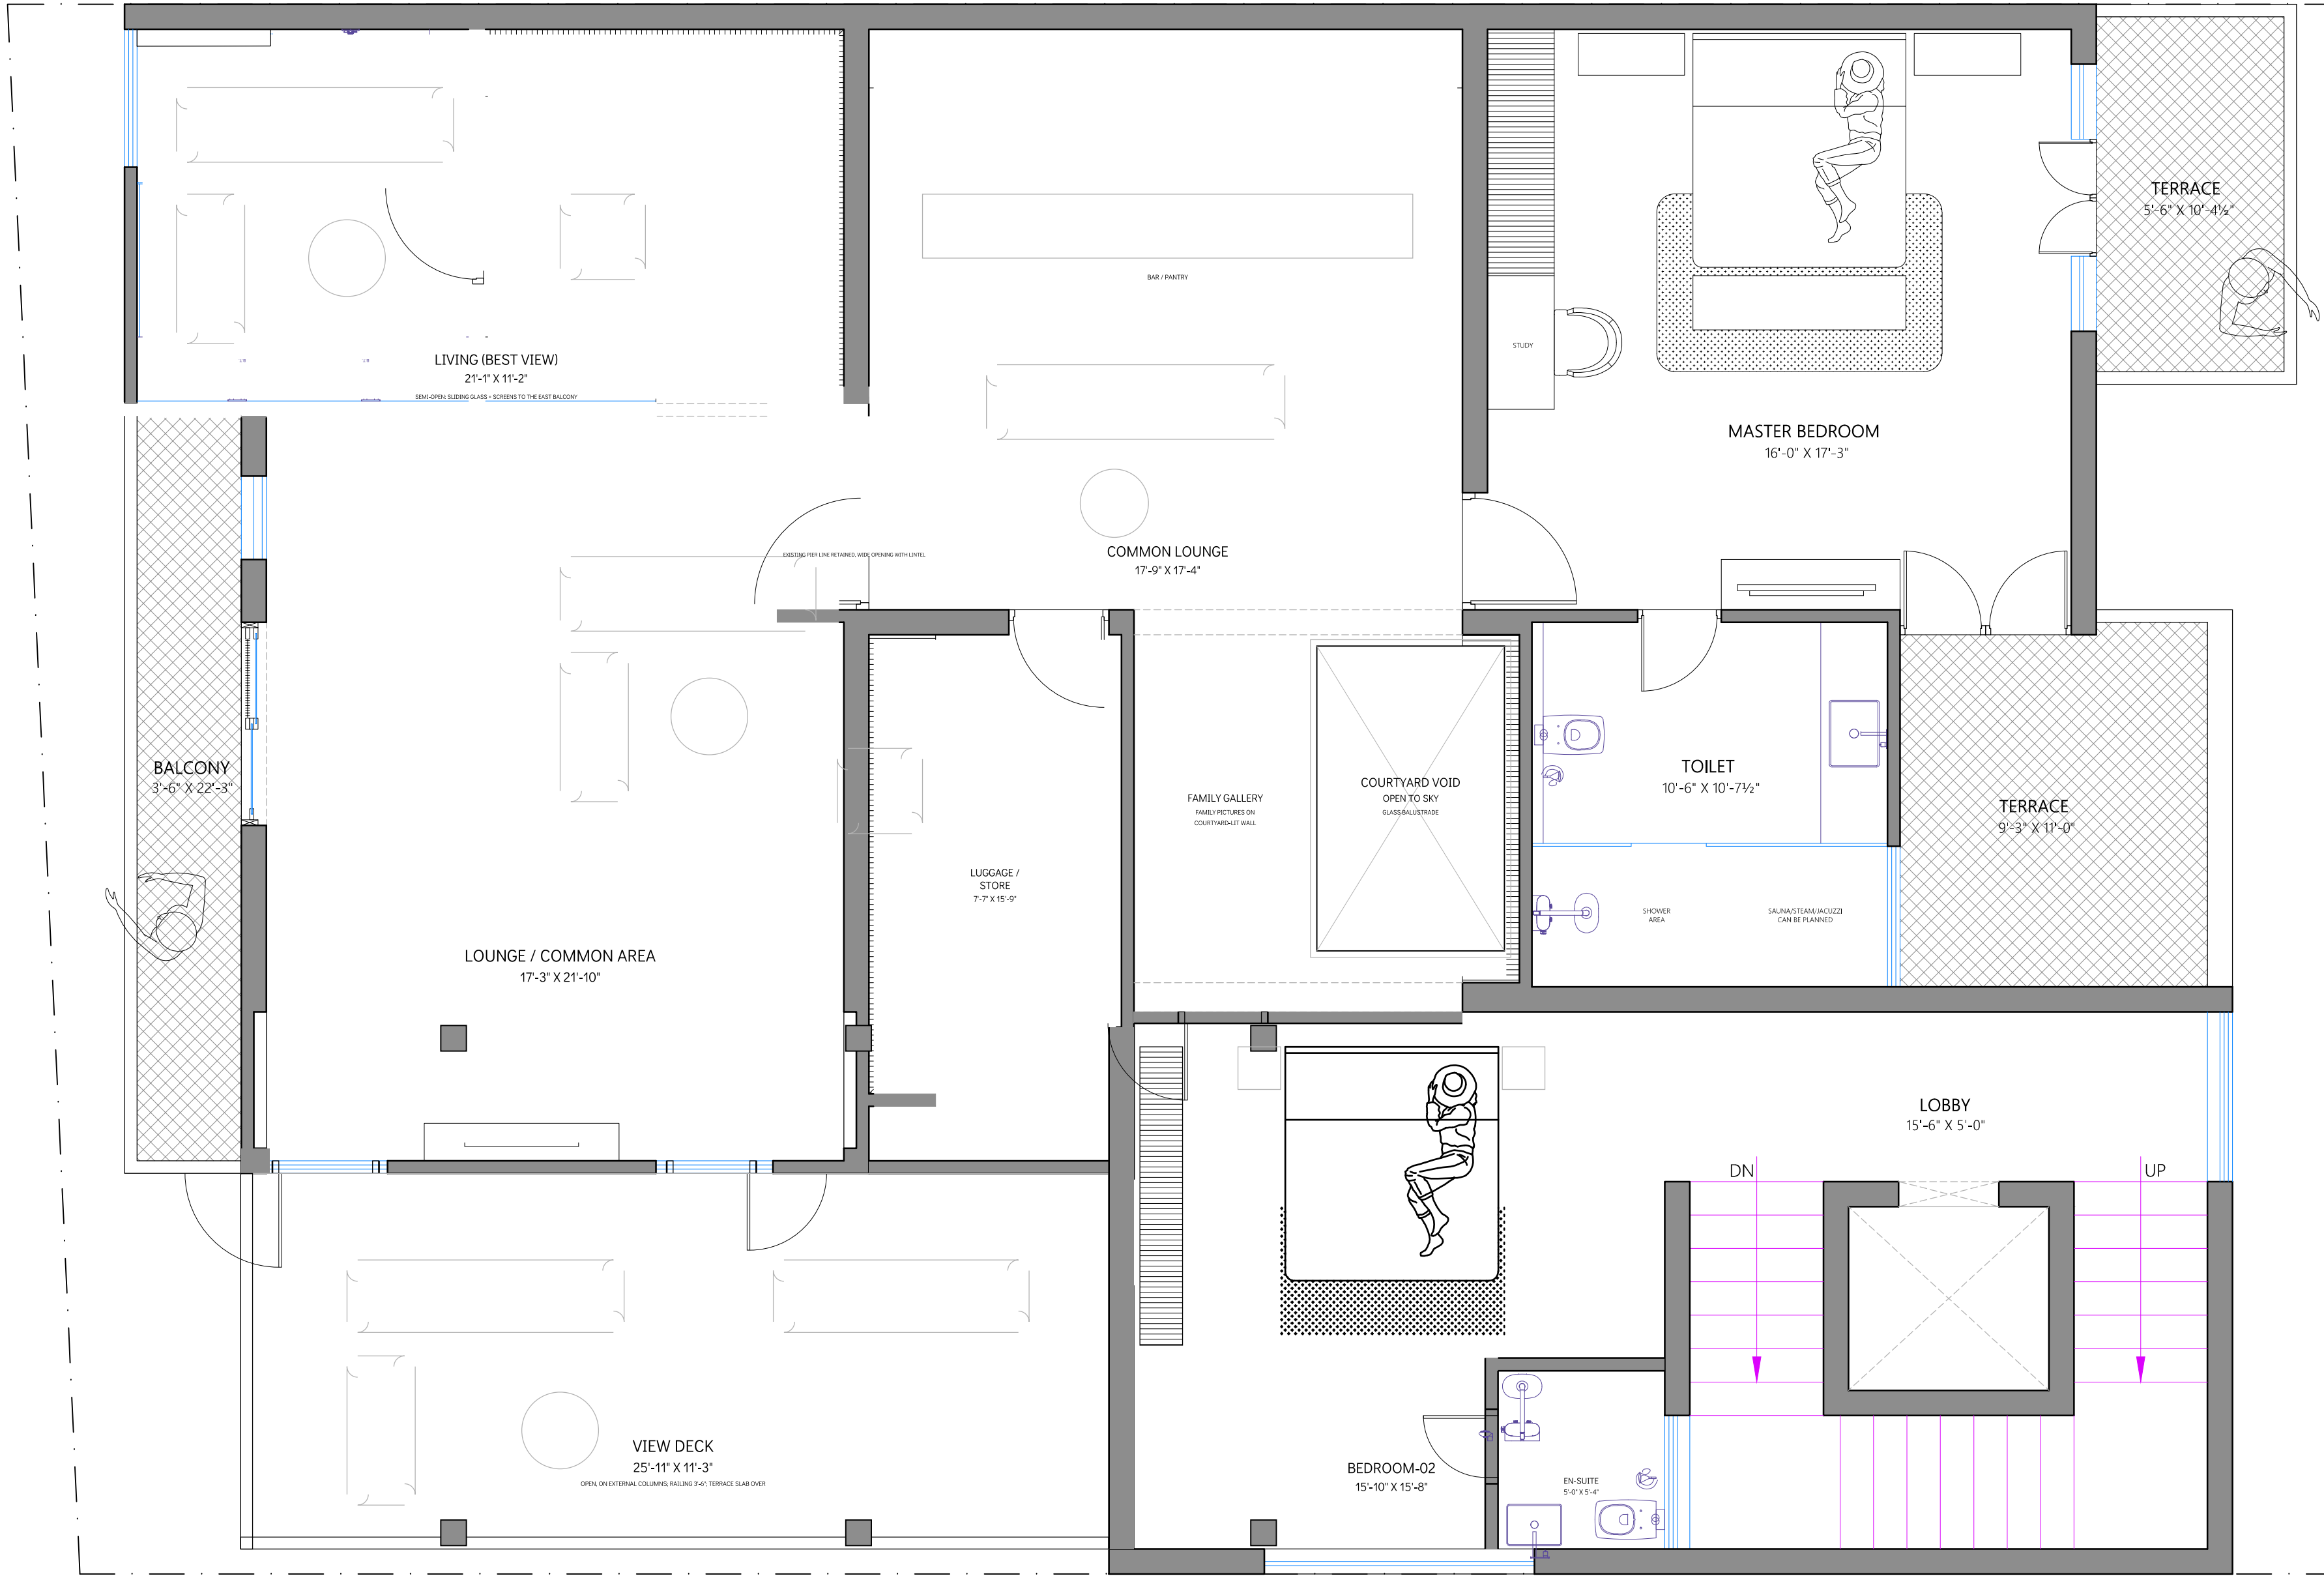


NOTES (SECOND FLOOR, R3):
1. SOUTH-EAST TOILET, WALK-IN CLOSET AND BEDROOM-02 REMOVED; THE SOUTH-EAST CORNER WITH THE BEST VIEW BECOMES THE LIVING ROOM, THE REST A COMMON LOUNGE. FORMER NORTH WINDOWS BECOME DOORS TO THE GARDEN AND BEDROOM-02, OR ARE INFILLED.
2. BEDROOM-02 WITH EN-SUITE IN THE FORMER LIVING OVER THE PORCH (NORTH-WEST); THE NEW EAST WING AT THIS LEVEL IS AN OPEN VIEW DECK ON EXTERNAL COLUMNS, NO WALLS. 3. STRUCTURAL WALL LINES RETAINED AS PIERS; OPENINGS WITH LINTELS.
4. FAMILY GALLERY ALONG THE COURTYARD VOID. 5. ROOM DIMENSIONS ARE CLEAR INTERNAL SIZES FROM THE DRAWN WALLS.

- NOTES:
1. Read this drawing along with relevant architectural, structural or service drawings.
 2. Do not scale; drawing should be read only.
 3. Any discrepancy to be brought to the notice of the architect before commencement of work.
 4. This drawing is a property of Ar. Akash Purohit and shall not be used or reproduced in any manner without the permission of the architects.

PROJECT:
17- CHANDRA PATH

SHEET TITLE:
SECOND FLOOR- LAYOUT

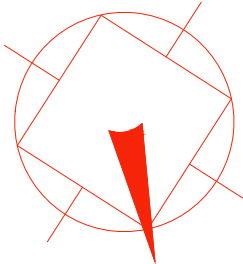

DRAWING NO:
SF-PP-01

DEALT BY:
KAPIL

CHECKED BY:
AKASH

SCALE:
N.T.S.

DATE:
15-09-2026

FILE PATH:

studio sqft

AR. AKASH PUROHIT
ar.akashpurohit@gmail.com
9784784226

