



BASEMENT -
RENOVATION LAYOUT

BF-PP-01

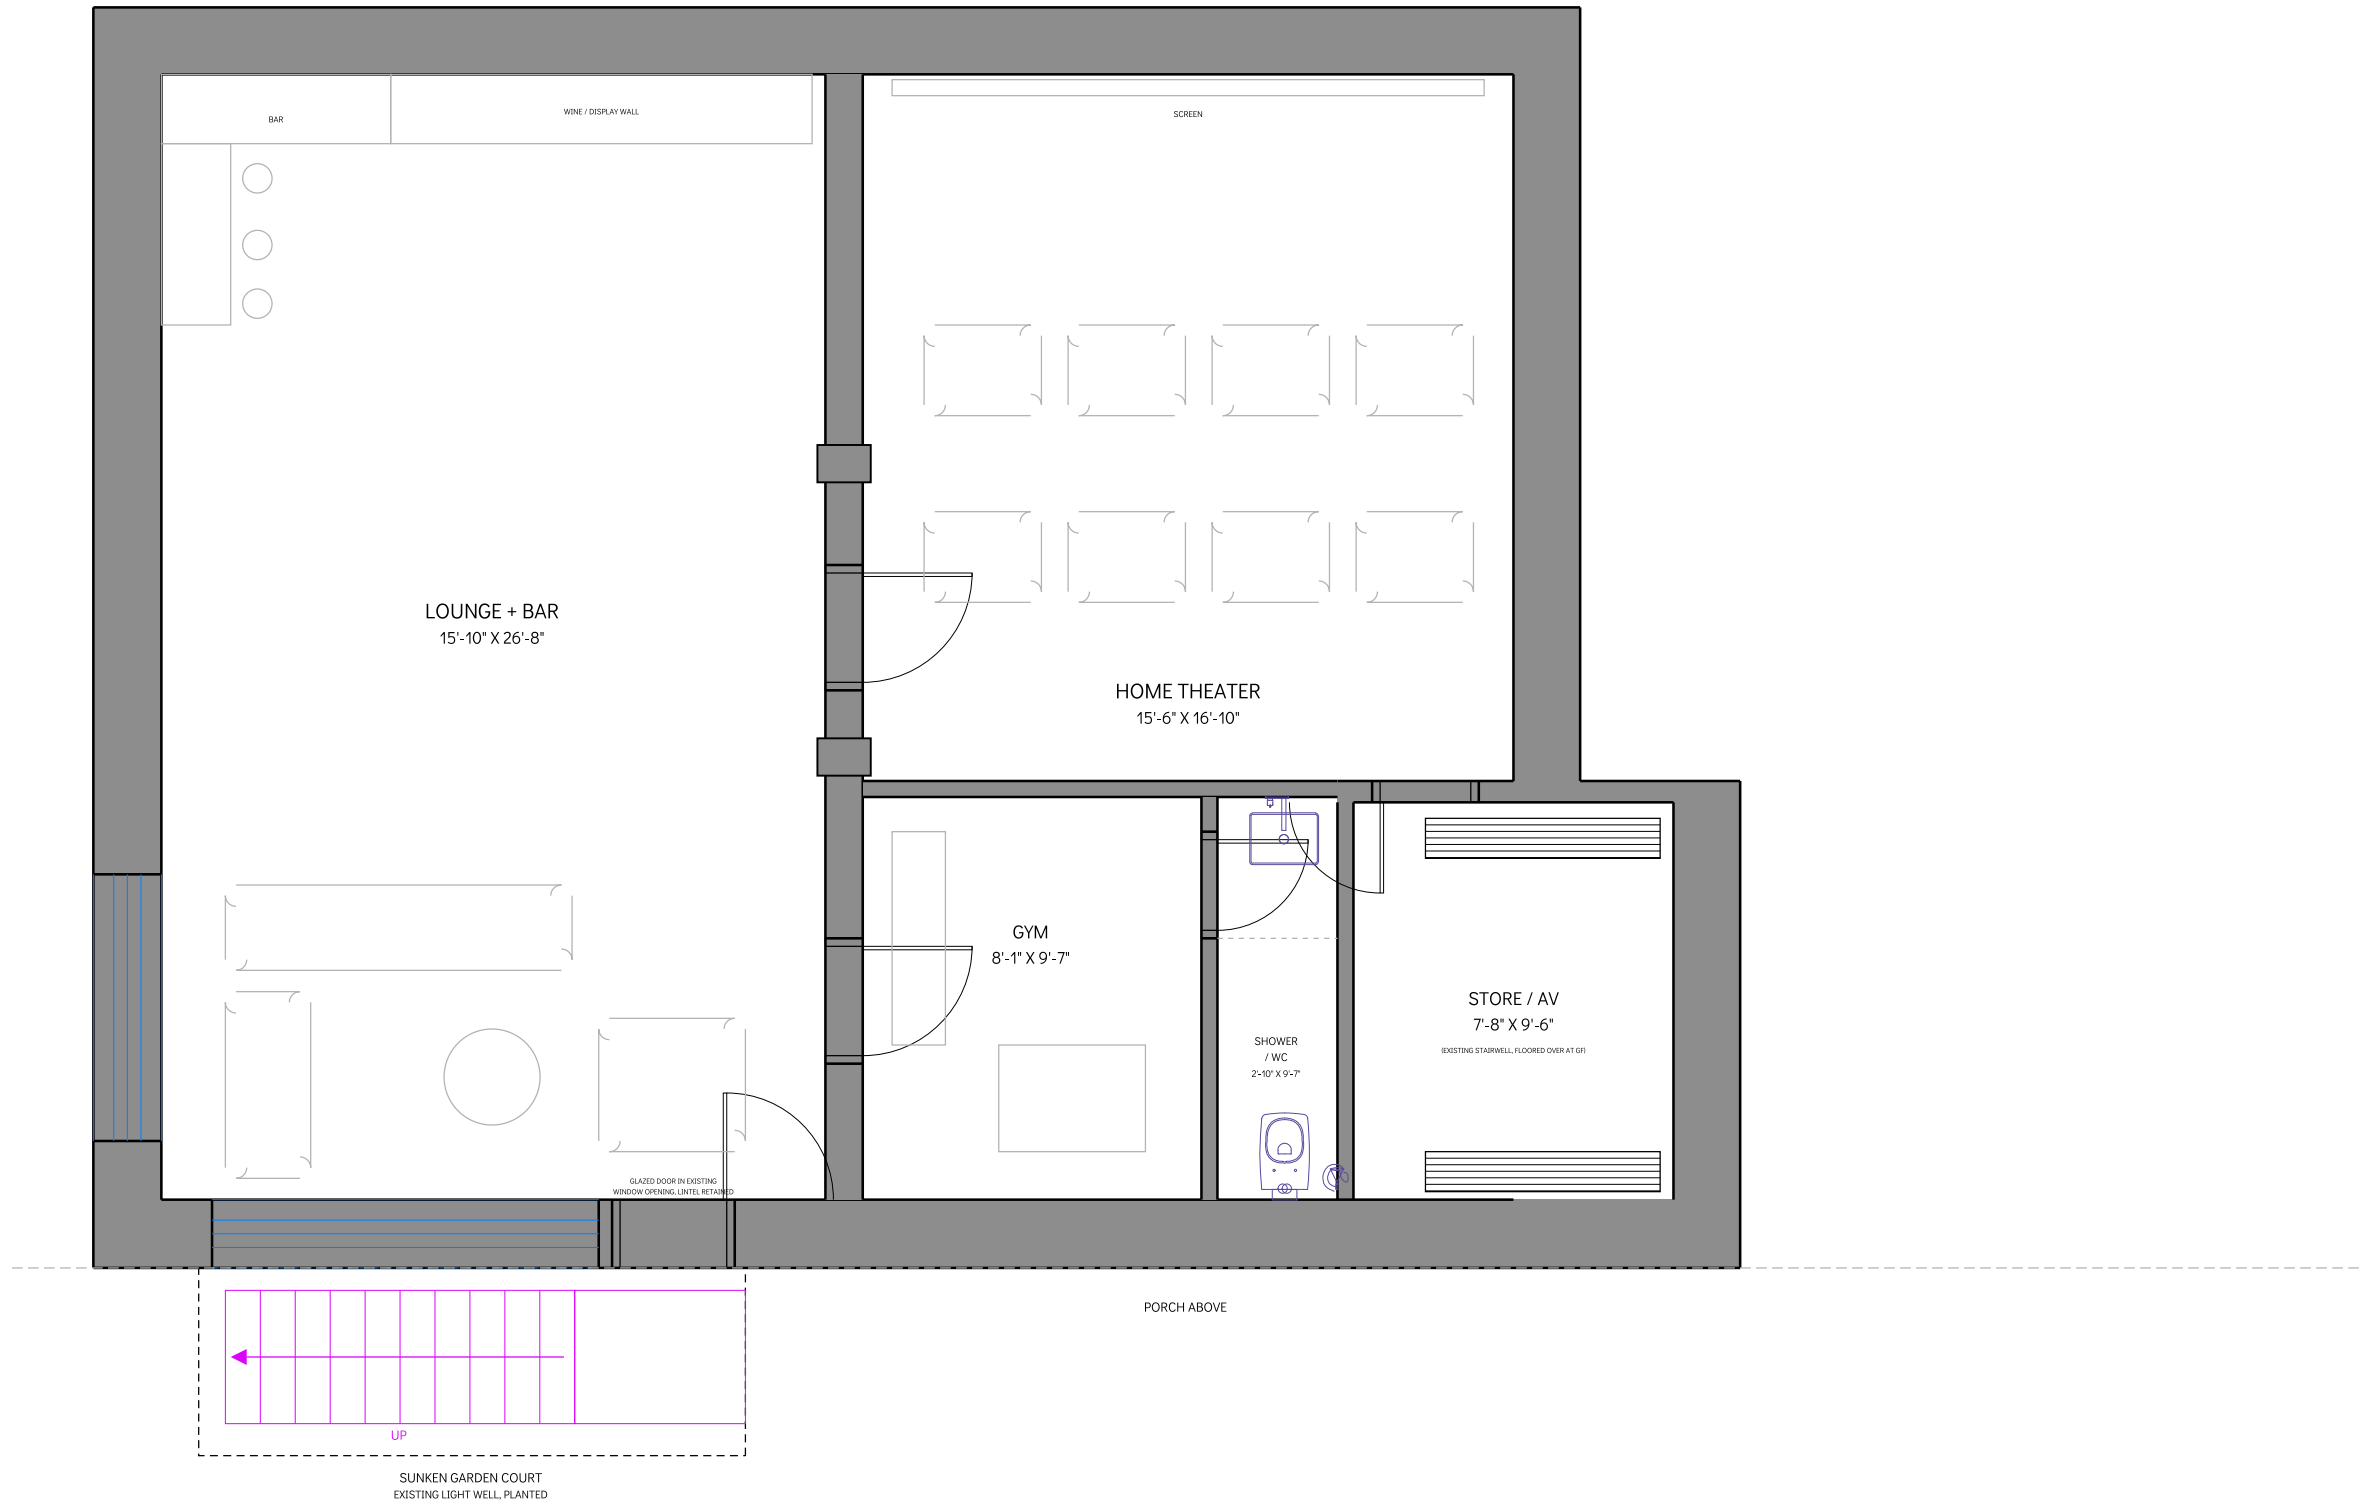

- NOTES (BASEMENT):
- Existing stairwell to be floored over or ground floor level; the well below becomes the store.
 - Existing north window converted to a glazed door: sill masonry removed, existing lintel retained.
 - New external stair inside the existing sunken light well, approx. 10 risers, 3'-6" wide, with canopy and floor trap.
 - Existing ceiling height 8'-6". Existing RCC columns and hidden beam on the centre line are retained; theater partition is non-load-bearing.
 - No new opening in the ground floor slab. Existing basement windows and walls otherwise unchanged.

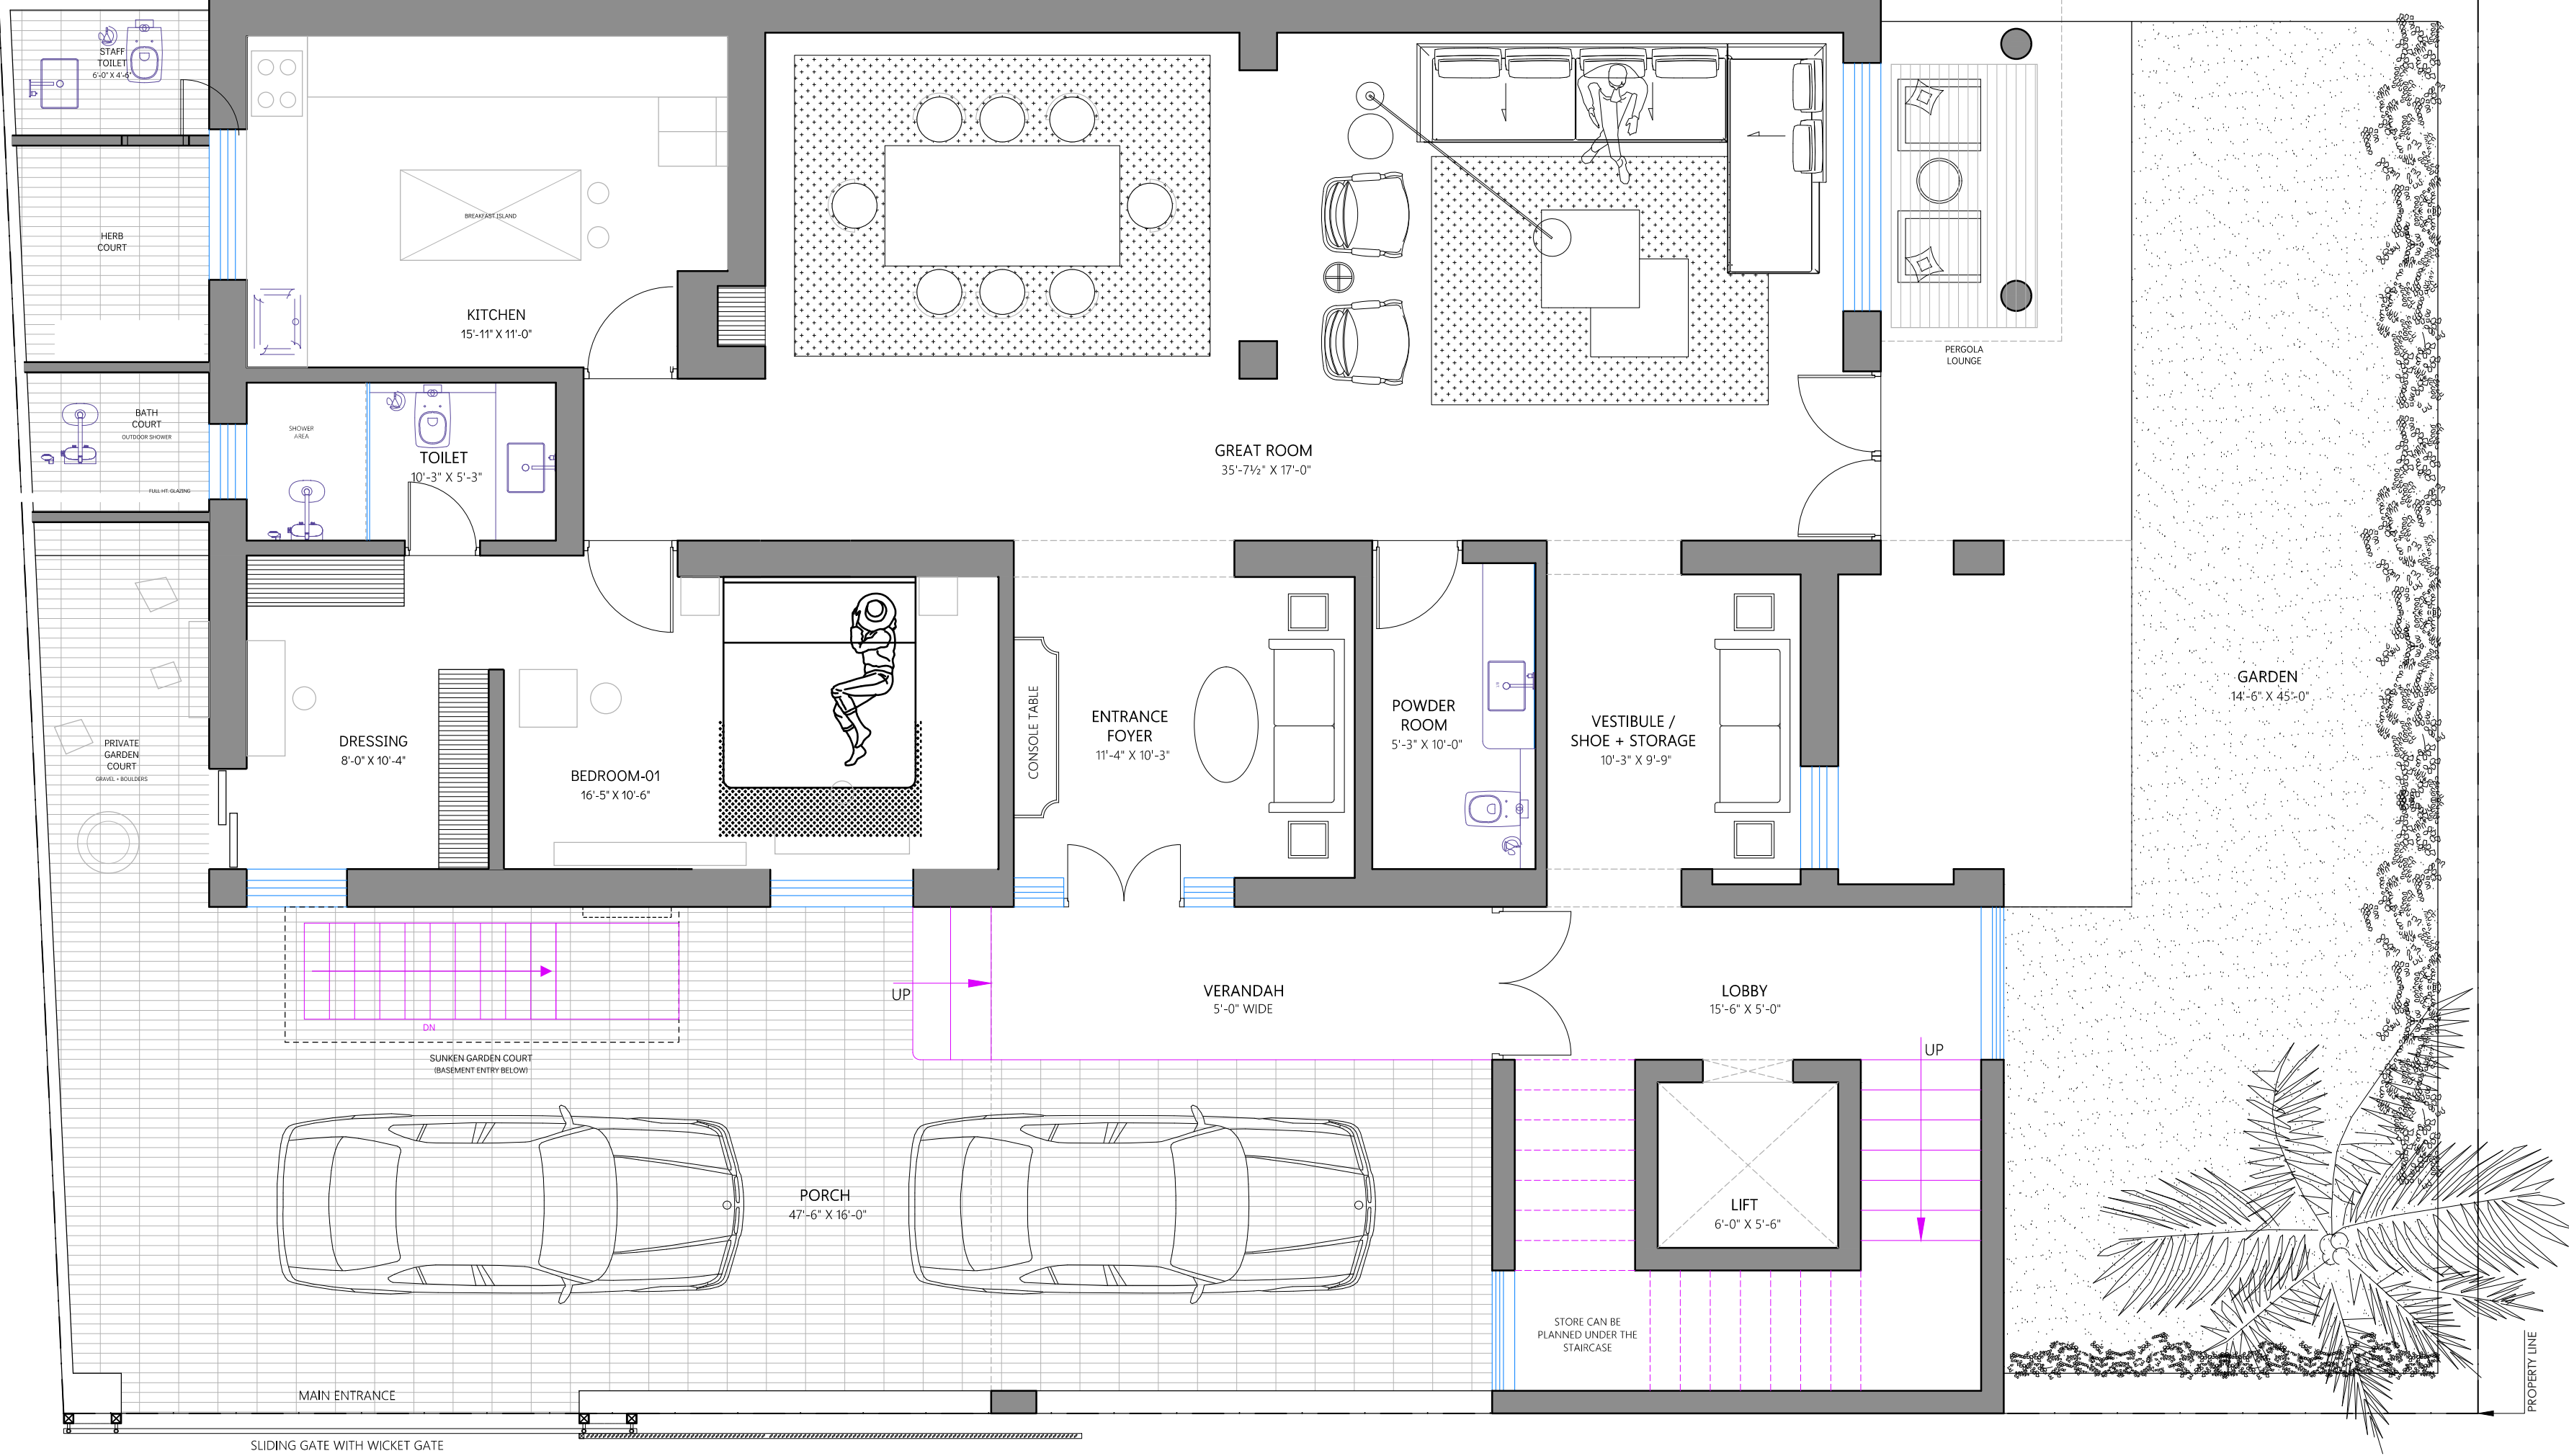

- NOTES:
1. Read this drawing along with relevant architectural, structural or service drawings.
 2. Do not scale; drawing should be read only.
 3. Any discrepancy to be brought to the notice of the architect before commencement of work.
 4. This drawing is a property of Ar. Akash Purohit and shall not be used or reproduced in any manner without the permission of the architects.

PROJECT:
17- CHANDRA PATH

SHEET TITLE:
**GROUND FLOOR -
RENOVATION LAYOUT**

DRAWING NO:
GF-PP-01

DEALT BY:
KAPIL

CHECKED BY:
AKASH


SCALE:
N.T.S.

DATE:
15-09-2026

FILE PATH:

studio sqft


AR. AKASH PUROHIT
ar.akashpurohit@gmail.com
9784784226

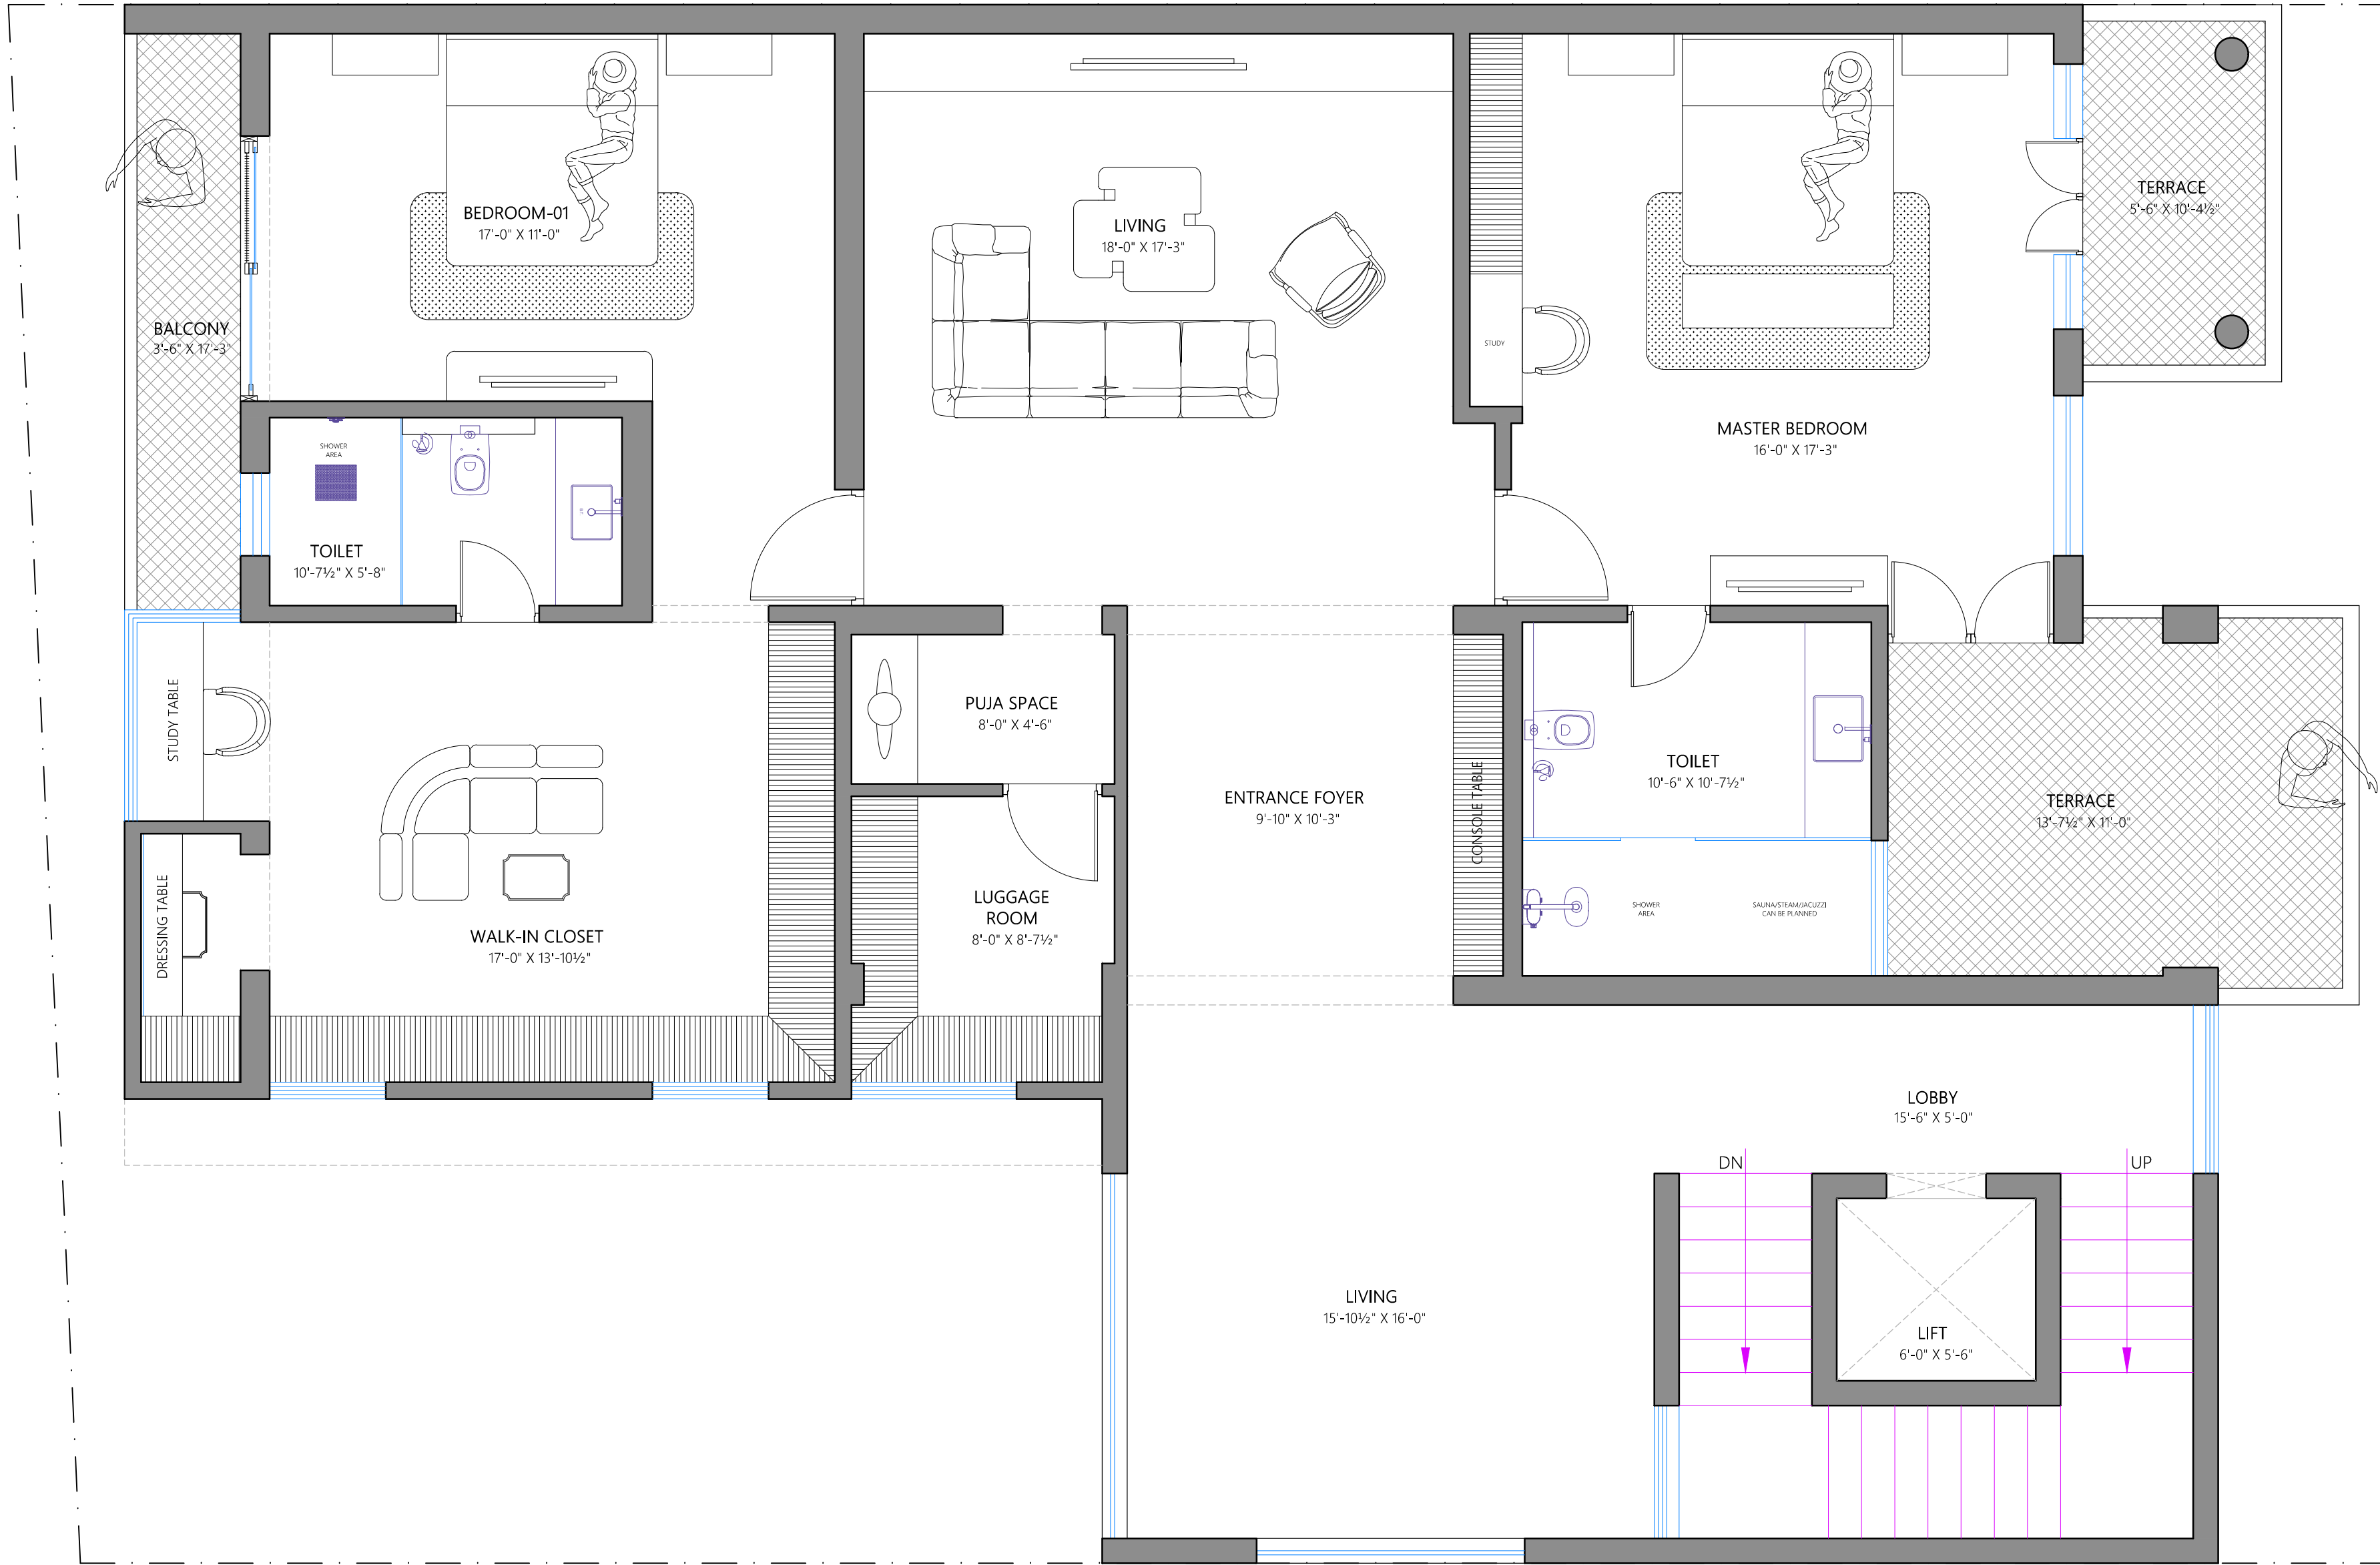

- NOTES:
1. Read this drawing along with relevant architectural, structural or service drawings.
 2. Do not scale; drawing should be read only.
 3. Any discrepancy to be brought to the notice of the architect before commencement of work.
 4. This drawing is a property of Ar. Akash Purohit and shall not be used or reproduced in any manner without the permission of the architects.

PROJECT:
17- CHANDRA PATH

SHEET TITLE:
**FIRST FLOOR -
RENOVATION LAYOUT**

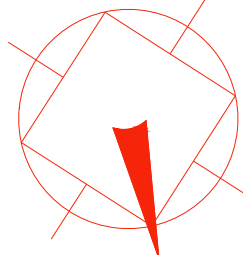

DRAWING NO:
FF-PP-01

DEALT BY:
KAPIL

CHECKED BY:
AKASH


SCALE:
N.T.S.

DATE:
15-09-2026

FILE PATH:

studio sqft


AR. AKASH PUROHIT
ar.akashpurohit@gmail.com
9784784226

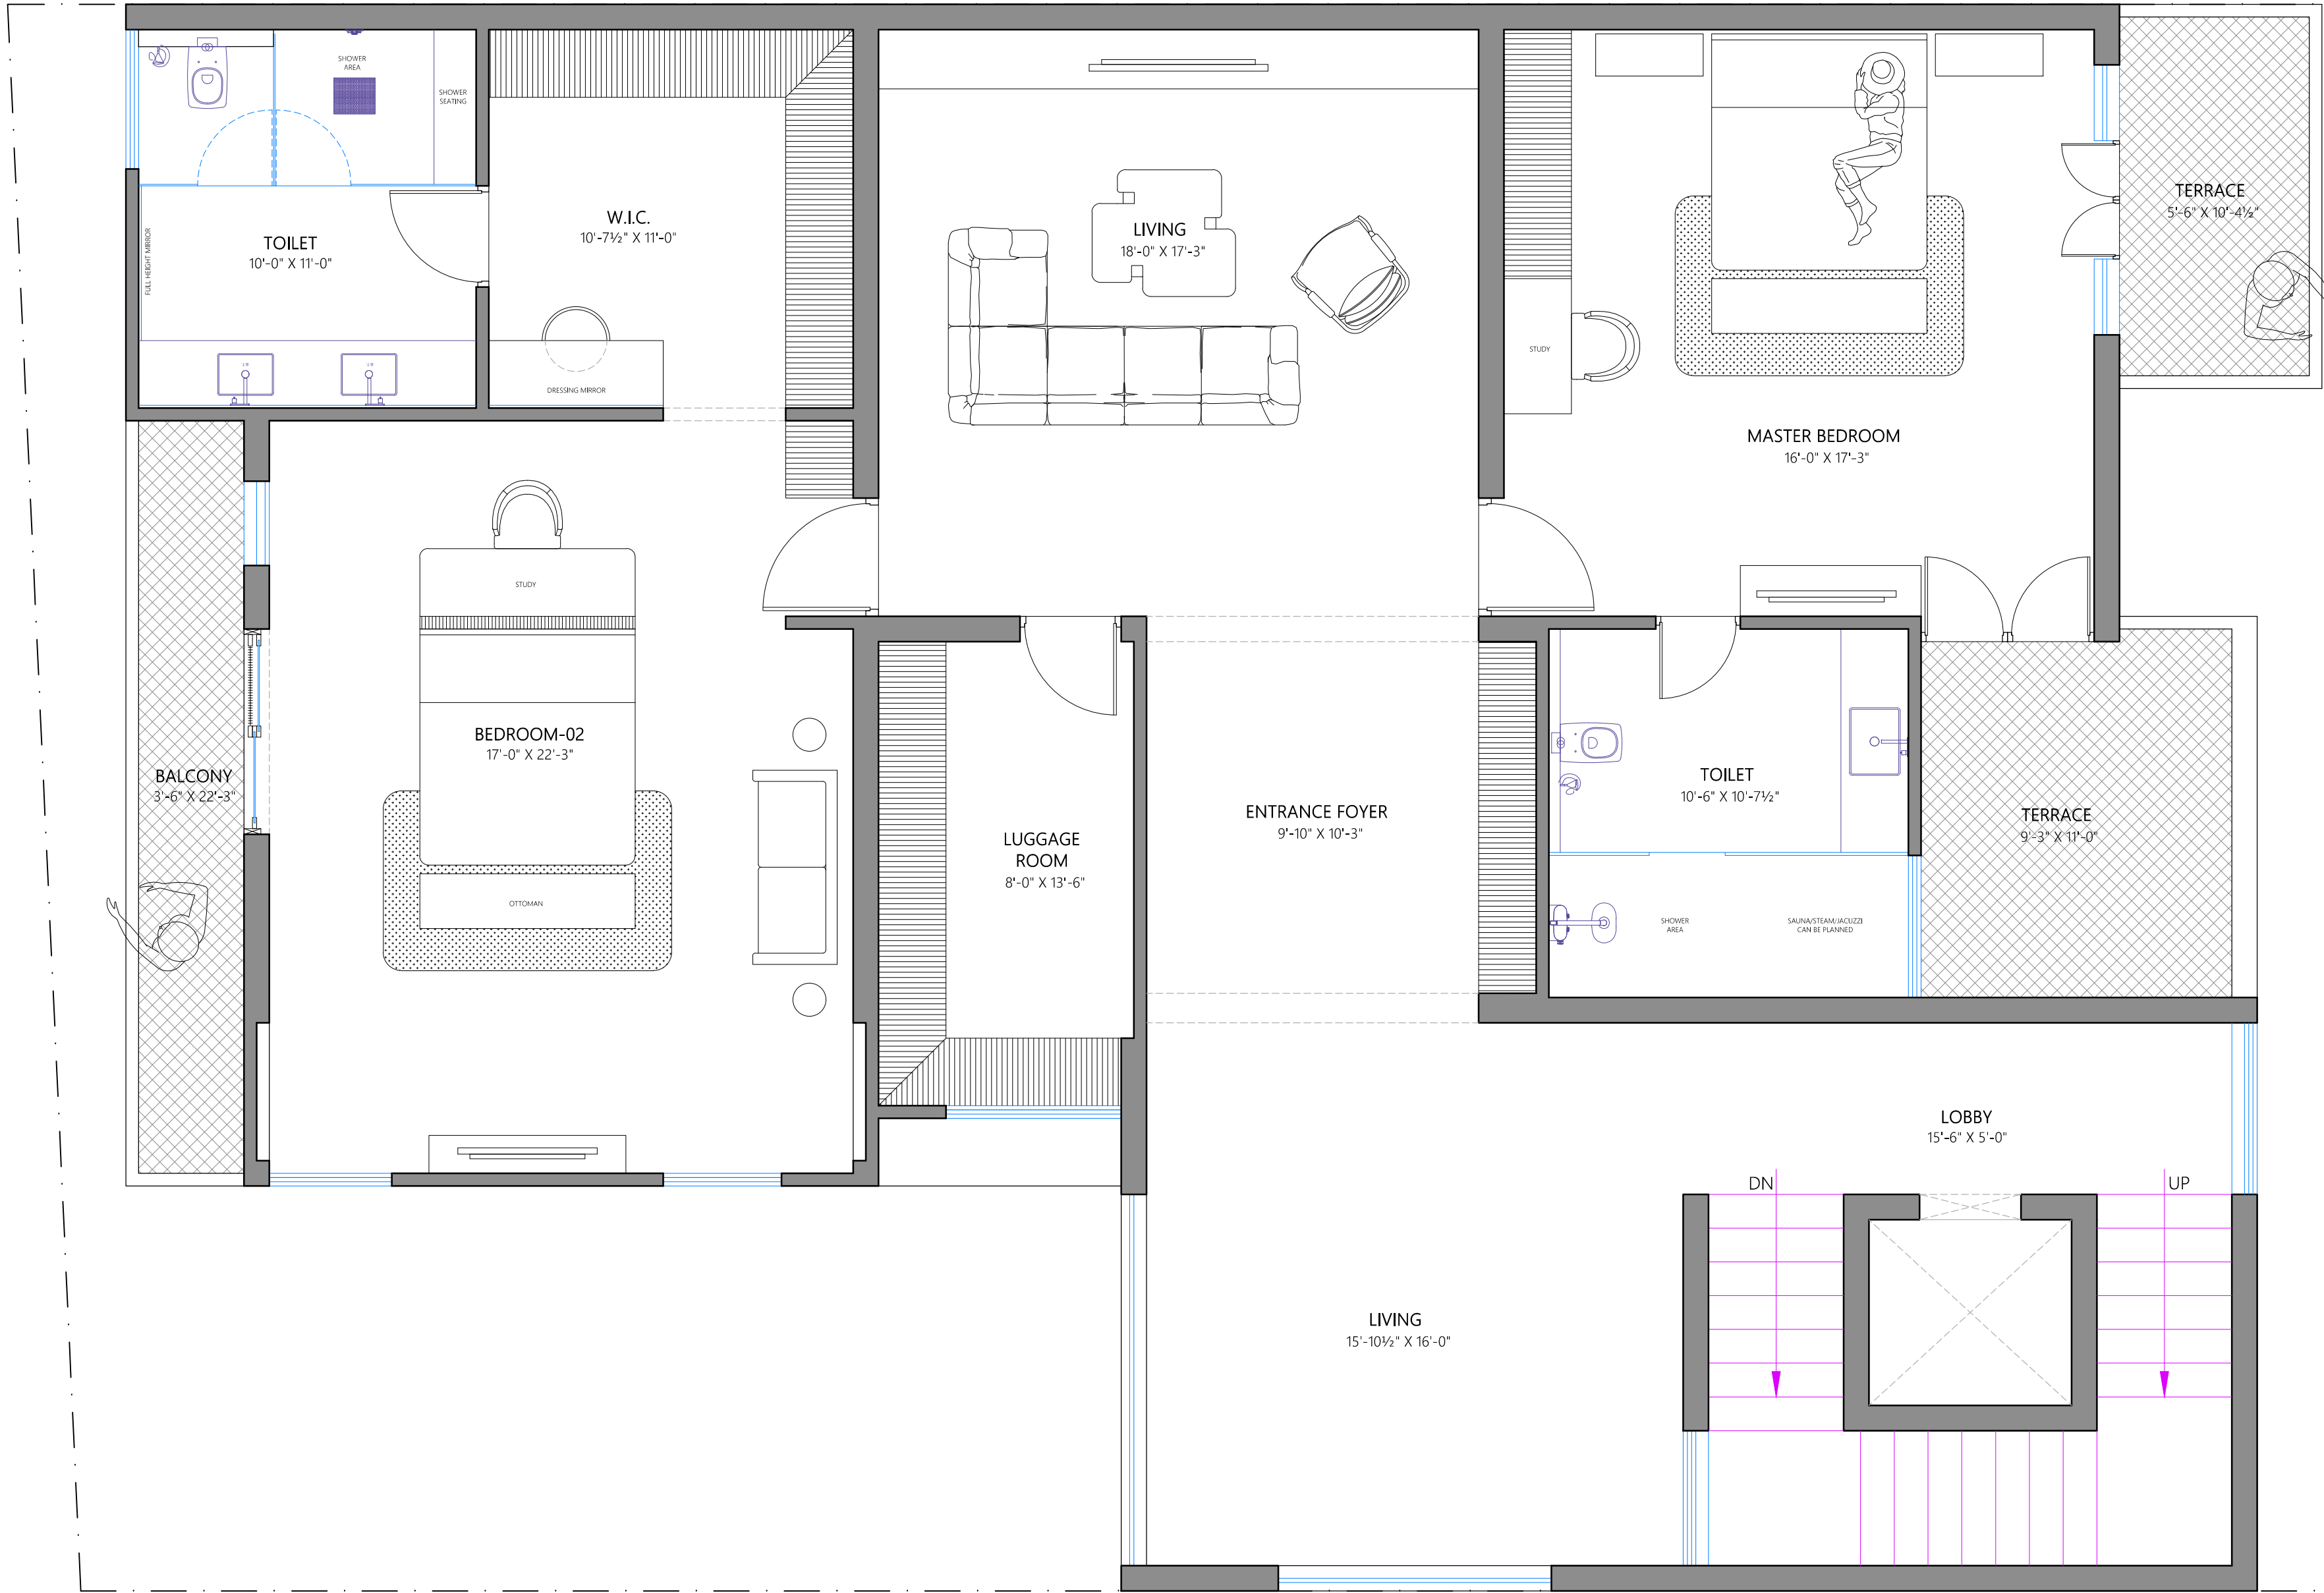

- NOTES:
1. Read this drawing along with relevant architectural, structural or service drawings.
 2. Do not scale; drawing should be read only.
 3. Any discrepancy to be brought to the notice of the architect before commencement of work.
 4. This drawing is a property of Ar. Akash Purohit and shall not be used or reproduced in any manner without the permission of the architects.

PROJECT:
17- CHANDRA PATH

SHEET TITLE:
SECOND FLOOR- LAYOUT

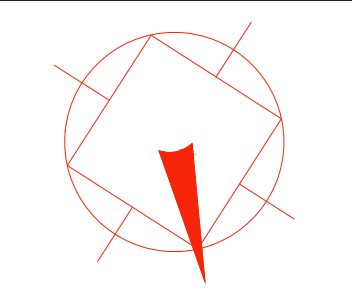

DRAWING NO:
SF-PP-01

DEALT BY:
KAPIL

CHECKED BY:
AKASH

SCALE:
N.T.S.

DATE:
15-09-2026

FILE PATH:

studio sqft

AR. AKASH PUROHIT
ar.akashpurohit@gmail.com
9784784226