

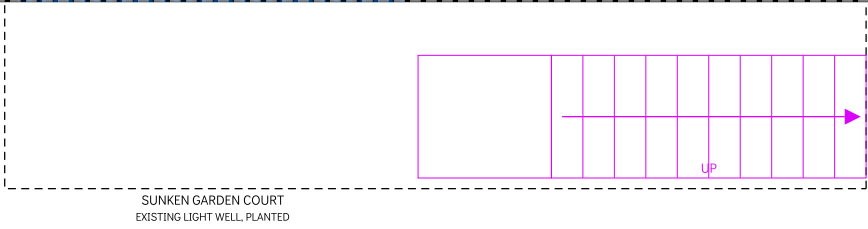


BASEMENT -  
RENOVATION LAYOUT

BF-PP-01

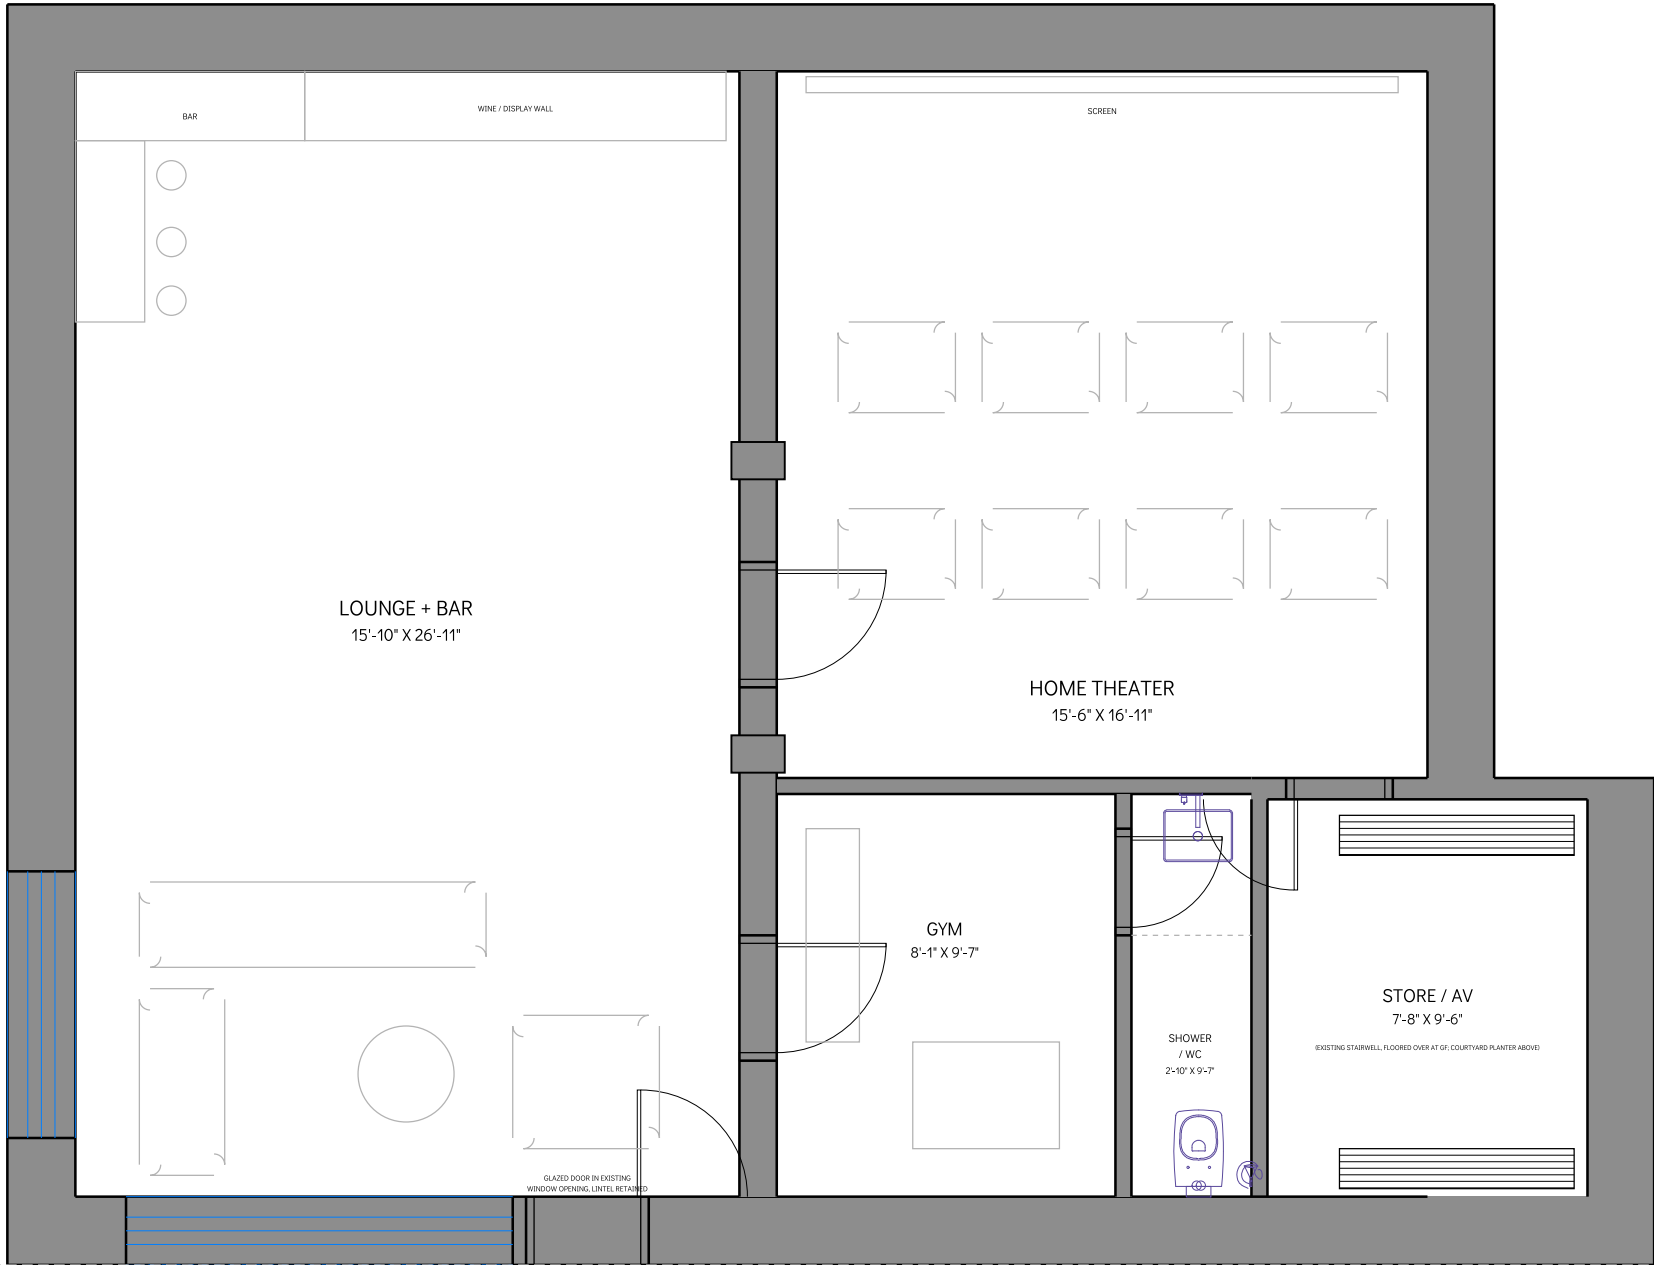


- NOTES (BASEMENT):
- Existing stairwell floored over at ground floor level; the well below is the store / AV room; the courtyard planter above it is waterproofed. The Brahmashan above stays open.
  - Basement entry by the stair in the west part of the existing north light well (north padas 3-4, outside the Brahmashan and the north-east); north window opening converted to a glazed door, sill masonry removed, lintel retained.
  - The servant room is at grade on the east side (see GF-PP-01), not at this level.
  - Existing ceiling height 8'-6". Existing RCC columns and hidden beam on the centre line are retained; theater partition is non-load-bearing.
  - No new opening in the ground floor slab. Existing basement windows and walls otherwise unchanged.

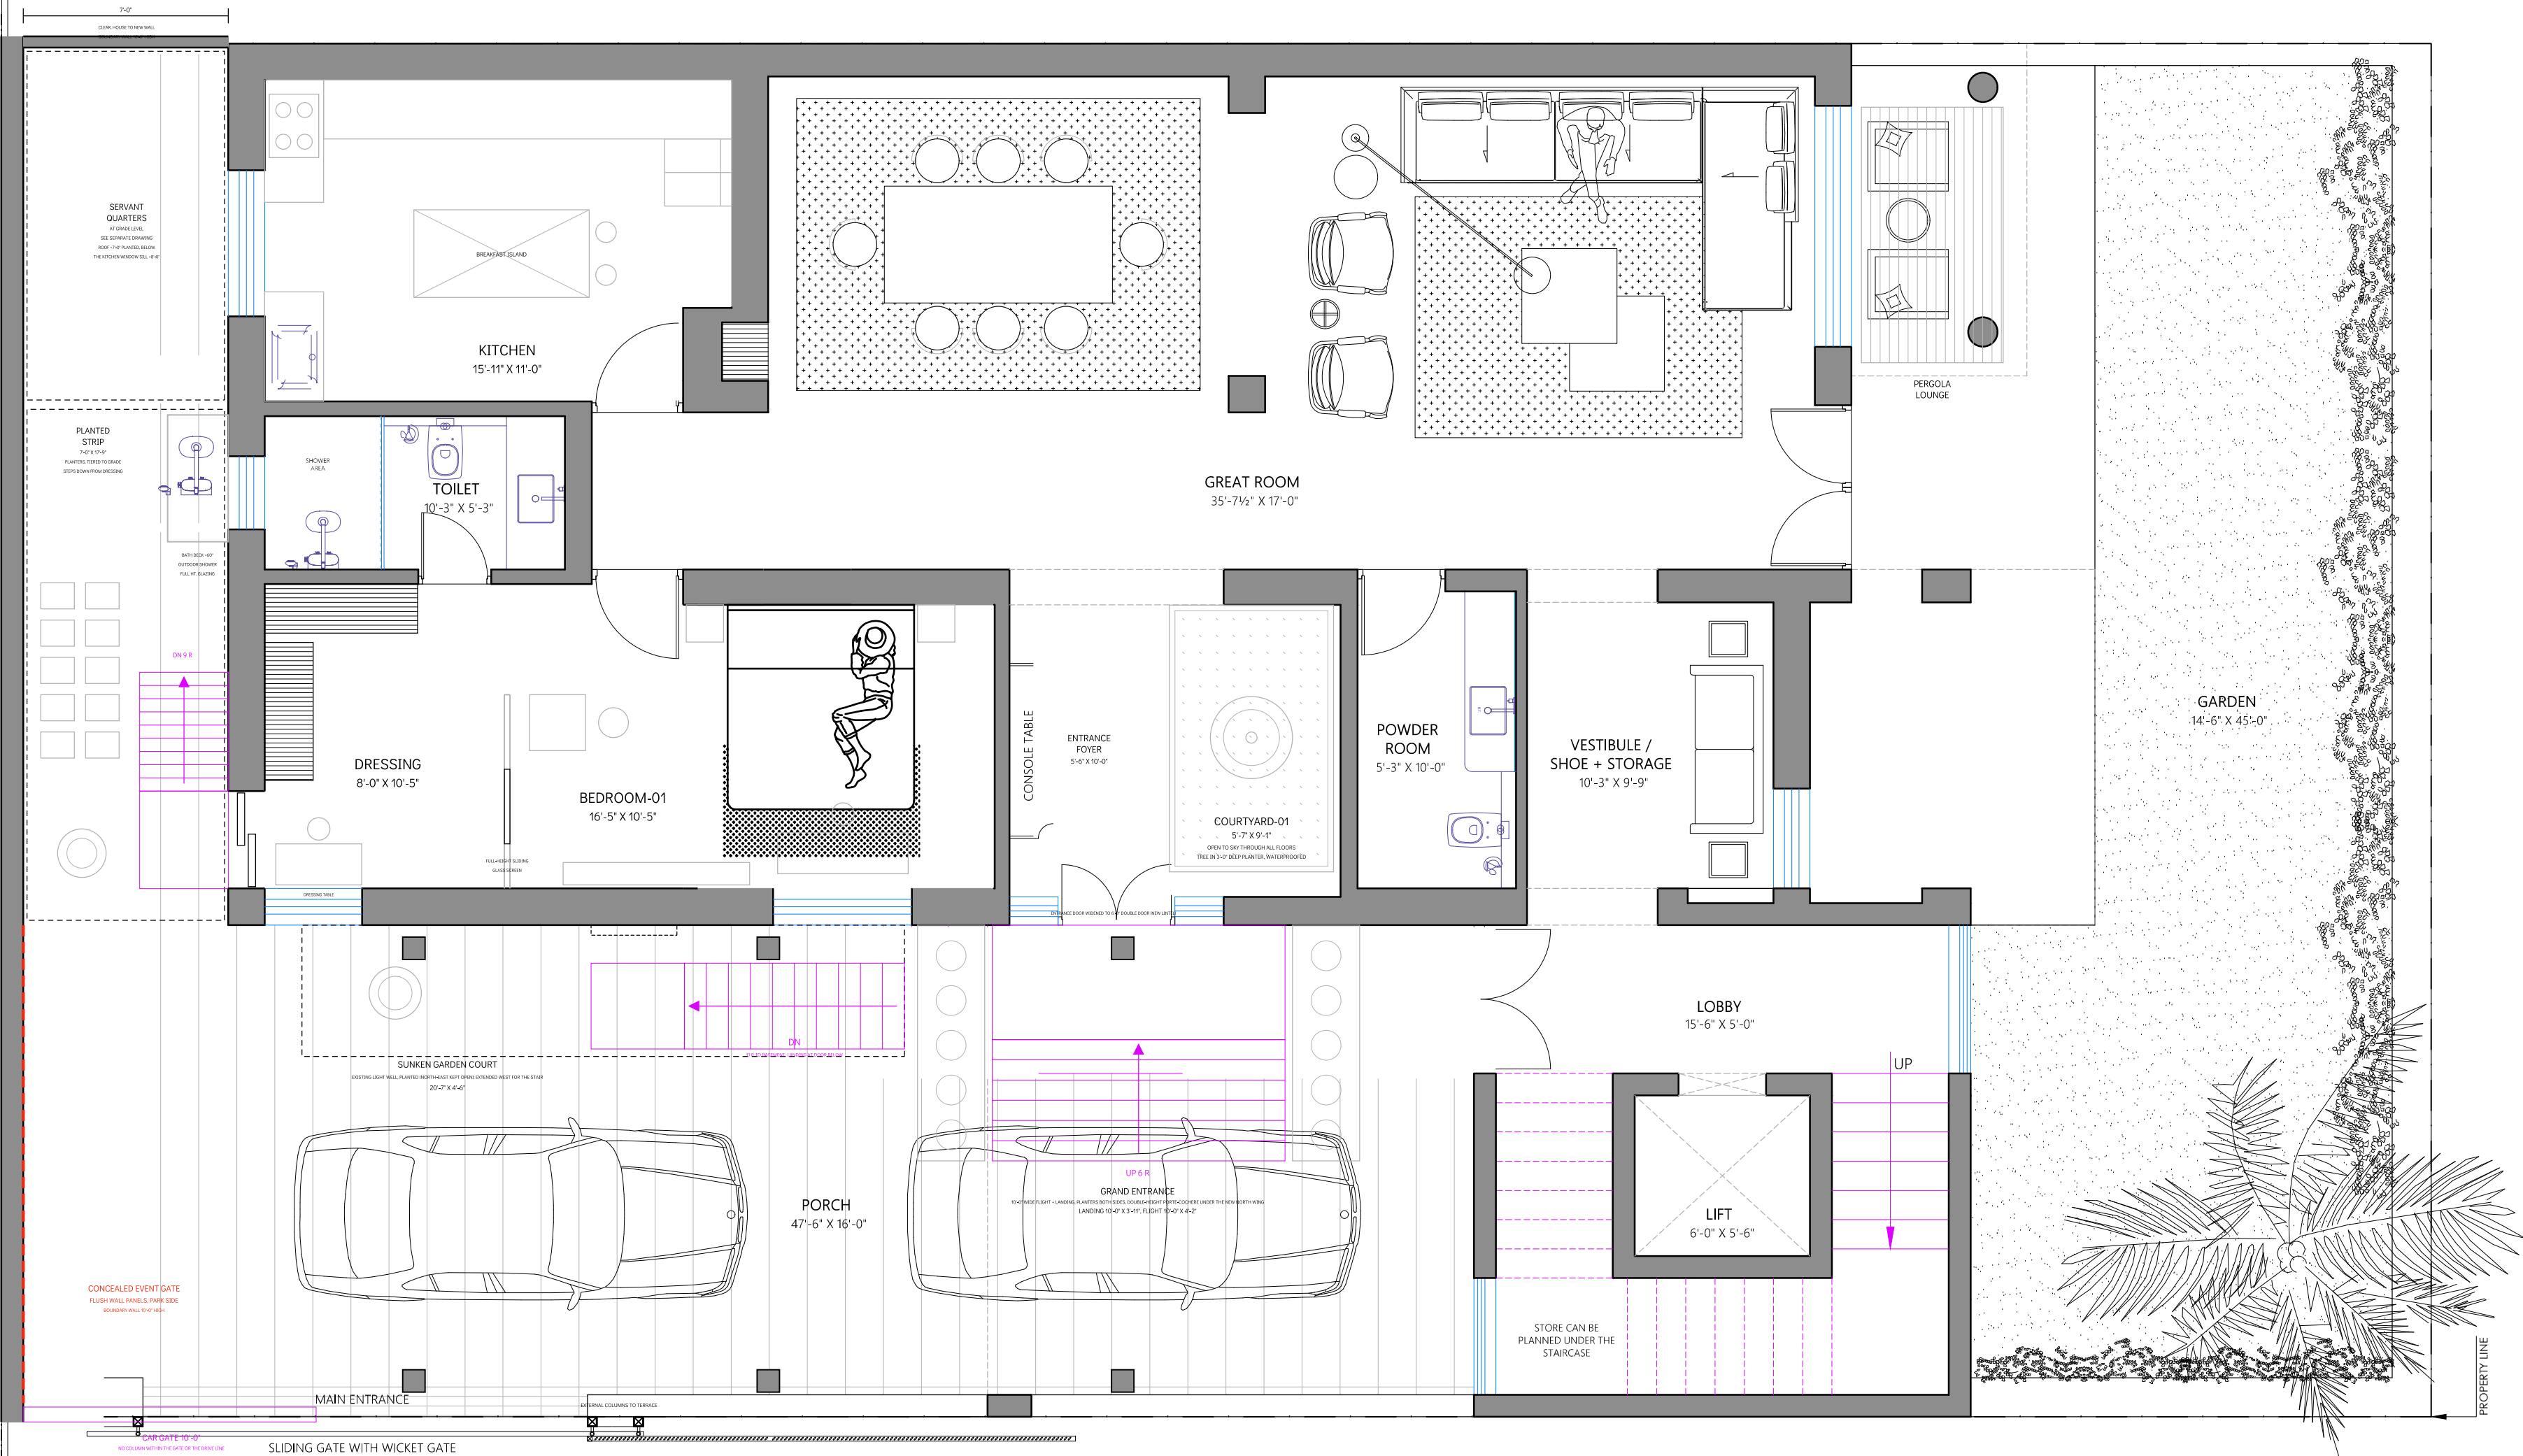

- NOTES:
1. Read this drawing along with relevant architectural, structural or service drawings.
  2. Do not scale; drawing should be read only.
  3. Any discrepancy to be brought to the notice of the architect before commencement of work.
  4. This drawing is a property of Ar. Akash Purohit and shall not be used or reproduced in any manner without the permission of the architects.

PROJECT:  
17- CHANDRA PATH

SHEET TITLE:  
**GROUND FLOOR -  
RENOVATION LAYOUT**

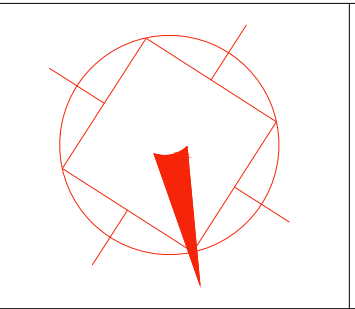

DRAWING NO:  
GF-PP-01

DEALT BY:  
KAPIL

CHECKED BY:  
AKASH

SCALE:  
N.T.S.


DATE:  
15-09-2026

FILE PATH:

studio sqft

AR. AKASH PUROHIT  
ar.akashpurohit@gmail.com  
9784784226


NOTES (REVISION R3):  
A. EAST SIDE: 7'-0" CLEAR BETWEEN THE HOUSE AND THE NEW STRAIGHT 10'-0" HIGH BOUNDARY WALL (9" THICK, FULL LENGTH, NO OPENINGS TO THE PARK EXCEPT THE EVENT GATE; CAR GATE 10'-0" AT THE EAST END OF THE NORTH BOUNDARY.  
B. CONCEALED EVENT GATE IN THE EAST BOUNDARY WALL FROM THE HOUSE CORNER TO THE FRONT BOUNDARY: FLUSH WALL-FINISHED PANELS ON CONCEALED PIVOTS, OPENED ONLY FOR EVENTS.  
C. BEDROOM-01 DAYLIGHT: THE DRESSING-BEDROOM PARTITION IS A FULL-HEIGHT SLIDING GLASS SCREEN, NO WARDROBE ON IT, SO EAST LIGHT FROM THE DRESSING DOOR REACHES THE BED; WARDROBES ON THE DRESSING'S SOUTH AND EAST WALLS. COURTYARD-01 IN THE EXISTING STAIRWELL SHAFT, OPEN TO SKY THROUGH ALL FLOORS; THE CENTRE IS KEPT OPEN AND FREE OF STAIRS. ENTRANCE STEPS ARE A COMPACT 6-RISER FLIGHT OUTSIDE THE EXISTING DOOR; BASEMENT STAIR IN THE WEST PART OF THE EXISTING LIGHT WELL. LIFT GIVES THE STEP-FREE ROUTE.  
D. EAST STRIP: SERVANT QUARTERS AT GRADE LEVEL ARE COVERED BY A SEPARATE DRAWING AND ARE NOT SHOWN HERE. THEIR ROOF AT 7'-0" PLANTED SITS BELOW THE KITCHEN EAST WINDOW SILL (4'-0" 3'-0" ABOVE THE KITCHEN FLOOR) SO THE KITCHEN KEEPS ITS WINDOW, CHIMNEY FLUE AND EXHAUST. AT GROUND FLOOR LEVEL, THE STRIP CARRIES A BATH DECK AT +60" WITH THE OUTDOOR SHOWER, TIERED PLANTERS, AND STEPS DOWN FROM THE DRESSING.  
E. SERVICE WING ROOFED AT 7'-6" WITH A PLANTER PARAPET, BATHROOM EAST WINDOW IN OBSCURE GLASS. GRAND ENTRANCE: 10'-0" FLIGHT CENTRED ON THE WIDENED FRONT DOOR NORTH PADA 51, BELOW THE BRAHMASTHAN LINE. BASEMENT STAIR IN THE NORTH LIGHT WELL. THE WHOLE BLOCK OVER THE PORCH LOBBY, LIFT, MAIN STAIR, UPPER LIVING ROOMS IS DEMOLISHED AND REBUILT ON THE NEW COLUMN GRID; LIFT AND MAIN STAIR STAY IN THE NORTH-WEST.  
F. ALL ROOM DIMENSIONS ARE CLEAR INTERNAL SIZES TAKEN FROM THE DRAWN WALLS. SHEET ORIENTATION: TOP = SOUTH, BOTTOM = NORTH, LEFT = EAST, RIGHT = WEST.

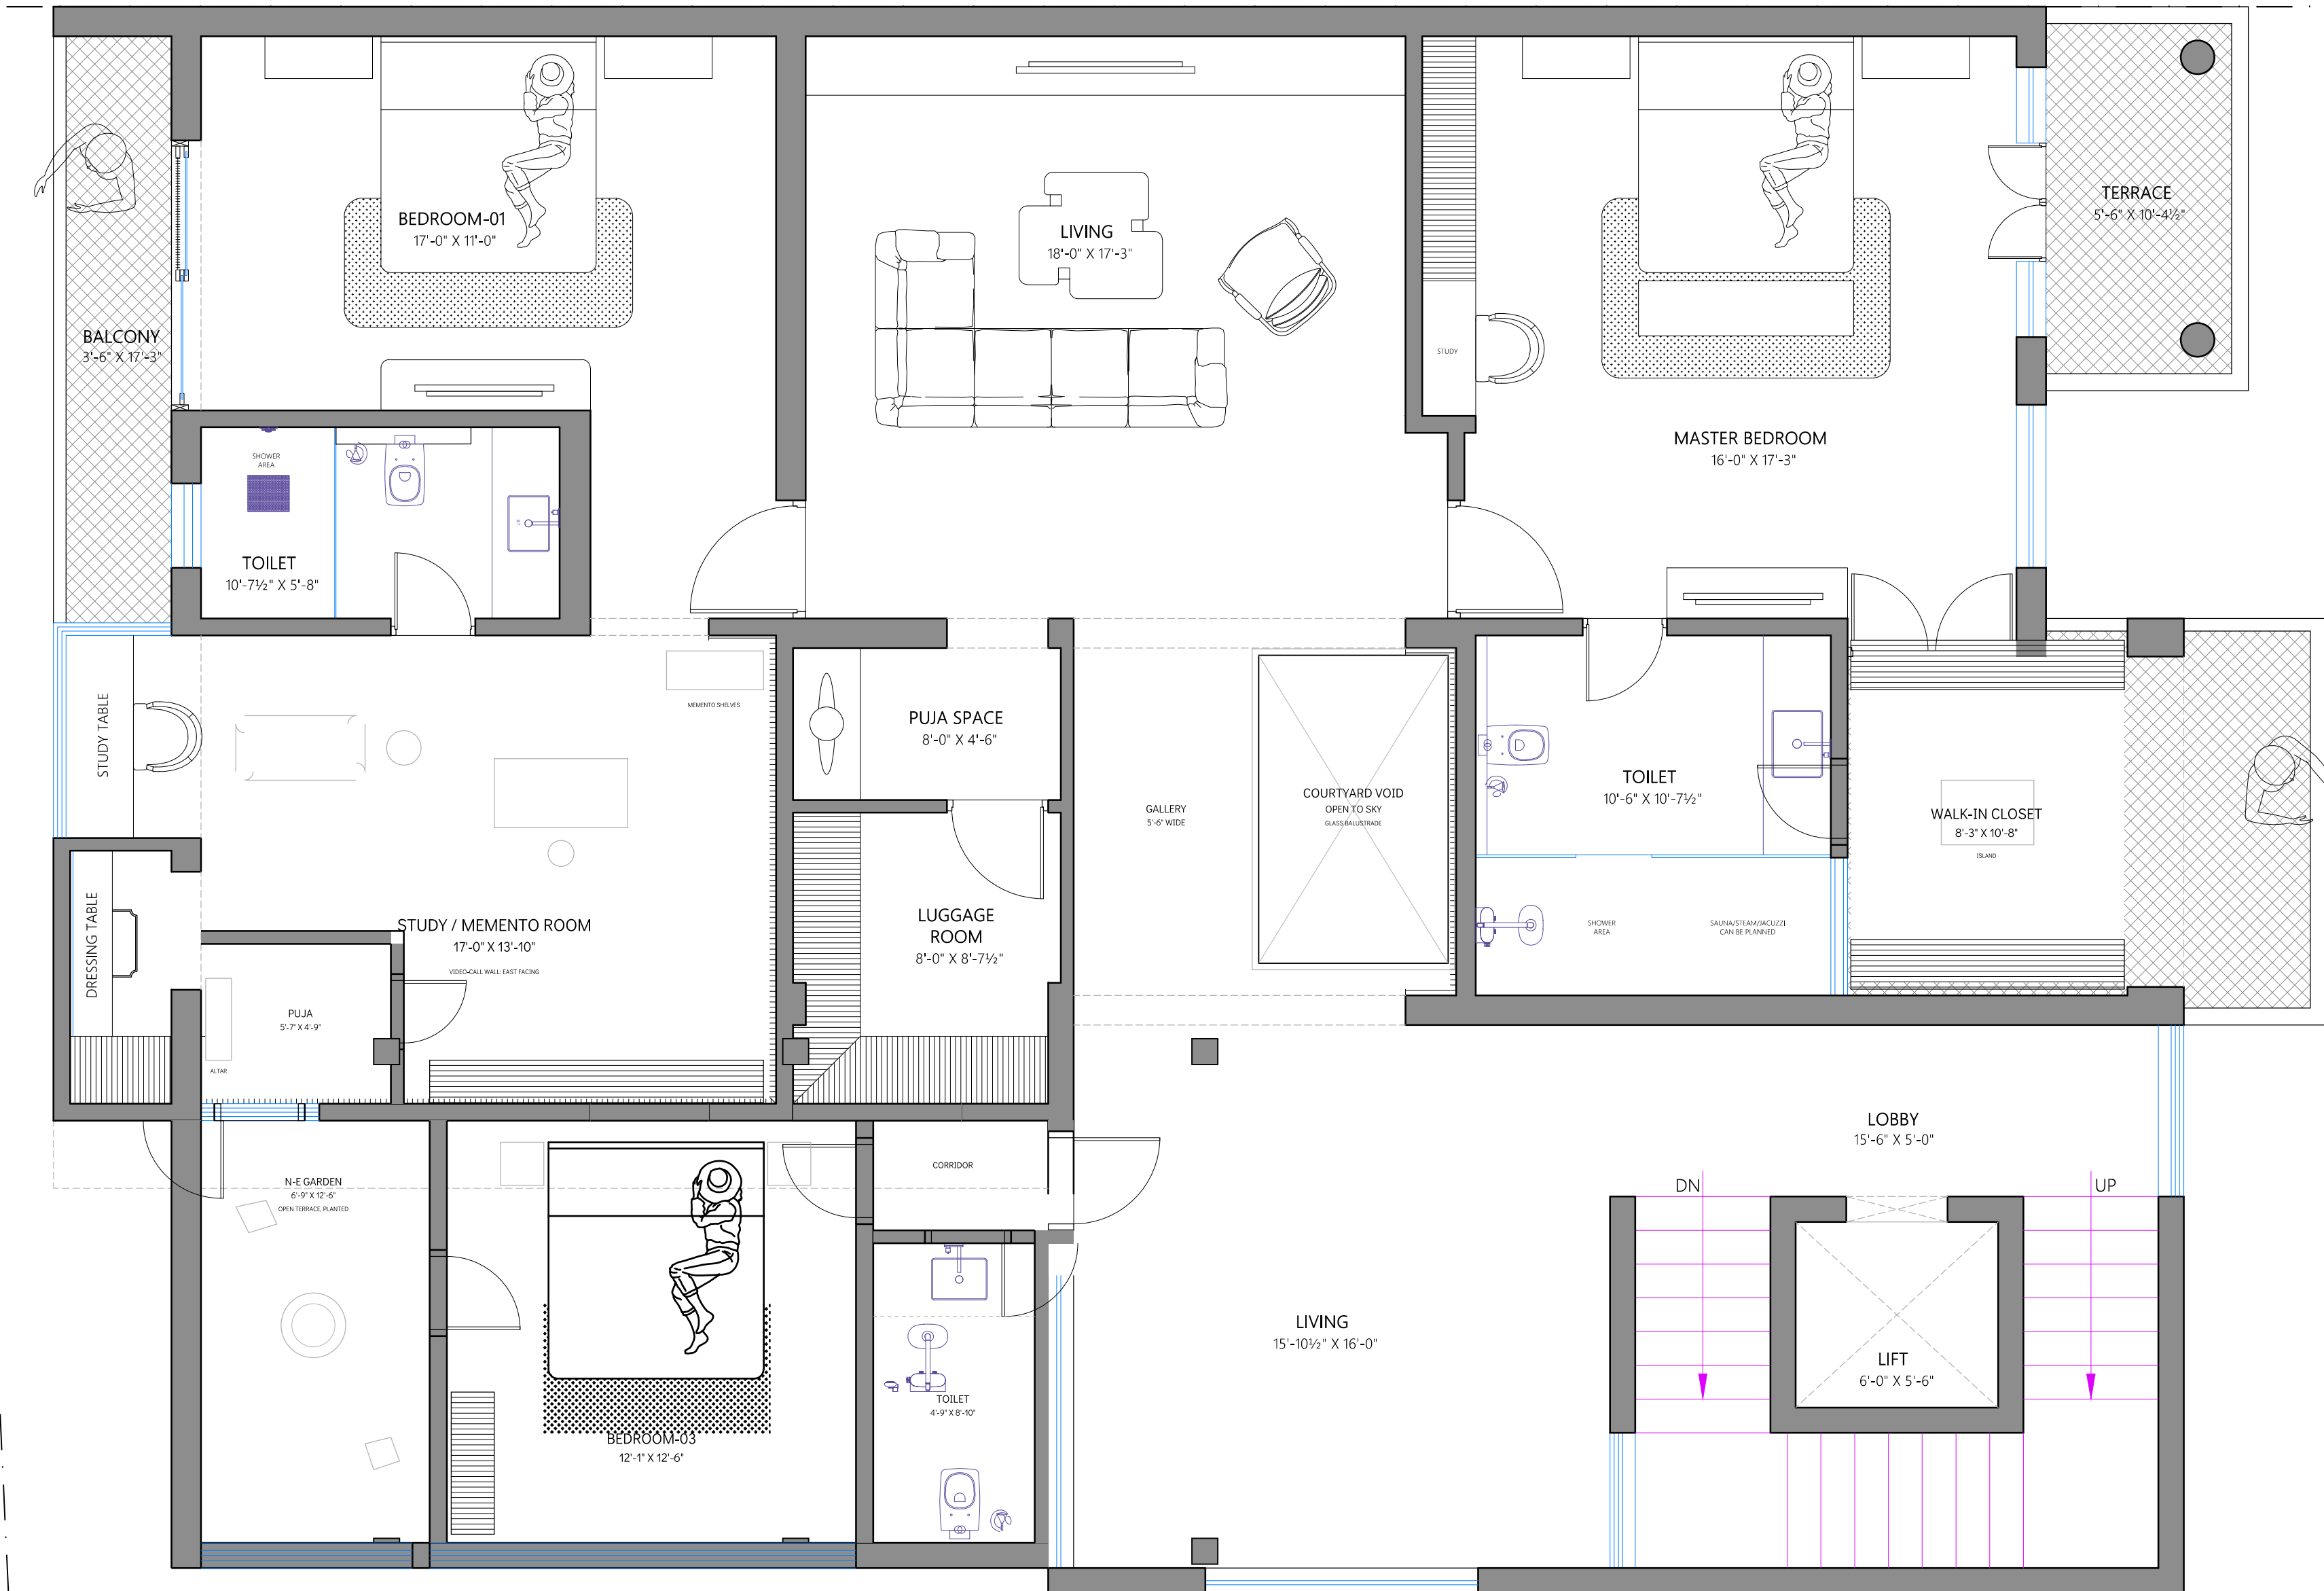

- NOTES:
1. Read this drawing along with relevant architectural, structural or service drawings.
  2. Do not scale; drawing should be read only.
  3. Any discrepancy to be brought to the notice of the architect before commencement of work.
  4. This drawing is a property of Ar. Akash Purohit and shall not be used or reproduced in any manner without the permission of the architects.

PROJECT:  
17- CHANDRA PATH

SHEET TITLE:  
**FIRST FLOOR -  
RENOVATION LAYOUT**

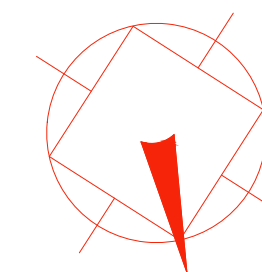

DRAWING NO:  
FF-PP-01

DEALT BY:  
KAPIL

CHECKED BY:  
AKASH

SCALE:  
N.T.S.


DATE:  
15-09-2026

FILE PATH:

**studio sqft**

AR. AKASH PUROHIT  
ar.akashpurohit@gmail.com  
9784784226

- NOTES (FIRST FLOOR, R3):
1. THE BLOCK OVER THE PORCH IS REBUILT FROM SCRATCH ON RCC COLUMNS FROM FOUNDATION TO TERRACE (THREE ON THE PORCH LINE, THREE AT THE BACK AGAINST THE NORTH WALL, NONE WITHIN THE 10'-0" CAR GATE OR THE DRIVE LINE), INDEPENDENT OF THE STONE WALLS; TO STRUCTURAL DESIGN.
  2. FORMER WEST TERRACE ENCLOSED AS MASTER WALK-IN CLOSET (LIGHT PARTITIONS ON EXISTING SLAB); 3. NORTH-EAST ROOM RE-PURPOSED AS STUDY WITH PUJA IN ITS NORTH-EAST CORNER.
  4. COURTYARD VOID WITHIN THE EXISTING STAIRWELL SHAFT; GLASS BALUSTRADE; 5. ROOM DIMENSIONS ARE CLEAR INTERNAL SIZES FROM THE DRAWN WALLS.

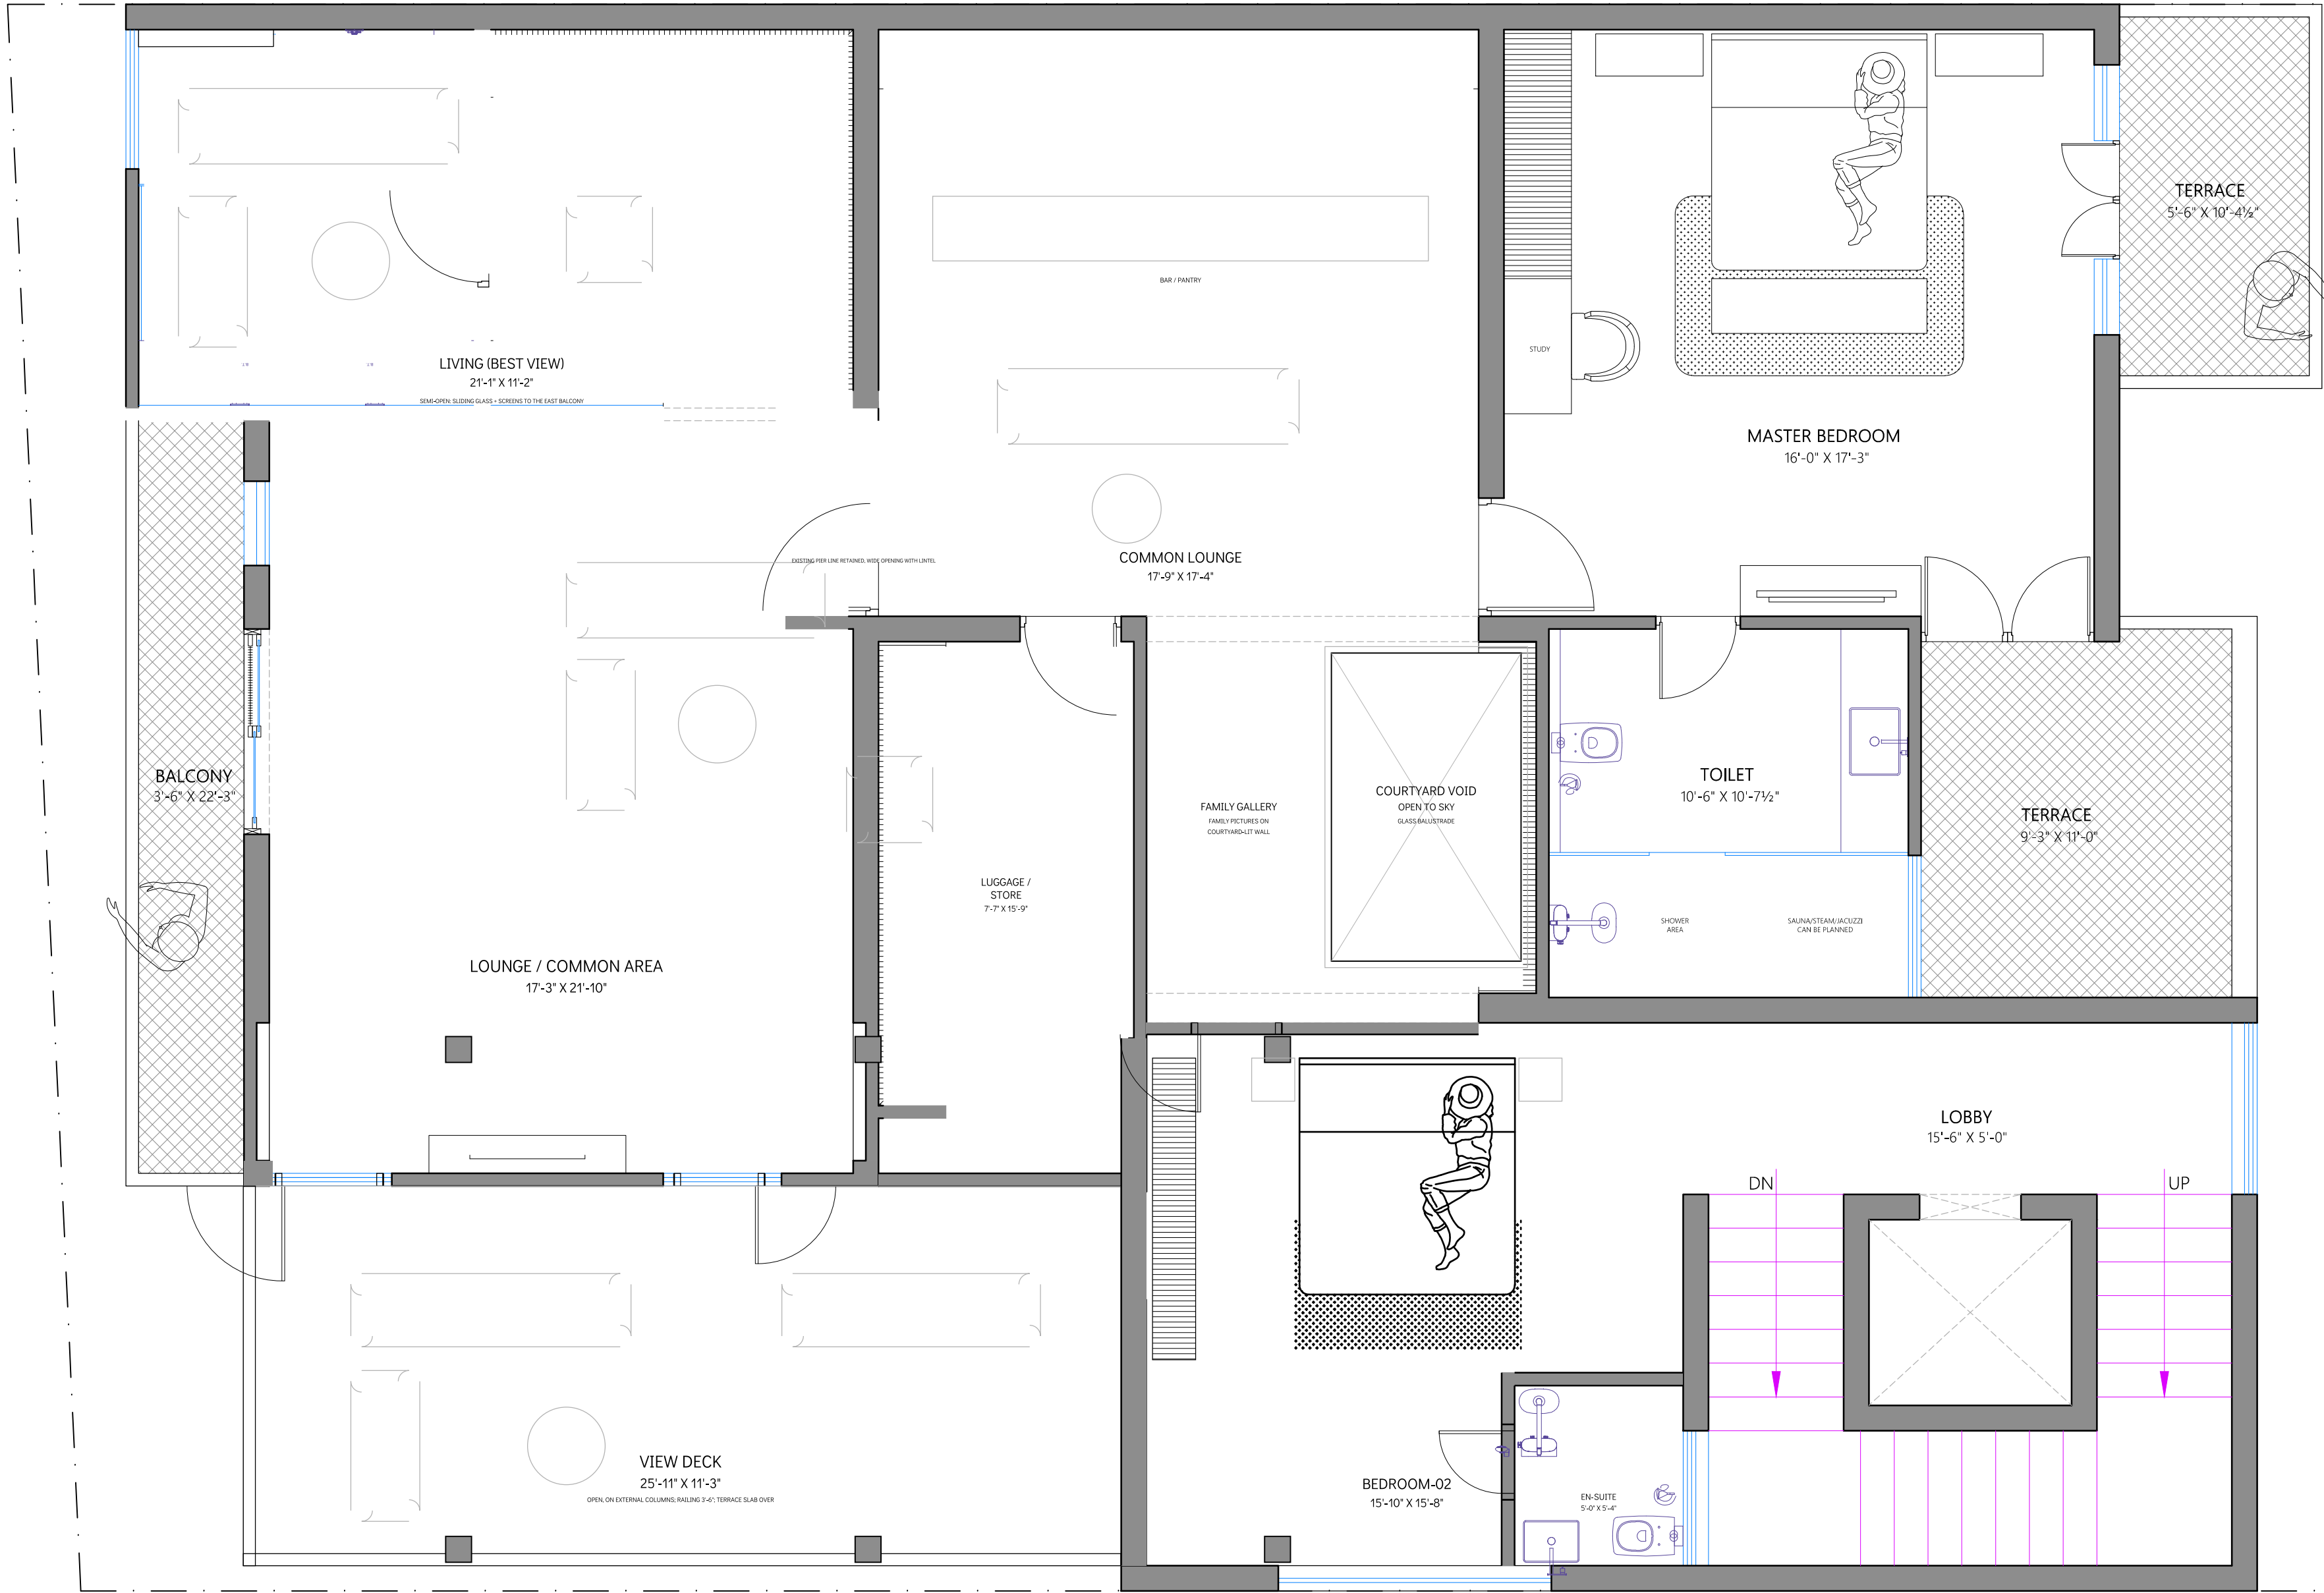


NOTES (SECOND FLOOR, R3):  
1. SOUTH-EAST TOILET, WALK-IN CLOSET AND BEDROOM-02 REMOVED; THE SOUTH-EAST CORNER WITH THE BEST VIEW BECOMES THE LIVING ROOM, THE REST A COMMON LOUNGE. FORMER NORTH WINDOWS BECOME DOORS TO THE GARDEN AND BEDROOM-02, OR ARE INFILLED.  
2. BEDROOM-02 WITH EN-SUITE IN THE FORMER LIVING OVER THE PORCH (NORTH-WEST); THE NEW EAST WING AT THIS LEVEL IS AN OPEN VIEW DECK ON EXTERNAL COLUMNS, NO WALLS. 3. STRUCTURAL WALL LINES RETAINED AS PIERS; OPENINGS WITH LINTELS.  
4. FAMILY GALLERY ALONG THE COURTYARD VOID. 5. ROOM DIMENSIONS ARE CLEAR INTERNAL SIZES FROM THE DRAWN WALLS.

- NOTES:
1. Read this drawing along with relevant architectural, structural or service drawings.
  2. Do not scale; drawing should be read only.
  3. Any discrepancy to be brought to the notice of the architect before commencement of work.
  4. This drawing is a property of Ar. Akash Purohit and shall not be used or reproduced in any manner without the permission of the architects.

PROJECT:  
17- CHANDRA PATH

SHEET TITLE:  
**SECOND FLOOR- LAYOUT**

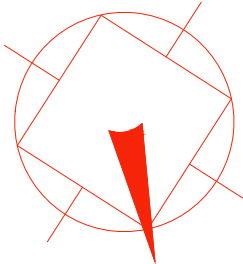

DRAWING NO:  
SF-PP-01

DEALT BY:  
KAPIL

CHECKED BY:  
AKASH

SCALE:  
N.T.S.

DATE:  
15-09-2026


FILE PATH:

**studio sqft**

AR. AKASH PUROHIT  
ar.akashpurohit@gmail.com  
9784784226

TERRACE FLOOR -  
LAYOUT

TF-PP-01

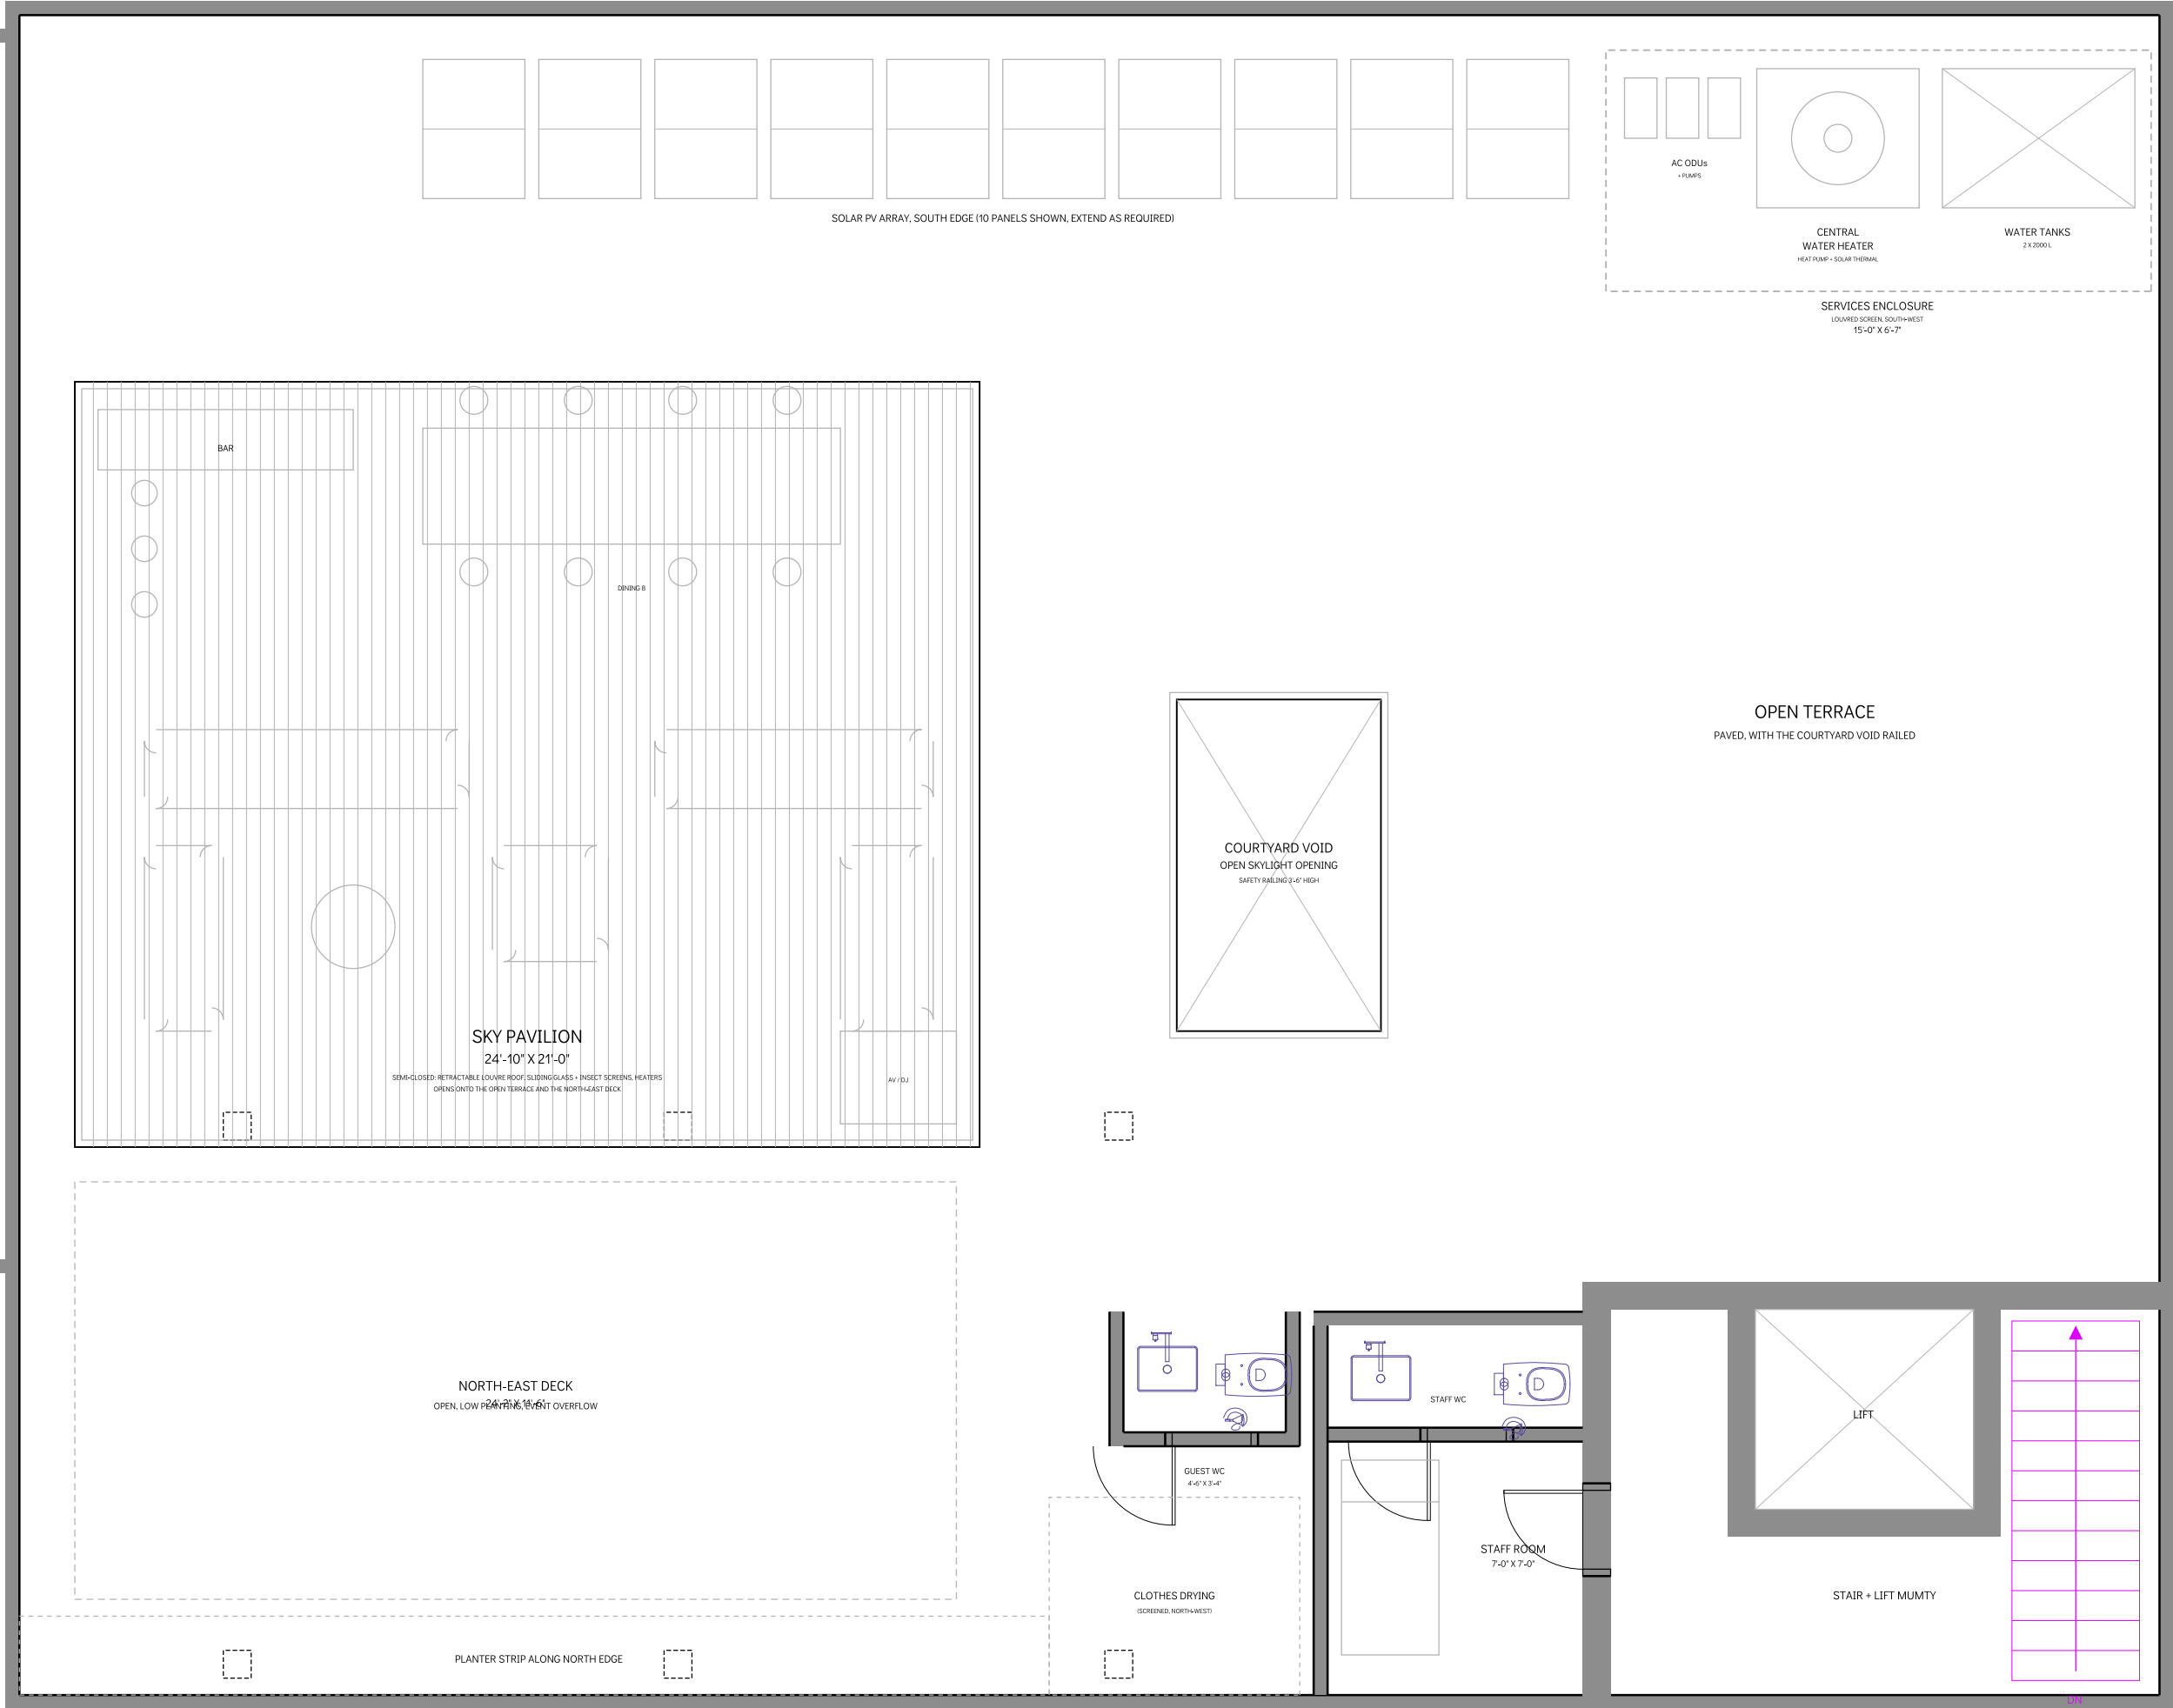

NOTES (TERRACE, R5):  
1. PARAPET 3'-6" HIGH ALL ROUND; COURTYARD VOID RAILED. 2. WATER TANKS, CENTRAL WATER HEATER, AC OUTDOOR UNITS AND PUMPS IN A LOUVRED SERVICES ENCLOSURE IN THE SOUTH-WEST; SOLAR PV ALONG THE SOUTH PARAPET; NORTH-EAST KEPT OPEN AND LOW (VASTUI).  
3. SKY PAVILION ON THE EAST: STEEL FRAME, RETRACTABLE LOUVRE ROOF, SLIDING GLASS WITH INSECT SCREENS, BAR, DINING AND LOUNGE; POWER AND WATER TO THE BAR. 4. STAFF ROOM, WC, GUEST WC AND SCREENED DRYING YARD BESIDE THE MUMTY (NORTH-WEST).  
5. TERRACE SLAB OVER THE NORTH WING CARRIED ON THE EXTERNAL COLUMNS (DASHED); PAVILION AND SERVICES LOADS TO BE CHECKED BY THE STRUCTURAL ENGINEER. 6. WATERPROOFING AND SLOPES TO NORTH-EAST DRAIN POINTS.