
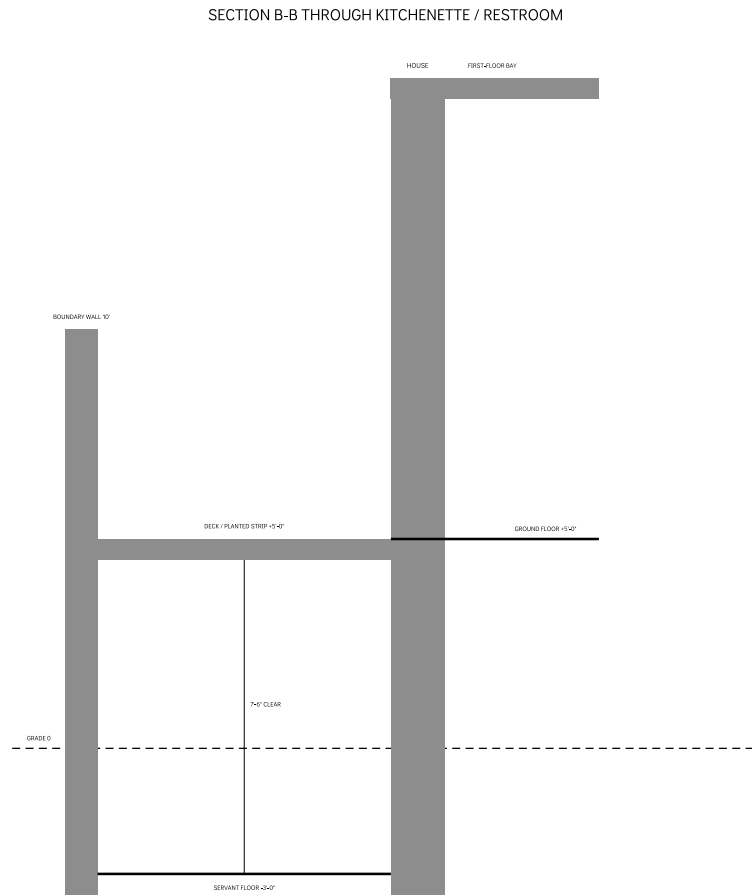
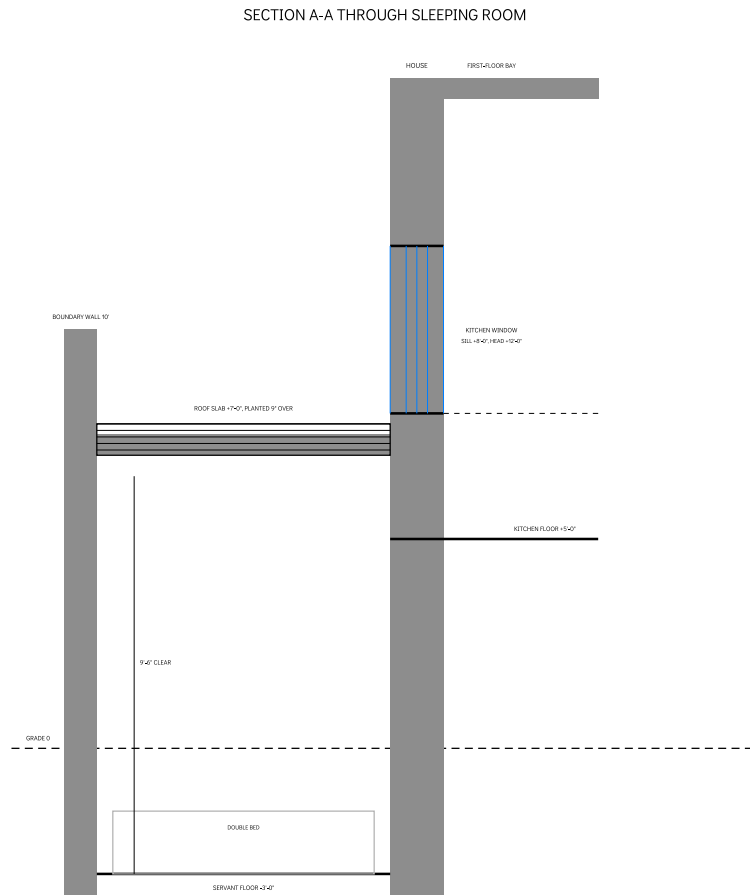


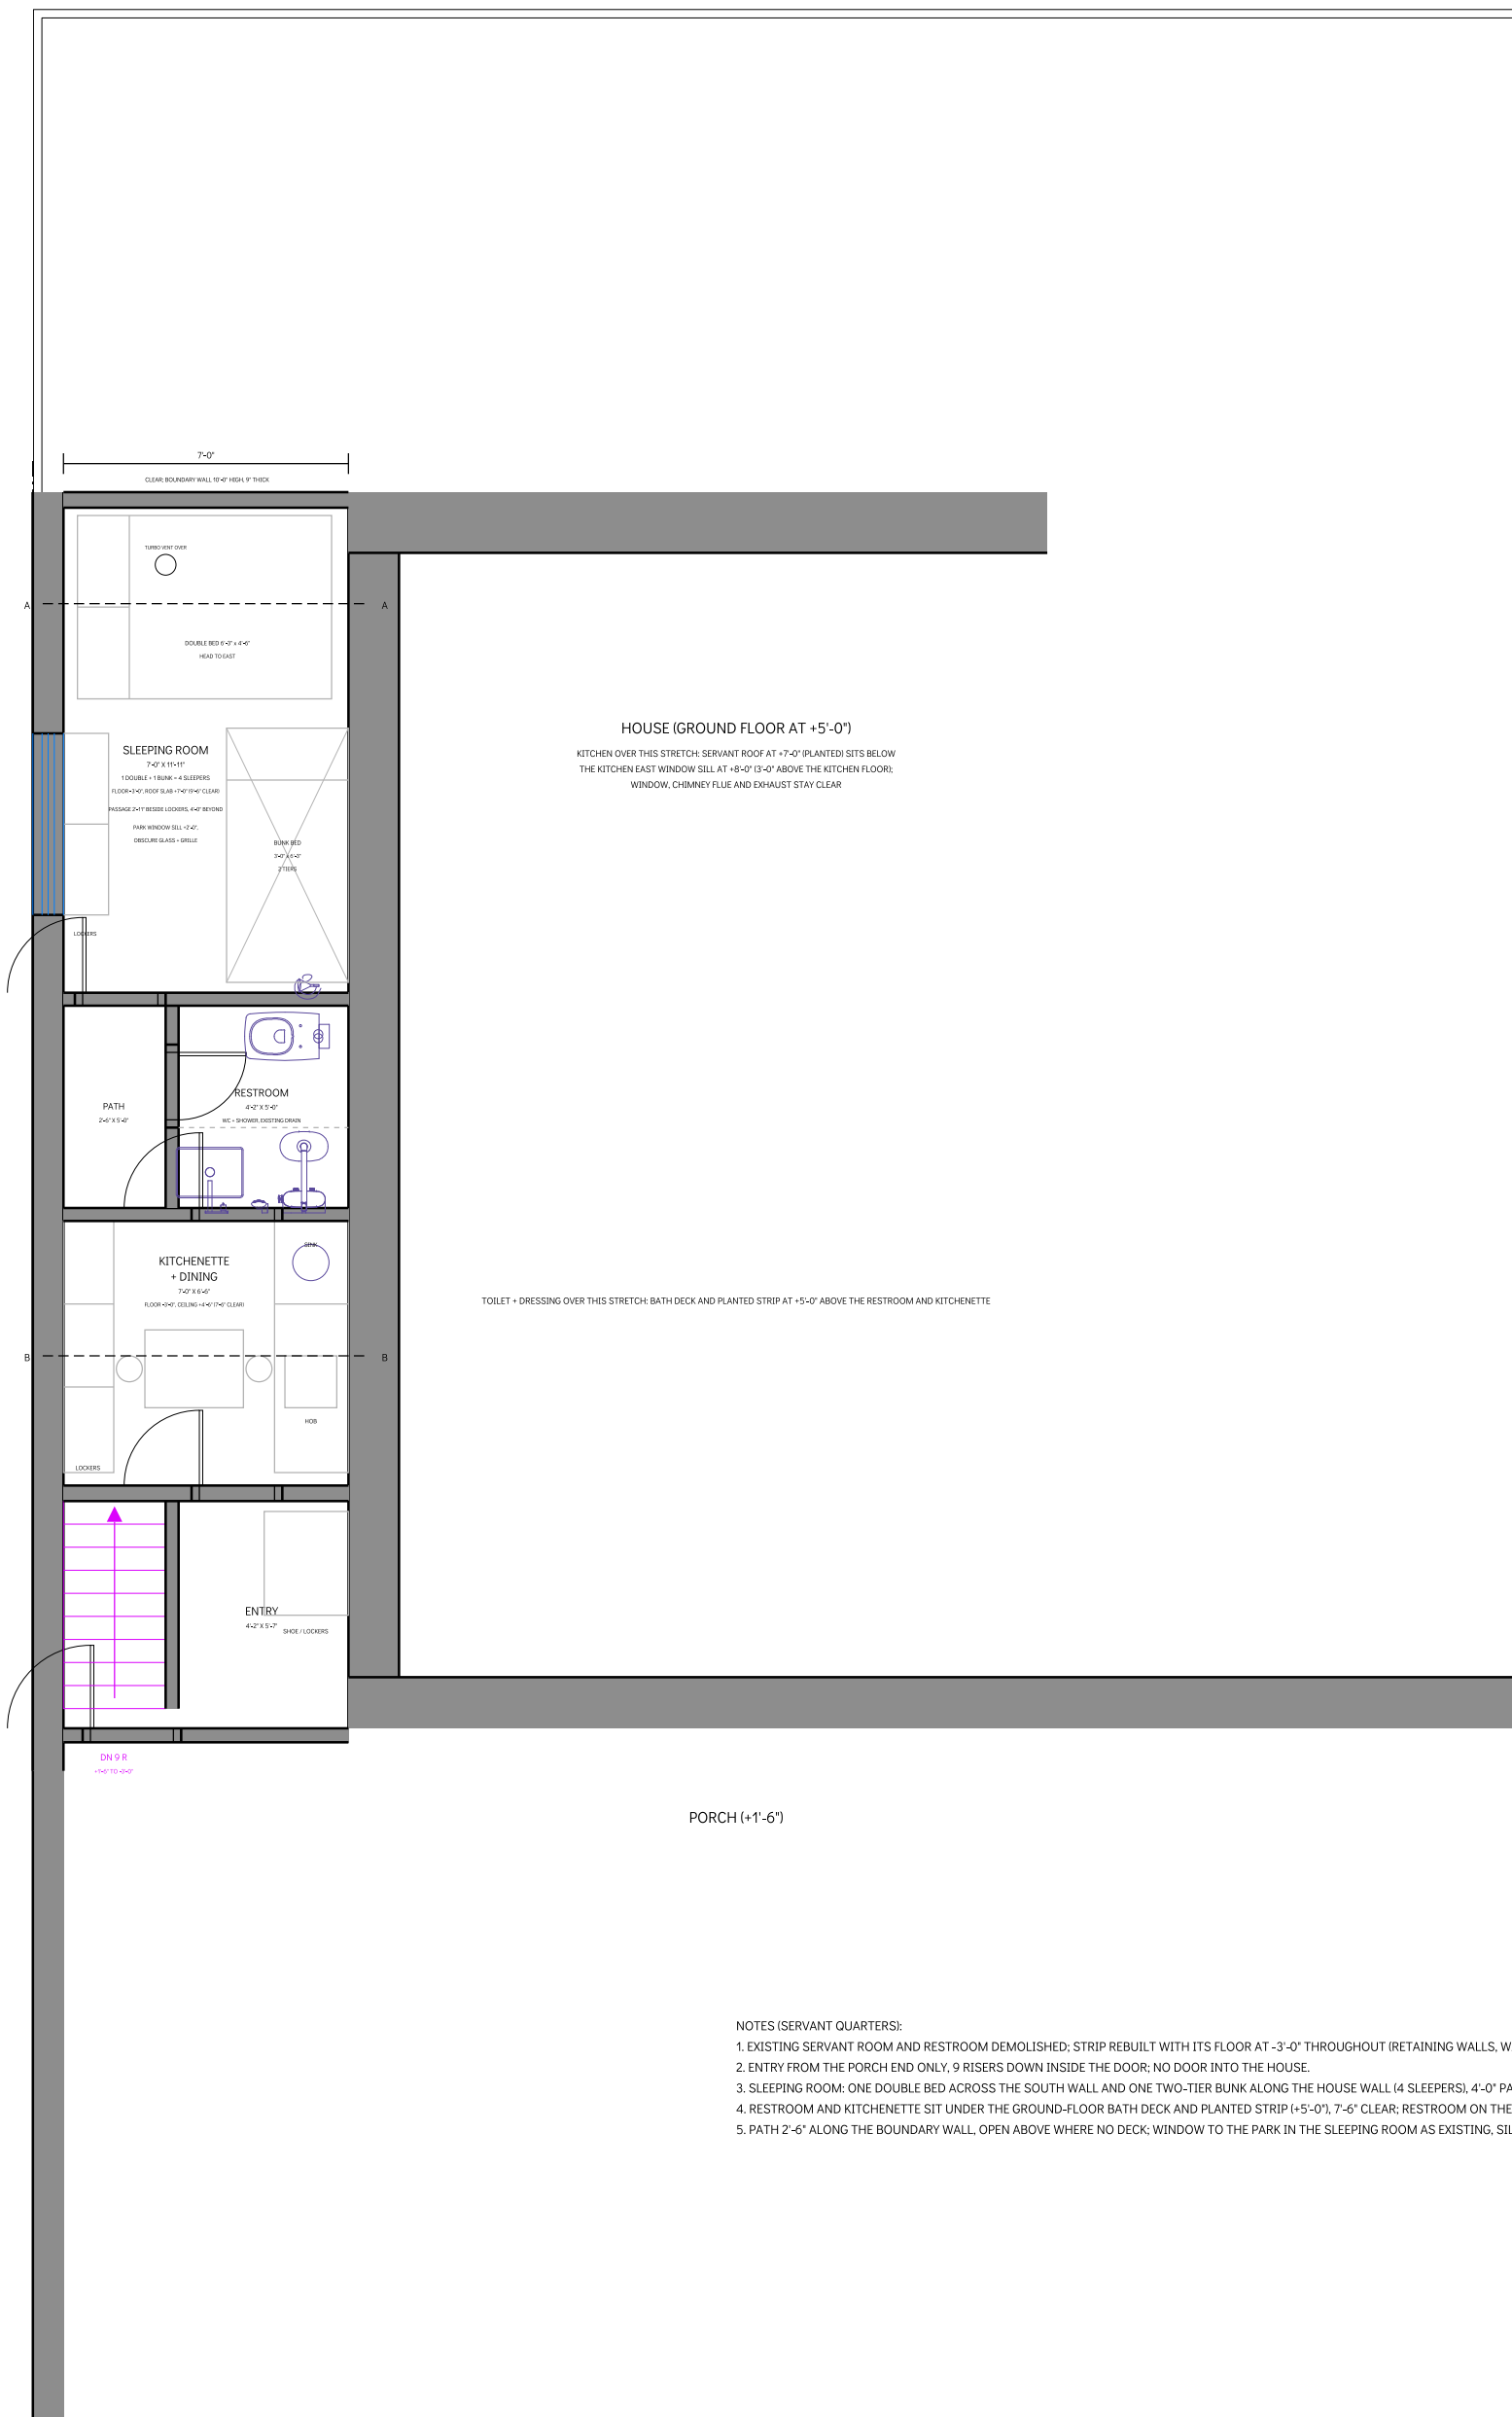

SERVANT QUARTERS - GRADE LEVEL LAYOUT

- NOTES (SERVANT QUARTERS):
- EXISTING SERVANT ROOM AND RESTROOM DEMOLISHED; STRIP REBUILT WITH ITS FLOOR AT -3'-0" THROUGHOUT (RETAINING WALLS, WATERPROOFED, SUMP + PUMP FOR DRAINAGE).
 - ENTRY FROM THE PORCH END ONLY, 9 RISERS DOWN INSIDE THE DOOR; NO DOOR INTO THE HOUSE.
 - SLEEPING ROOM: ONE DOUBLE BED ACROSS THE SOUTH WALL AND ONE TWO-TIER BUNK ALONG THE HOUSE WALL (4 SLEEPERS); 4'-0" PASSAGE WITH LOCKERS UNDER THE PARK WINDOW. SINGLE HEIGHT: FLOOR -3'-0"; ROOF SLAB AT +7'-0" (9'-6" CLEAR) PLANTED OVER; KEPT BELOW THE KITCHEN EAST WINDOW SILL AT +8'-0" SO THE KITCHEN KEEPS ITS WINDOW, CHIMNEY FLUE AND EXHAUST. TURBO VENT IN THE ROOF.
 - RESTROOM AND KITCHENETTE SIT UNDER THE GROUND-FLOOR BATH DECK AND PLANTED STRIP (15'-0", 7'-6" CLEAR; RESTROOM ON THE EXISTING DRAIN, HIGH-LEVEL VENT TO THE PATH).
 - PATH 2'-6" ALONG THE BOUNDARY WALL, OPEN ABOVE WHERE NO DECK; WINDOW TO THE PARK IN THE SLEEPING ROOM AS EXISTING, SILL +2'-0" (5'-0" ABOVE THE SERVANT FLOOR), OBSCURE GLASS WITH A GRILLE. ALL DIMENSIONS ARE CLEAR INTERNAL SIZES.

SQ-PP-02